


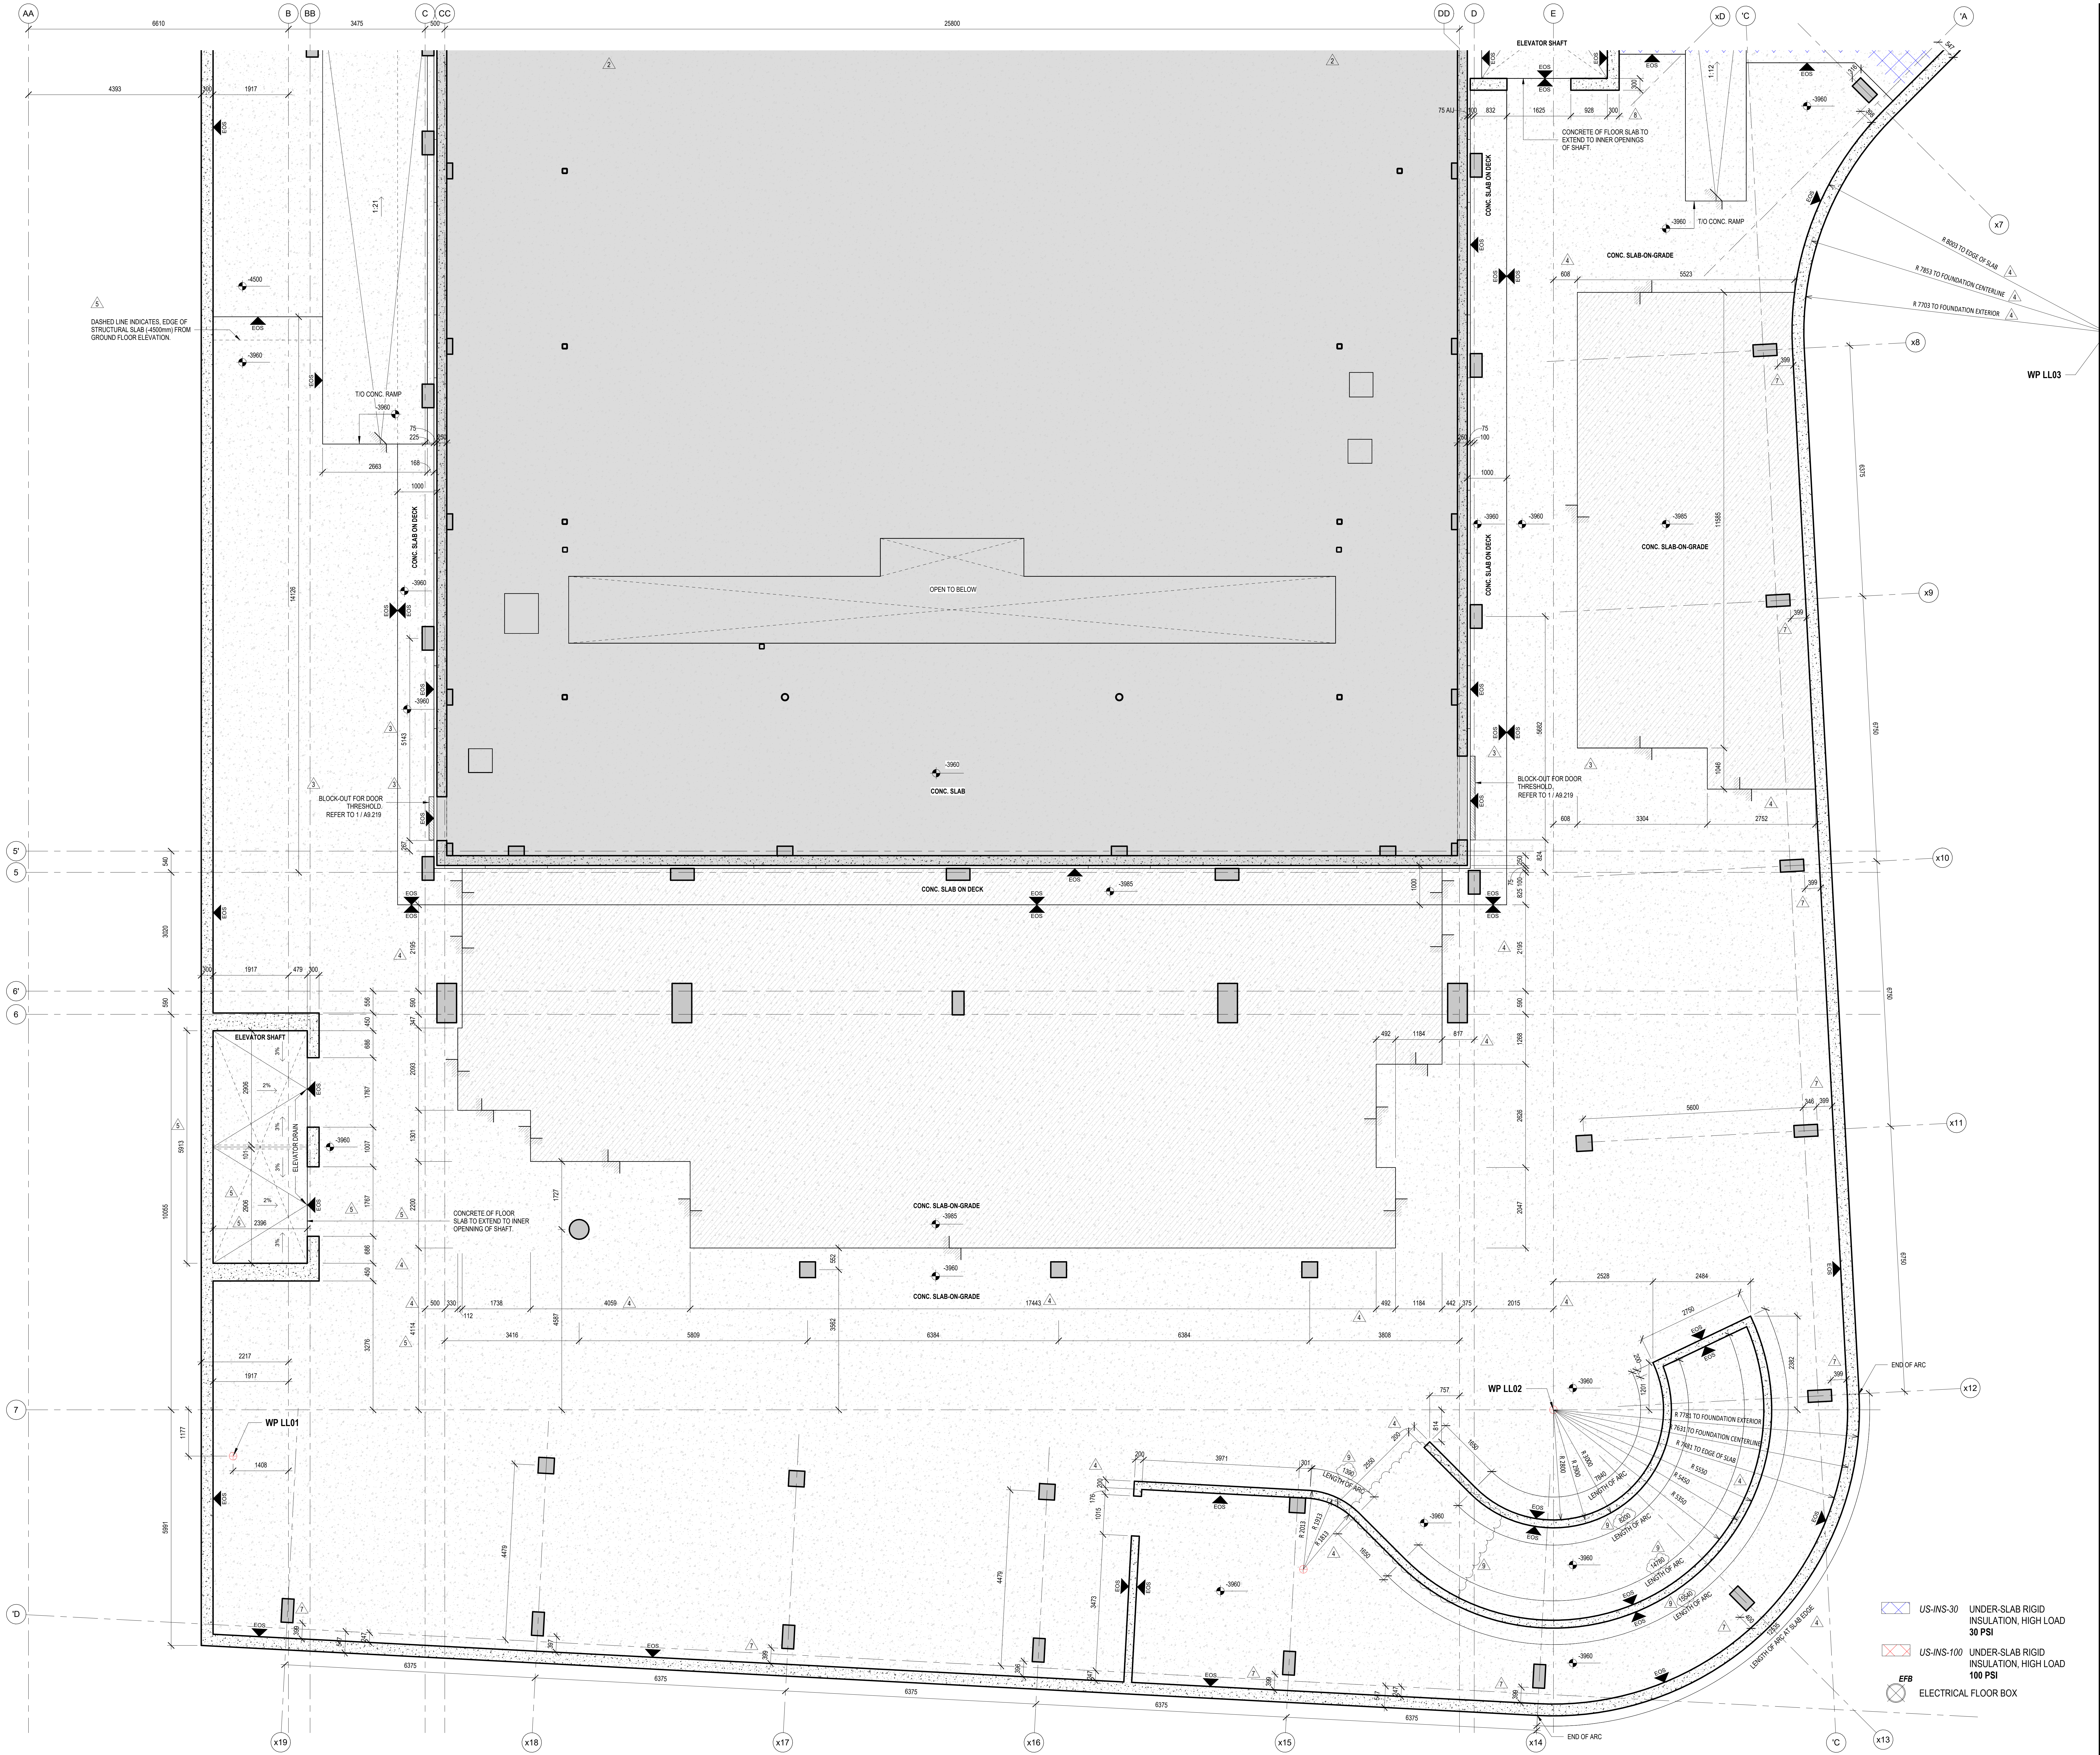

COPYRIGHT IS THAT OF THE ARCHITECT.
ANY USE OF THIS DRAWING REPRODUCED BY ANY
PERSON FOR ANY REASON WITHOUT THE WRITTEN
APPROVAL OF THE ARCHITECT IS TO BE REJECTED.
THE ARCHITECT IS NOT LIABLE FOR ANY LOSS OR
DAMAGE OF ANY KIND OR IN ANY MANNER
SUBSEQUENT REPRODUCTION OF THE ORIGINAL DRAWING.

GENERAL NOTES:

- DRAWINGS ARE NOT TO BE SCALED. CONTRACTOR SHALL VERIFY ALL EXISTING CONDITIONS AND CONDITIONS REQUIRED TO PERFORM THE WORK AND ALL REPORT ANY DISCREPANCIES WITH THE CONTRACT DOCUMENTS TO THE ARCHITECT BEFORE COMMENCING WORK.
- THE ARCHITECTURAL DRAWINGS ARE TO BE READ IN CONJUNCTION WITH ALL OTHER CONTRACT DOCUMENTS INCLUDING THE PROJECT MANUAL AND THE STRUCTURAL, MECHANICAL, ELECTRICAL, AND PLUMBING SPECIFICATIONS. DIFFERENCES BETWEEN THE CONTRACT DOCUMENTS WITH RESPECT TO THE QUANTITY, COST OR SCOPE OF WORK, THE CONTRACT SHALL PREVAIL.
- POSITIONS OF EXPOSED OR FINISHED MECHANICAL OR ELECTRICAL ACCESS FITTINGS AND PIPES ARE INDICATED ON THE ARCHITECTURAL DRAWINGS. LOCATIONS SHOWN ON THE ARCHITECTURAL DRAWINGS SHALL GOVERN OVER MECHANICAL AND ELECTRICAL WORKING DRAWINGS. MECHANICAL AND ELECTRICAL ITEMS NOT CLEARLY LOCATED WILL BE LOCATED AS DIRECTED BY THE ARCHITECT.
- OVERLAP INDICATED ARE TAKEN BETWEEN THE FACES OF THE STRUCTURAL MEMBERS UNLESS OTHERWISE NOTED.
- THE ARCHITECT HAS NOT BEEN RETAINED FOR SUPERVISION OF CONSTRUCTION AND ASSUMES NO RESPONSIBILITY FOR MEANS, METHODS AND TECHNIQUES OF CONSTRUCTION.
- THESE DOCUMENTS ARE NOT TO BE USED FOR CONSTRUCTION UNLESS SPECIFICALLY NOTED FOR SUCH PURPOSE.

NO.	DESCRIPTION	DATE
1	ISSUED FOR BIDDING	2024-06-28
2	ISSUED FOR BIDDING	2024-06-28
KEY PLAN

SCALE

ARCHITECTS

KPMB

KPMB Architects
351 King Street East, Suite 1200
Toronto, Canada M5A 0L6
+1 416 577 5104
kpmb@kpmbarchitects.com

HINDLE ARCHITECTS

Hindle Architects
Suite 510, Burns Building
237 8th Avenue SE
Calgary, AB
T2G 0C3

TAW

Tawana Architecture Collective
8003, 118 5 Ave SE
Calgary, AB T2G 0T1
(403) 451 0294

CMILC

**Arts Commons Transformation
Phase 1 Expansion**

ACT

200 8th Avenue S.E. Calgary, Alberta

Project North **True North**

Project No. 2041
Scale As indicated
Plot Date 2024-06-28

**ENLARGED SLAB EDGE
PLAN - LOWER LEVEL - S**


A2.402



COPYRIGHT IS THAT OF THE ARCHITECT.
ANY USE OF THIS DRAWING REPRODUCED BY ANY
PERSON FOR ANY REASON WITHOUT THE WRITTEN
APPROVAL OF THE ARCHITECT IS TO BE REJECTED.
THE ARCHITECT IS NOT LIABLE FOR ANY LOSS OR
DAMAGE OF INFORMATION RESULTING FROM
SUBSEQUENT REPRODUCTION OF THE ORIGINAL DRAWING.

- GENERAL NOTES:
1. DRAWINGS ARE NOT TO BE SCALED. CONTRACTOR SHALL VERIFY ALL EXISTING CONDITIONS AND DIMENSIONS PRIOR TO PERFORMING THE WORK AND SHALL REPORT ANY DISCREPANCIES WITHIN THE CONTRACT DOCUMENTS TO THE ARCHITECT FOR THE CONTRACT DOCUMENTS.
 2. THE ARCHITECTURAL DRAWINGS ARE TO BE READ IN CONJUNCTION WITH ALL OTHER CONTRACT DOCUMENTS INCLUDING THE PROJECT MANUAL AND THE STRUCTURAL, MECHANICAL, ELECTRICAL, AND PLUMBING (M-E-P) SPECIFICATIONS. THE CONTRACTOR SHALL BE RESPONSIBLE FOR THE DIFFERENCE BETWEEN THE CANAL LIMIT DOCUMENTS WITH RESPECT TO THE QUANTITY, COST OR SCOPE OF WORK. 
 3. POSITIONS OF EXISTING OR PROPOSED MECHANICAL OR ELECTRICAL EQUIPMENT AND FITTINGS ARE INDICATED ON THE ARCHITECTURAL DRAWINGS. LOCATIONS SHOWN ON THE ARCHITECTURAL DRAWINGS SHALL GOVERN OVER ANY OTHER TECHNICAL DRAWINGS. MECHANICAL AND ELECTRICAL ITEMS NOT CLEARLY LOCATED WILL BE LOCATED AS DIRECTED BY THE ARCHITECT.
 4. DIMENSIONS INDICATED ARE TAKEN BETWEEN THE FACES UNLESS OTHERWISE SPECIFIED. DIMENSIONS SHALL BE TAKEN FROM THE FACE OF THE MEMBER UNLESS OTHERWISE SPECIFIED.
 5. THE ARCHITECT HAS NOT BEEN ADVISED FOR SUPERVISION OF CONSTRUCTION AND ASSUMES NO RESPONSIBILITY FOR MEANS, METHODS AND TECHNIQUES OF CONSTRUCTION.
 6. THESE DOCUMENTS ARE NOT TO BE USED FOR CONSTRUCTION UNLESS SPECIFICALLY NOTED FOR SUCH PURPOSE.

1	2024-11-13	ISSUED FOR BIDDING
2	2024-11-13	ISSUED FOR BIDDING
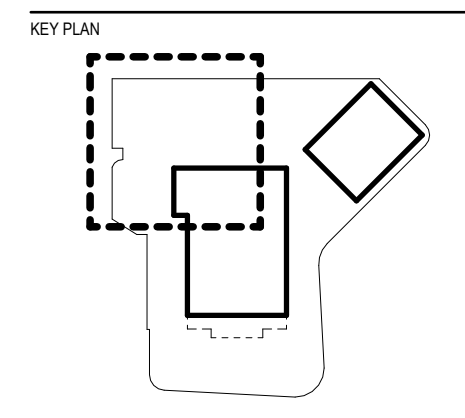

ARCHITECTS

KPMB

KPMB Architects
351 King Street East, Suite 1200
Toronto, Canada M5A 0L6
+1 416 577 5104
kpmbs@kpmbarchitects.com

HINDLE ARCHITECTS

Hindle Architects
Suite 510, Burns Building
237 8th Avenue SE
Calgary, AB
T2G 0C3

TAW


Taw Architecture Collective
8203, 118 1 Ave SE
Calgary, AB T2G 0T1
(403) 451 0294

CMIC

Arts Commons Transformation
Phase 1 Expansion

ACT

206 8th Avenue S.E. Calgary, Alberta

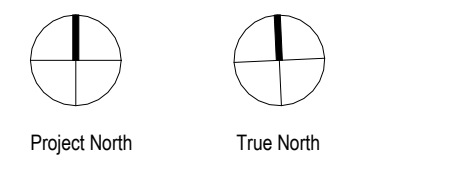

Project No. 2041
Scale 1:50
Plot Date 2024-06-28

ENLARGED SLAB EDGE
PLAN - LEVEL 3 - NW

A2.430

THE ARCHITECT IS NOT LIABLE FOR ANY LOSS OR
DISTORTION OF INFORMATION RESULTING FROM
SUBSEQUENT REPRODUCTION OF THE ORIGINAL DRAWING.

DRAWINGS. NOT TO BE SCALED. CONTRACTOR WILL VERIFY DIMENSIONS, CONSTRUCTION AND DIMENSIONS REQUIRED TO CONFORM TO THE WORK AND WILL REPORT ANY DISCREPANCIES WITH CONTRACT DOCUMENTS TO THE ARCHITECT IMMEDIATELY UPON DISCOVERY. THE ARCHITECTURAL DRAWINGS ARE TO BE READ IN CONJUNCTION WITH THE SPECIFICATIONS AND NOTES INCLUDING THE PROJECT MANUALS AND THE STRUCTURAL, MECHANICAL AND ELECTRICAL DRAWINGS. IN CASES OF CONFLICT, THE SPECIFICATIONS SHALL PREVAIL. DIMENSIONS WITH RESPECT TO THE QUANTITY, SCOPE OR SCOPE OF WORK, THE GREATER SHALL APPLY.


POSITIONS, IDENTIFICATION, MECHANICAL OR ELECTRICAL DEVICES, FITTINGS AND FIXTURES ARE INDICATED ON THE ARCHITECTURAL DRAWINGS. LOCATIONS OF MECHANICAL AND ELECTRICAL DEVICES SHALL GOVERN OVER MECHANICAL AND ELECTRICAL DRAWINGS. MECHANICAL AND ELECTRICAL ITEMS NOT CLEARLY LOCATED SHALL BE LOCATED AS DIRECTED BY THE ARCHITECT.

DIMENSIONS INDICATED ARE IN FEET BETWEEN THE FACES OF DIMENSIONED PARTS UNLESS OTHERWISE NOTED. THE ARCHITECT HAS NOT BEEN RETAINED FOR SUPERVISION OF CONSTRUCTION AND ASSUMES NO RESPONSIBILITY FOR MEASUREMENTS, METHODS AND TECHNIQUES OF CONSTRUCTION.

THESE DOCUMENTS ARE NOT TO BE USED FOR CONSTRUCTION UNLESS SPECIFICALLY NOTED FOR SUCH PURPOSE.

3	2025-11-21	ISSUED FOR S-620
2	2025-09-30	ISSUED FOR CONSOLIDATION
1	2025-04-01	ISSUED FOR TENDER PACKAGE 2

KEY PLAN

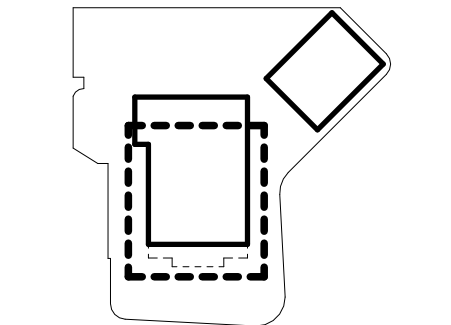

EN



ARCHITECTS

KPMB

KPMB Architects
61 King Street East, Suite 1200
Toronto, Canada M5A 0L6
+1 416 977 5104
kpm@kpmarchitects.com


HINDLE ARCHITECT

Kindle Architects
Suite 510, Burns Building
137 8th Avenue SE
Calgary, AB
T2G 5C3

TAW
Taww Architecture Collective
203, 1218 9 Ave SE
Calgary, AB T2G 0T1
(403) 431 0294

Arts Commons Transformation Phase 1 Expansion

ACT

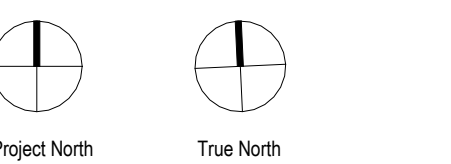

Project No.	2041
Scale	1 : 50
Plot Date	2024-06-28


ENLARGED SLAB EDGE
PLAN - LEVEL 2 - LARGE
HALL

A2.463

COPYRIGHT IS THAT OF THE ARCHITECT.
 ANY VERSION OF THIS DRAWING REPRODUCED BY ANY
 MEANS FROM ANY MEDIA WITHOUT PRIOR WRITTEN
 APPROVAL OF THE ARCHITECT IS TO BE READ FOR
 INFORMATION ONLY.
 THE ARCHITECT IS NOT LIABLE FOR ANY LOSS OR
 DISTORTION OF INFORMATION RESULTING FROM
 SUBSEQUENT REPRODUCTION OF THE ORIGINAL DRAWING.

DRAWINGS ARE NOT TO SCALE. CONTRACTOR WILL
VERIFY ALL EXISTING CONDITIONS AND DIMENSIONS
BEFORE PERFORMING THE WORK AND WILL REPORT ANY
DISCREPANCIES WITH THE CONTRACT DOCUMENTS TO THE
ARCHITECT IMMEDIATELY UPON DISCOVERY.
THE ARCHITECTURAL DRAWINGS ARE TO BE READ IN
CONJUNCTION WITH ALL OTHER CONTRACT DOCUMENTS
AND SPECIFICATIONS. THE ARCHITECTURAL DRAWINGS
MECHANICAL AND ELECTRICAL DRAWINGS. IN CASES OF
DIFFERENCE BETWEEN THE CONSULTANT'S DOCUMENTS
WITH RESPECT TO QUALITY, SIZE OR SCOPE OF
WORK, THE MECHANICAL, ELECTRICAL AND PLUMBING
POSITIONS OF EXPOSED OR FINISHED MECHANICAL,
OR ELECTRICAL DEVICES, FITTINGS AND FIXTURES ARE
TO GOVERN OVER THE ARCHITECTURAL DRAWINGS.
ALL DIMENSIONS SHOWN ON THE ARCHITECTURAL DRAWINGS SHALL COVER
OVER MECHANICAL AND ELECTRICAL DRAWINGS.
LOCATIONS OF ALL MECHANICAL AND ELECTRICAL
EQUIPMENT SHALL BE LOCATED AS DIRECTED BY THE
ARCHITECT.
DIMENSIONS INDICATED ARE TAKEN BETWEEN THE FACE
OF FINISHED SURFACES UNLESS OTHERWISE NOTED.
THE ARCHITECT HAS NOT BEEN RETAINED FOR
STRUCTURAL DESIGN. THE CONTRACTOR ASSUMES ALL
RESPONSIBILITY FOR MEANS, METHODS AND TECHNIQUES
OF CONSTRUCTION.
THESE DOCUMENTS ARE NOT TO BE USED FOR
ANY PURPOSE OTHER THAN SPECIFICALLY NOTED FOR SUCH
PURPOSE.

3	2025-11-21	ISSUED FOR S1-600
2	2025-09-30	ISSUED FOR CONSOLIDATION
1	2025-04-01	ISSUED FOR TENDER PACKAGE 2

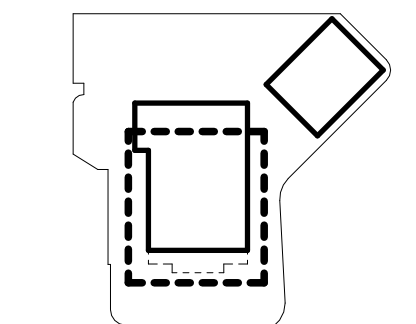

KPMB


KPMB Architects
51 King Street East, Suite 1200
Toronto, Canada M5A 0L6
+1 416 977 5104
pmb@kpmbarchitects.com

Hindle Architects
Suite 510, Burns Building
37 8th Avenue SE
Calgary, AB

TAW
Tawaw Architecture Collective
203, 1218 9 Ave SE
Calgary, AB T2G 0T1
(403) 431 0294

Arts Commons Transformation Phase 1 Expansion

06 8th Avenue S.E. Calgary, Alberta

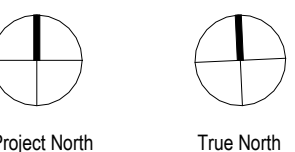

Project No.	2041
Scale	1 : 50
Plot Date	2024-06-2

ENLARGED SLAB EDGE
PLAN - LEVEL 3 - LARGE
HALL


A2.464

THE ARCHITECT IS NOT LIABLE FOR ANY LOSS OR
DISTORTION OF INFORMATION RESULTING FROM
SUBSEQUENT REPRODUCTION OF THE ORIGINAL DRAWING.

LOCAL NOTES:
DRAWINGS ARE NOT TO BE SCALED. CONTRACTOR WILL VERIFY ALL EXISTING CONDITIONS AND DIMENSIONS REQUIRED TO PERFORM THE WORK AND WILL REPORT ANY DISCREPANCIES WITH THE CONTRACT DOCUMENTS TO THE ARCHITECT BEFORE PROCEEDING.
THE ARCHITECTURAL DRAWINGS ARE TO BE READ IN CONJUNCTION WITH THE STRUCTURAL DRAWINGS, INCLUDING THE PROJECT MANUALS AND THE STRUCTURAL, MECHANICAL AND ELECTRICAL DRAWINGS. IN CASES OF DISCREPANCIES BETWEEN THE CONTRACT DOCUMENTS WITH RESPECT TO THE QUANTITY, SCOPE OR SCOPE OF WORK, THE GREATER SHALL APPLY.
DIMENSIONS OF MECHANICAL AND ELECTRICAL DEVICES, FITTINGS AND FIXTURES ARE INDICATED ON THE ARCHITECTURAL DRAWINGS. LOCATIONS OF MECHANICAL AND ELECTRICAL DEVICES GOVERN OVER MECHANICAL AND ELECTRICAL DIMENSIONS.
MECHANICAL AND ELECTRICAL ITEMS NOT CLEARLY LOCATED MUST BE LOCATED AS DIRECTED BY THE ARCHITECT.
DIMENSIONS INDICATED ARE TAKEN BETWEEN THE FACES UNLESS OTHERWISE NOTED.
THE ARCHITECT HAS NOT BEEN RETAINED FOR SUPERVISION OF CONSTRUCTION AND ASSUMES NO RESPONSIBILITY FOR MEANS, METHODS AND TECHNIQUES OF CONSTRUCTION.
THESE DOCUMENTS ARE NOT TO BE USED FOR CONSTRUCTION UNLESS SPECIFICALLY NOTED FOR SUCH PURPOSE.

3	2025-11-21	ISSUED FOR S-I-EI
2	2025-06-30	ISSUED FOR CONSOLIDATION
1	2025-04-01	ISSUED FOR TENDER PACKAGE 2

KEY PLAN

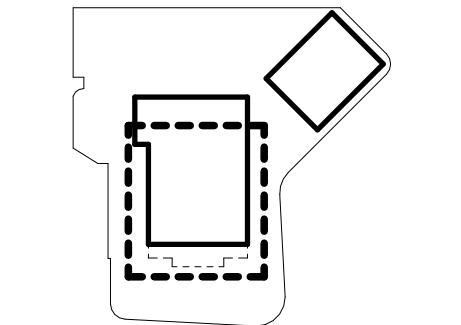

KPMB

KPMB Architects
61 King Street East, Suite 1200
Toronto, Canada M5A 0L6
+1 416 977 5104
pmb@kpmbarchitects.com

HINDLE ARCHITECTS


Hindle Architects
Suite 510, Burns Building
37 8th Avenue SE
Calgary, AB
T2G 5C3

TAW
Tawaw Architecture Collective
200, 1218 9 Ave SE
Calgary, AB T2G 0T1
(403) 431 0294

Arts Commons Transformation Phase 1 Expansion

ACT













05 8th Avenue S.E. Calgary, Alberta

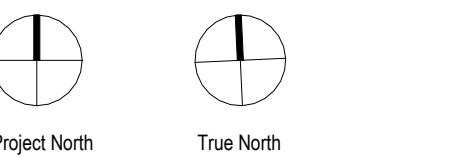

Project No. 2041
Scale 1 : 50
Plot Date 2024-06-28

ENLARGED SLAB EDGE
PLAN - LEVEL 4 - LARGE
HALL

A2.465

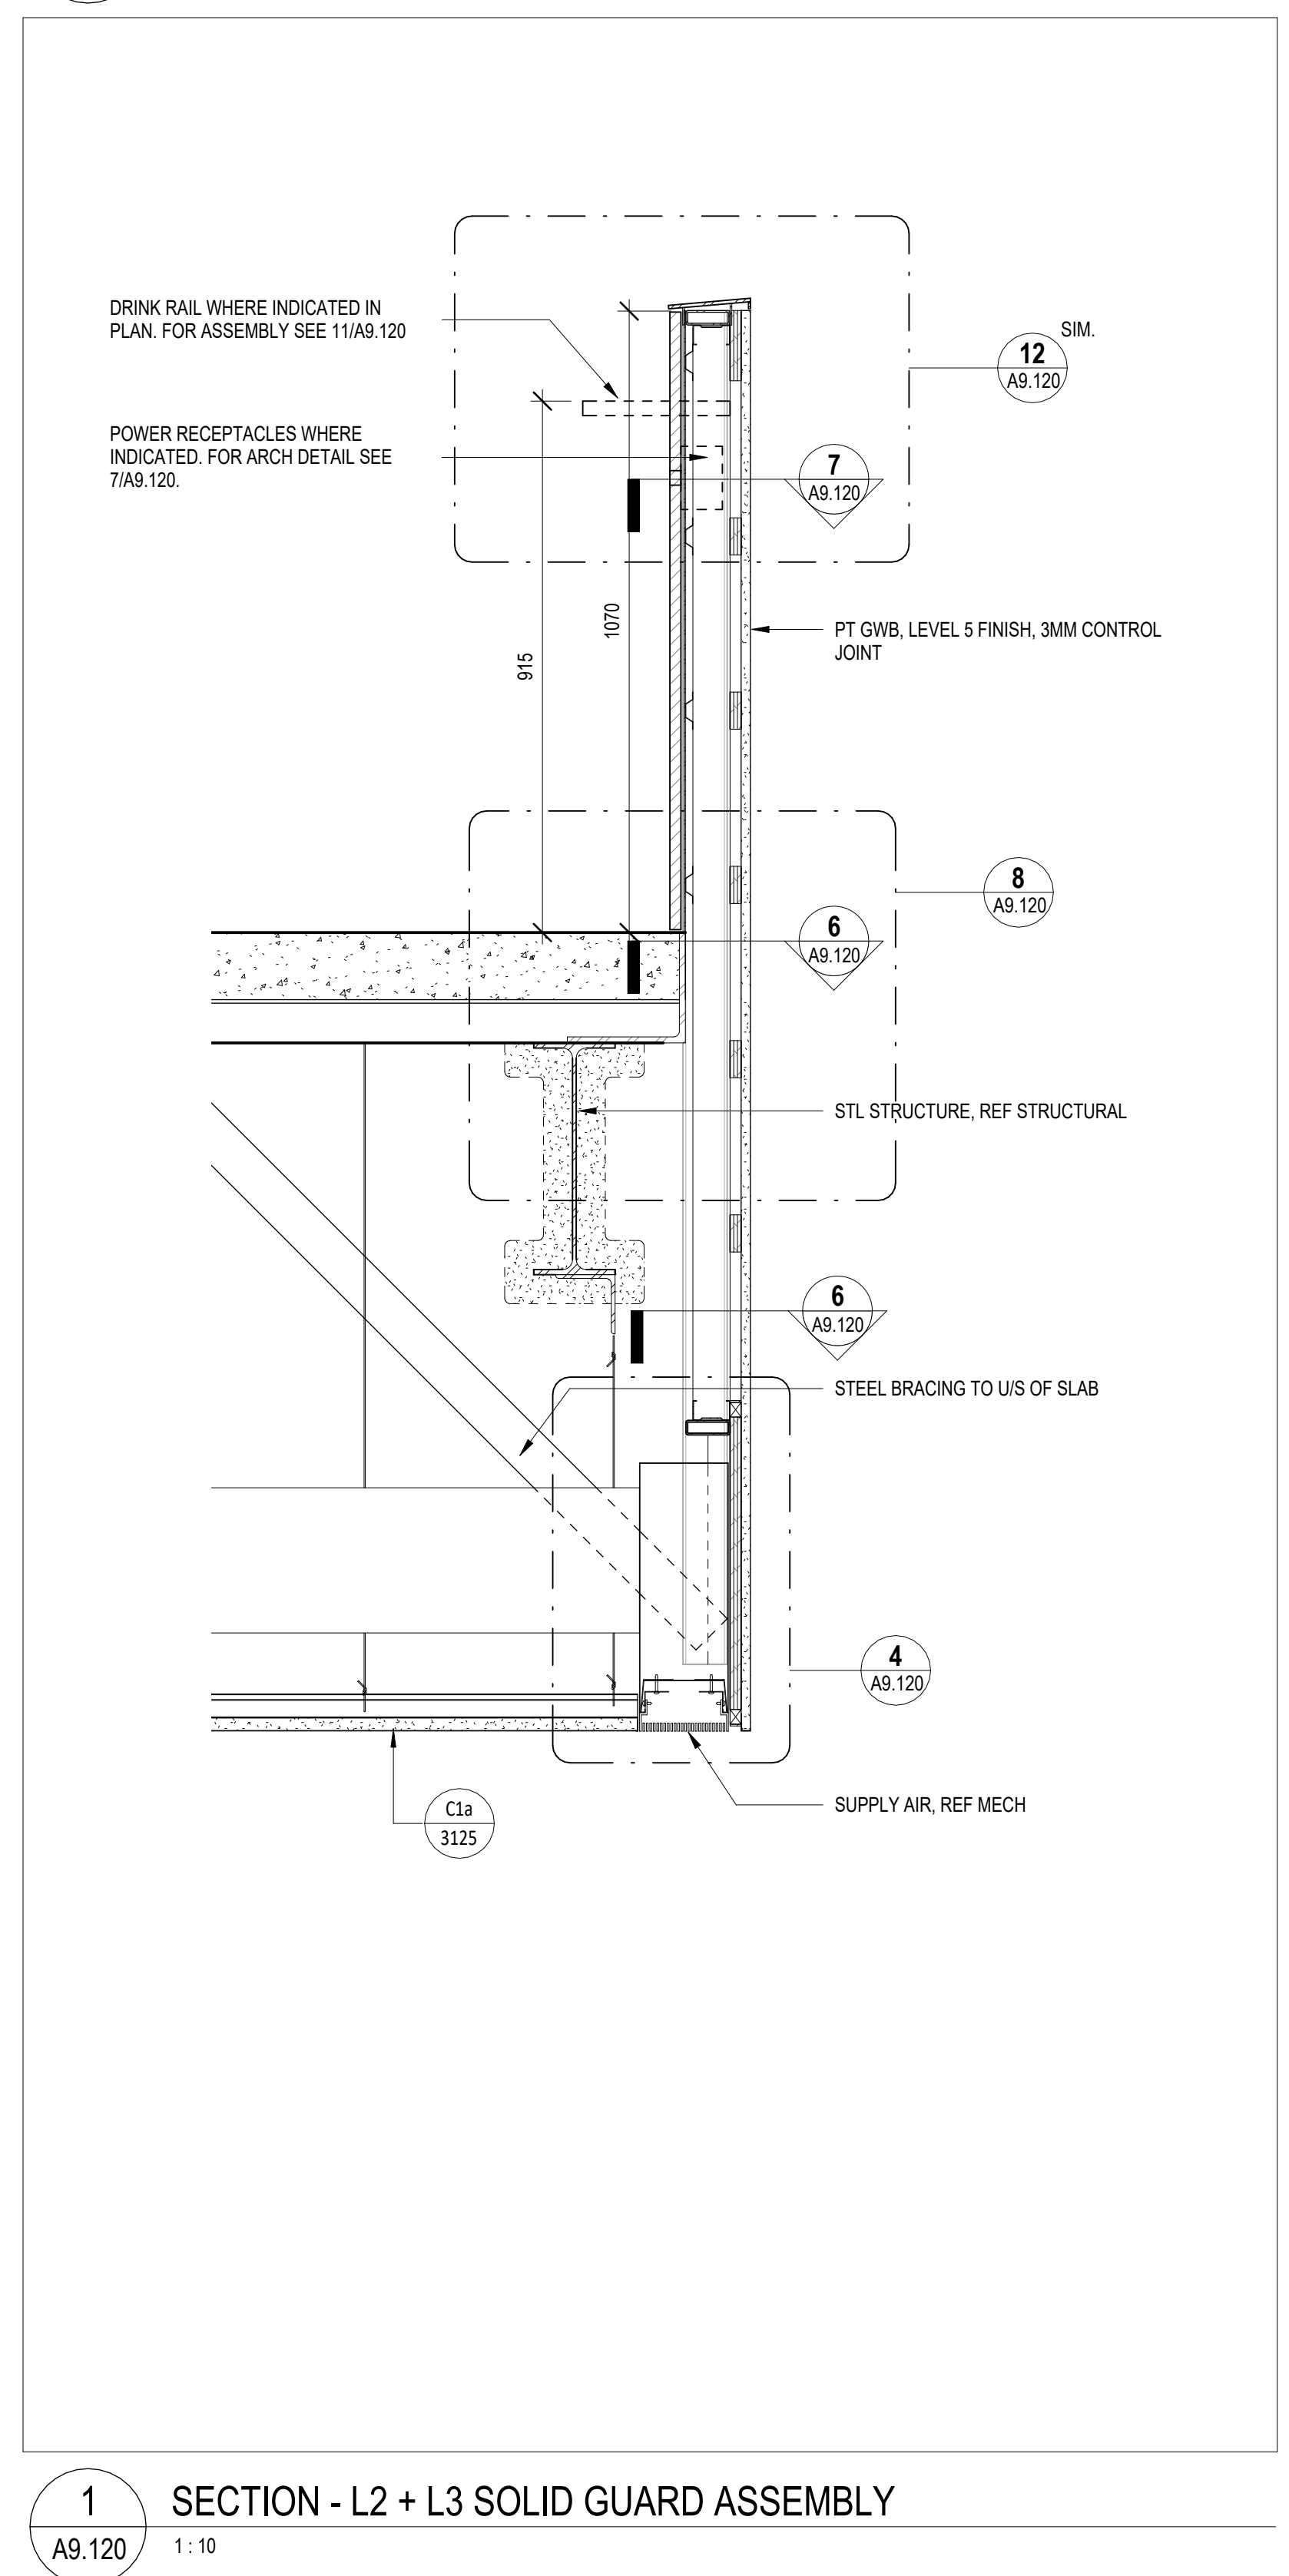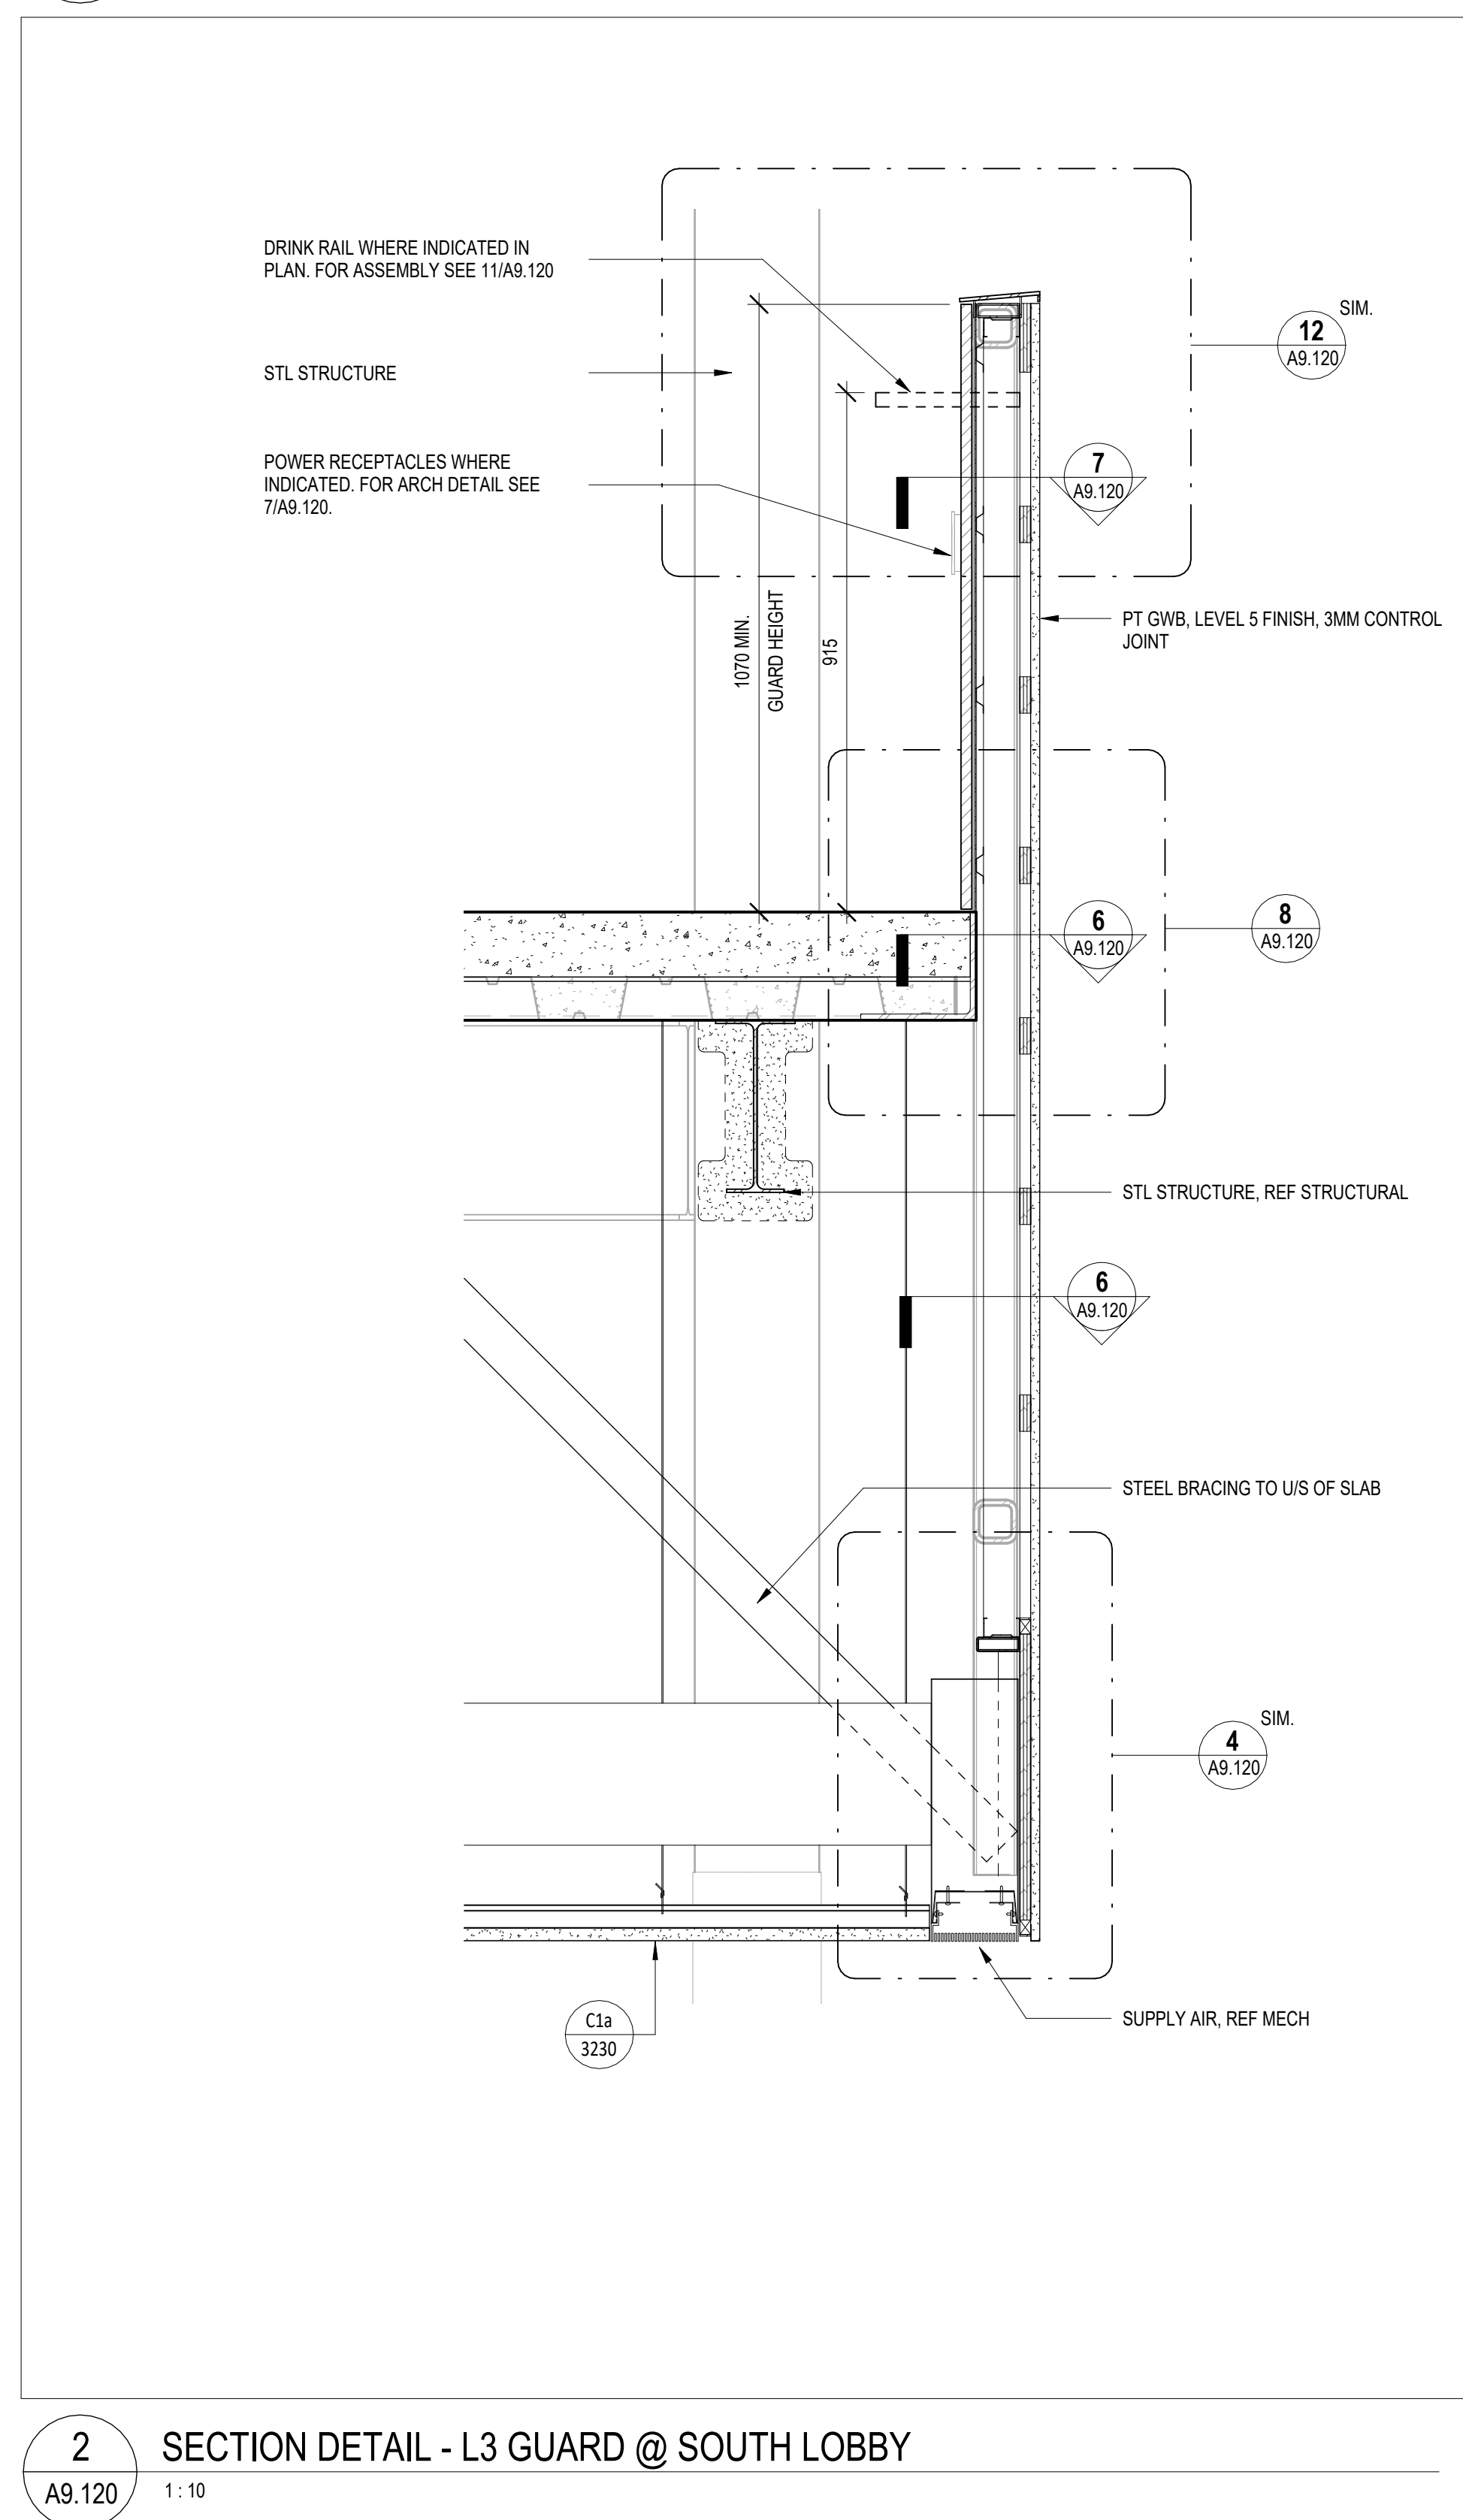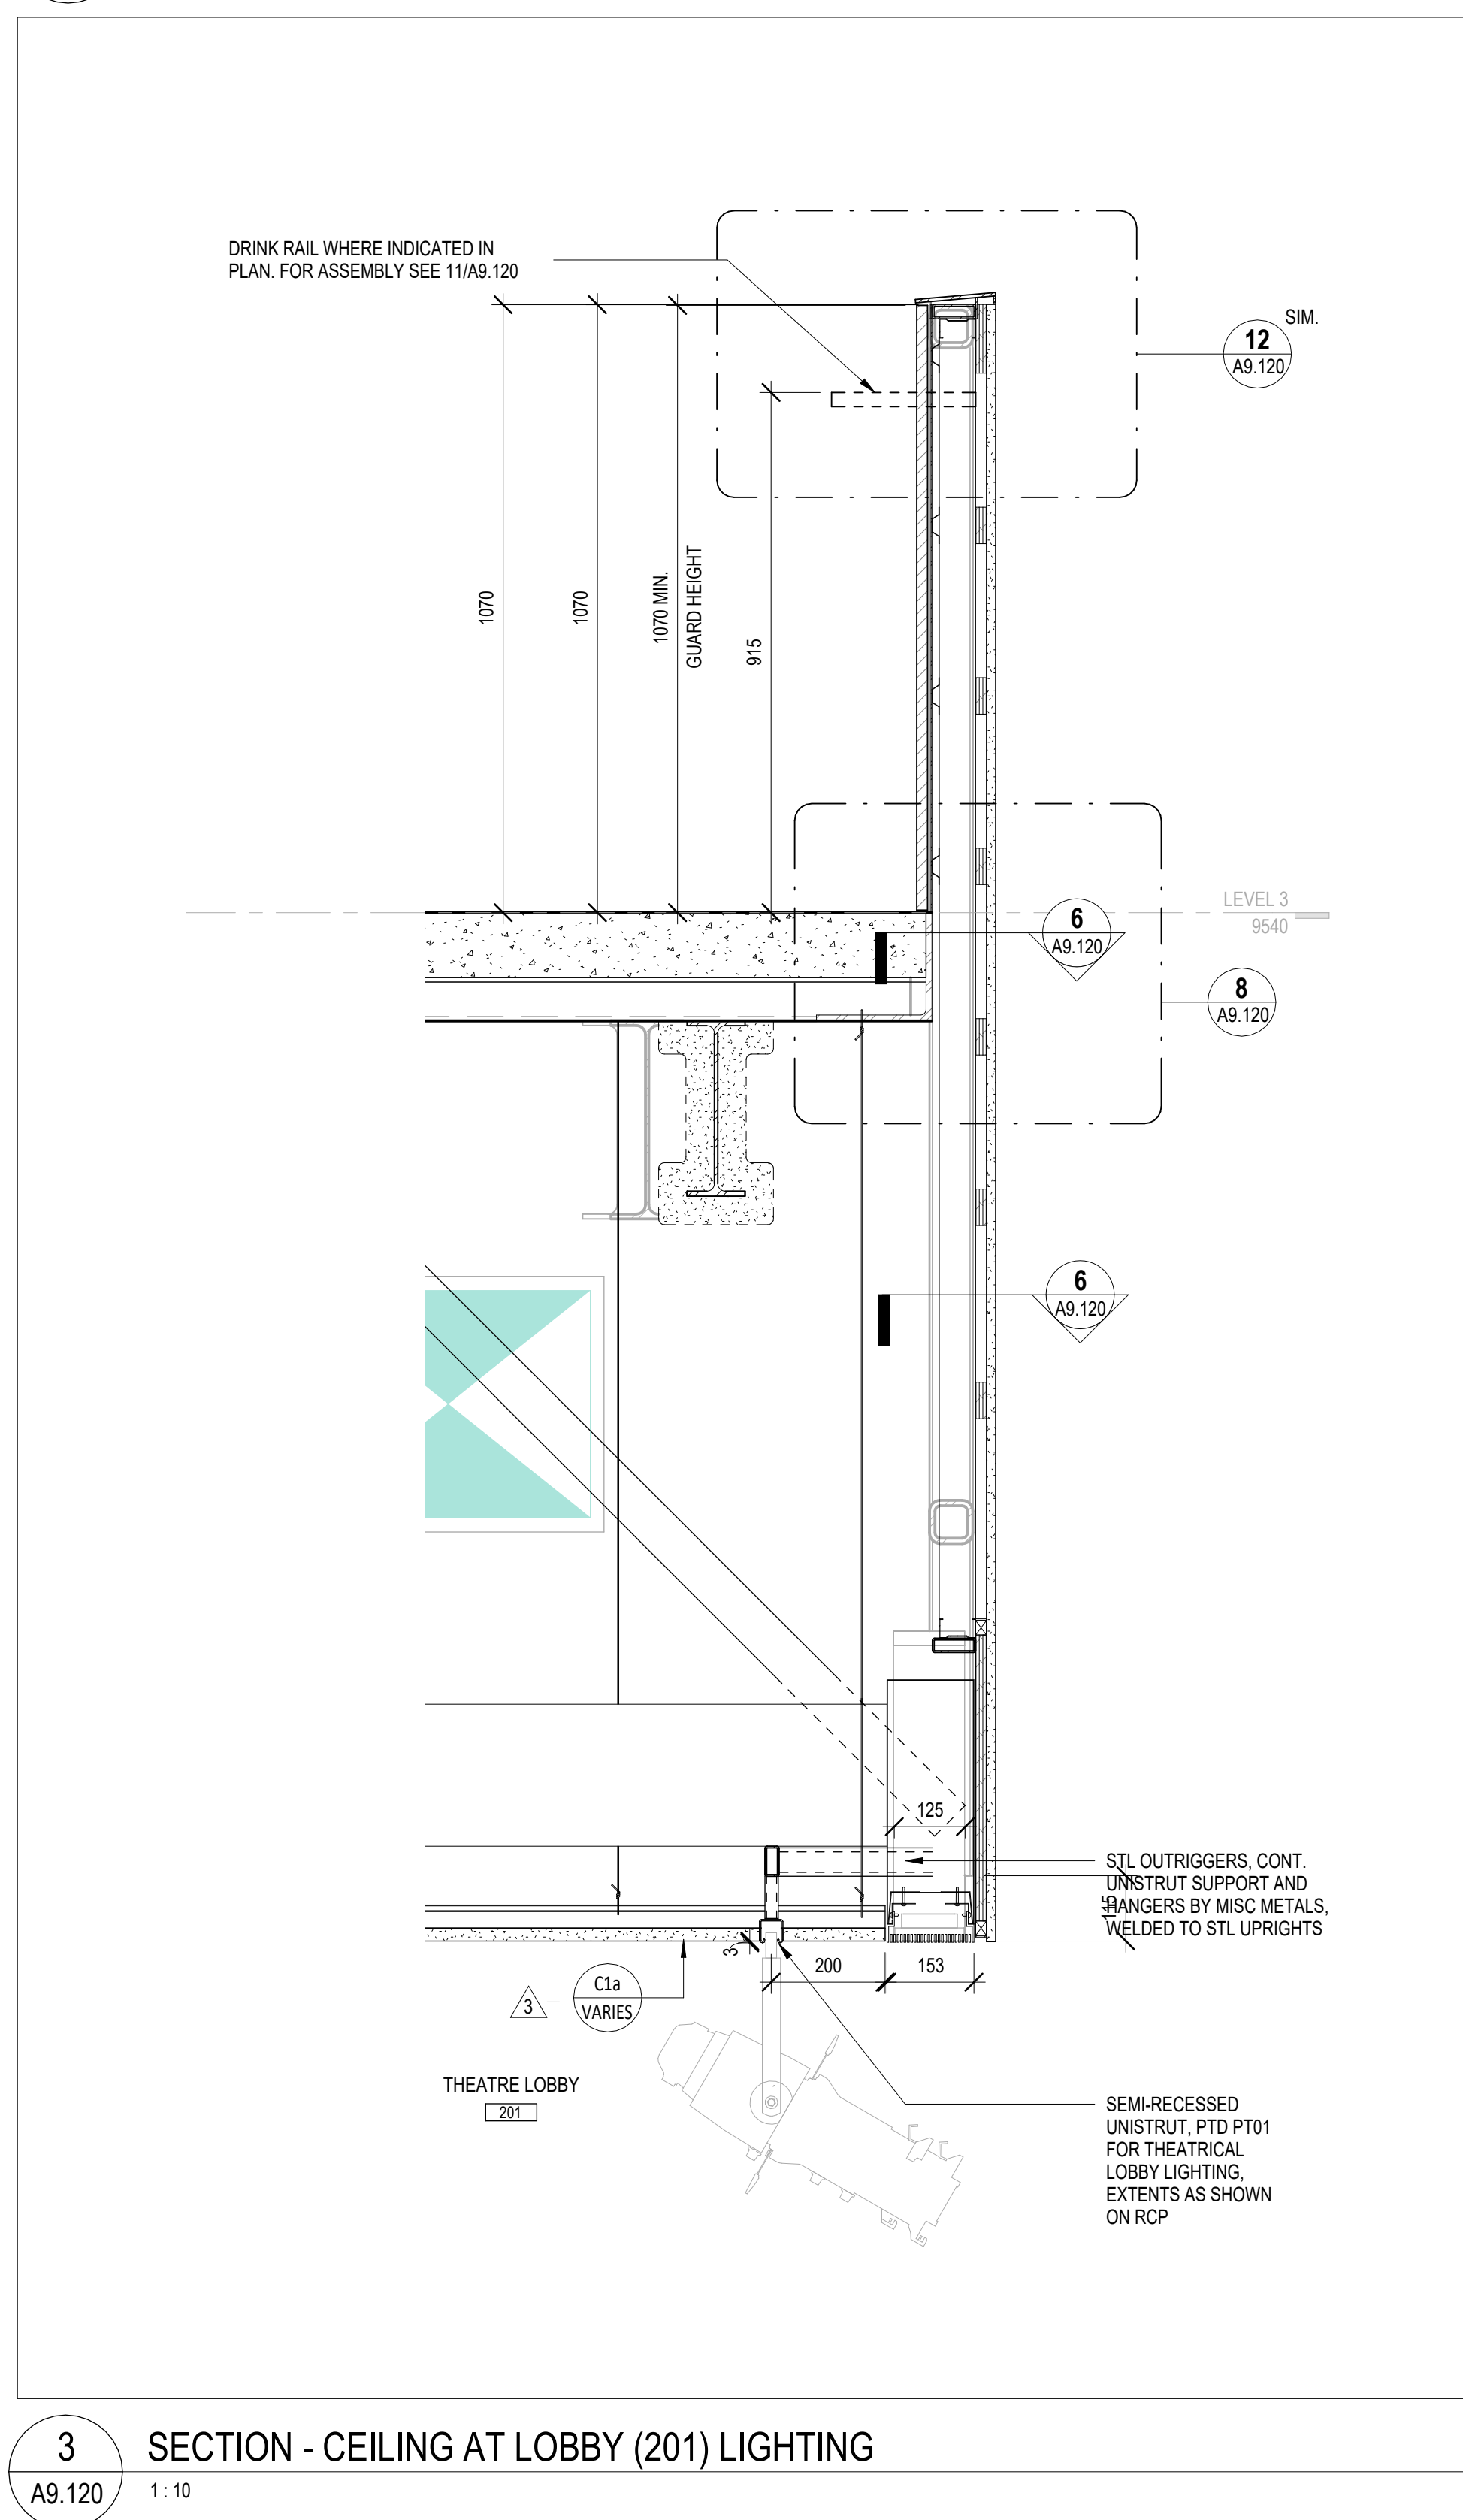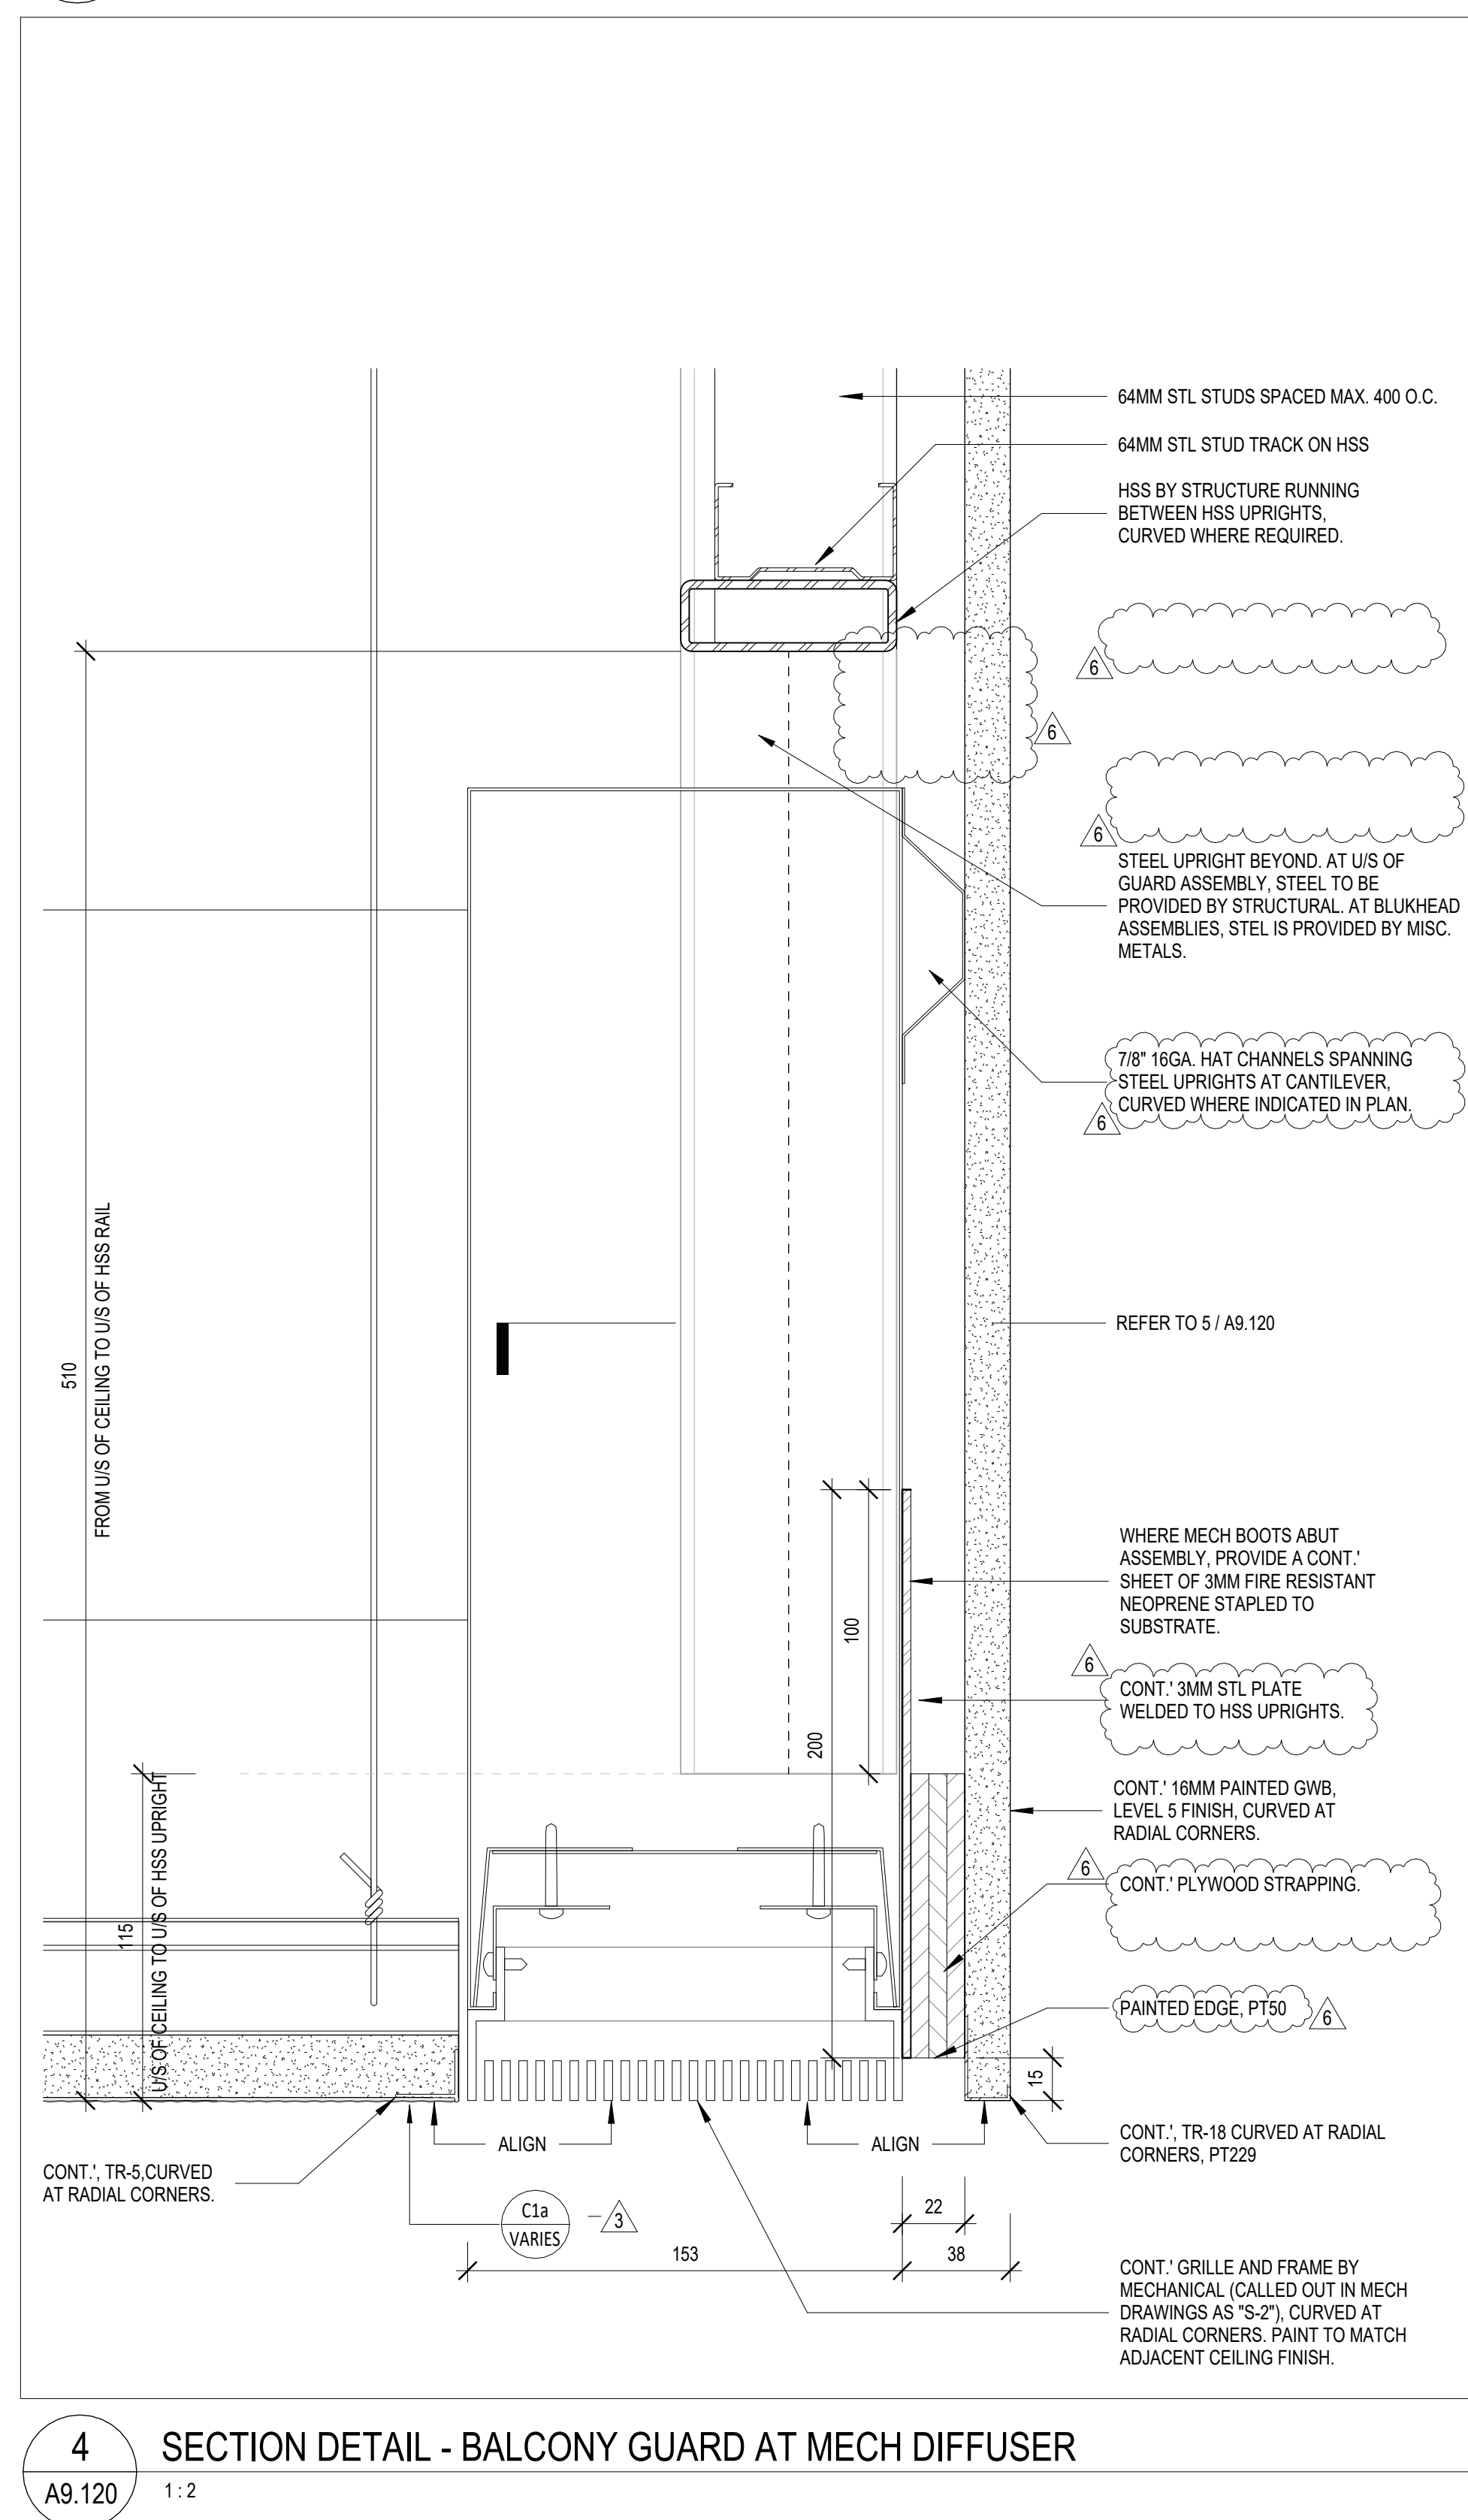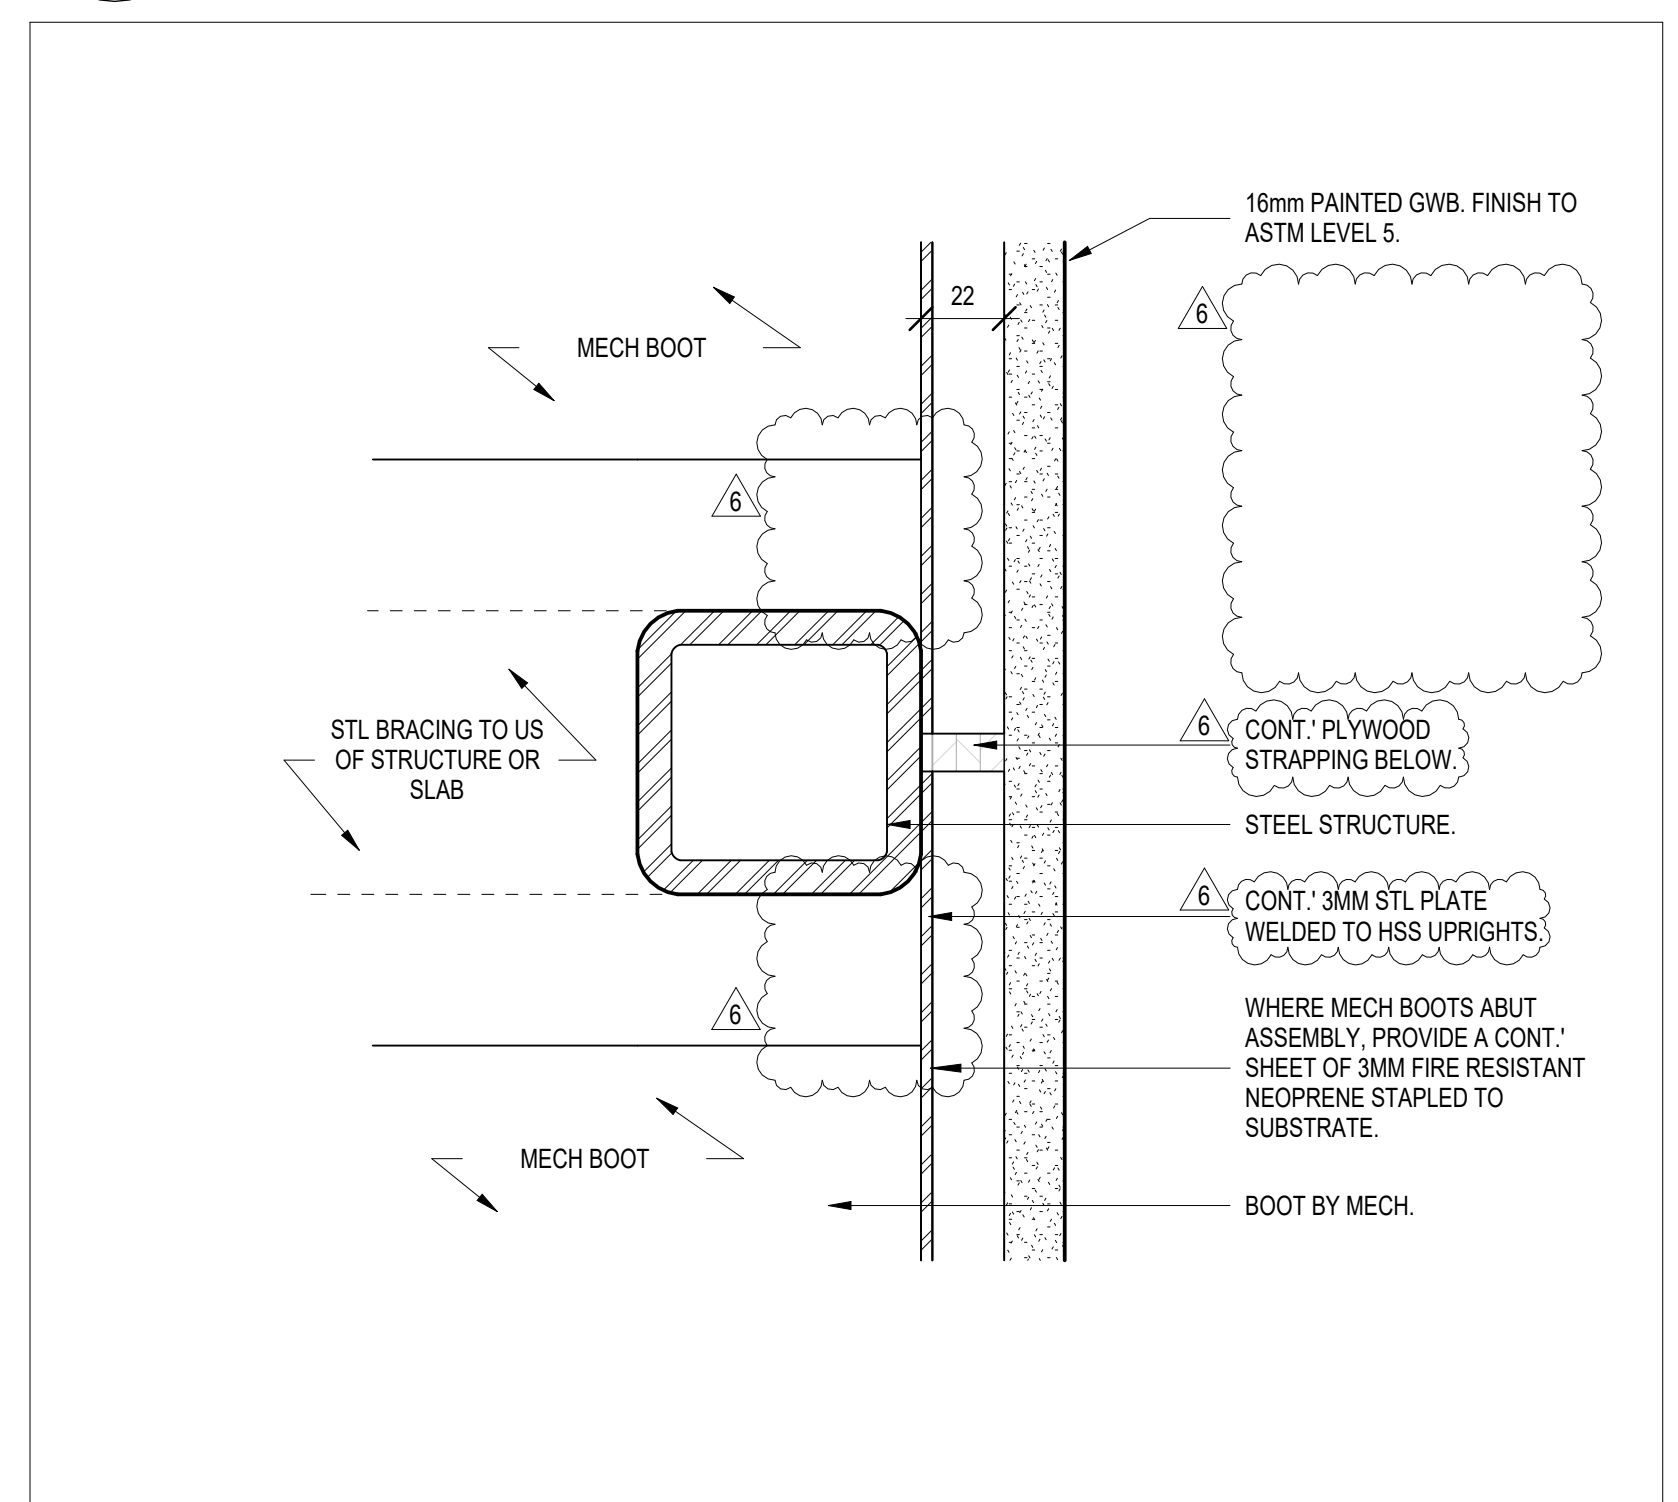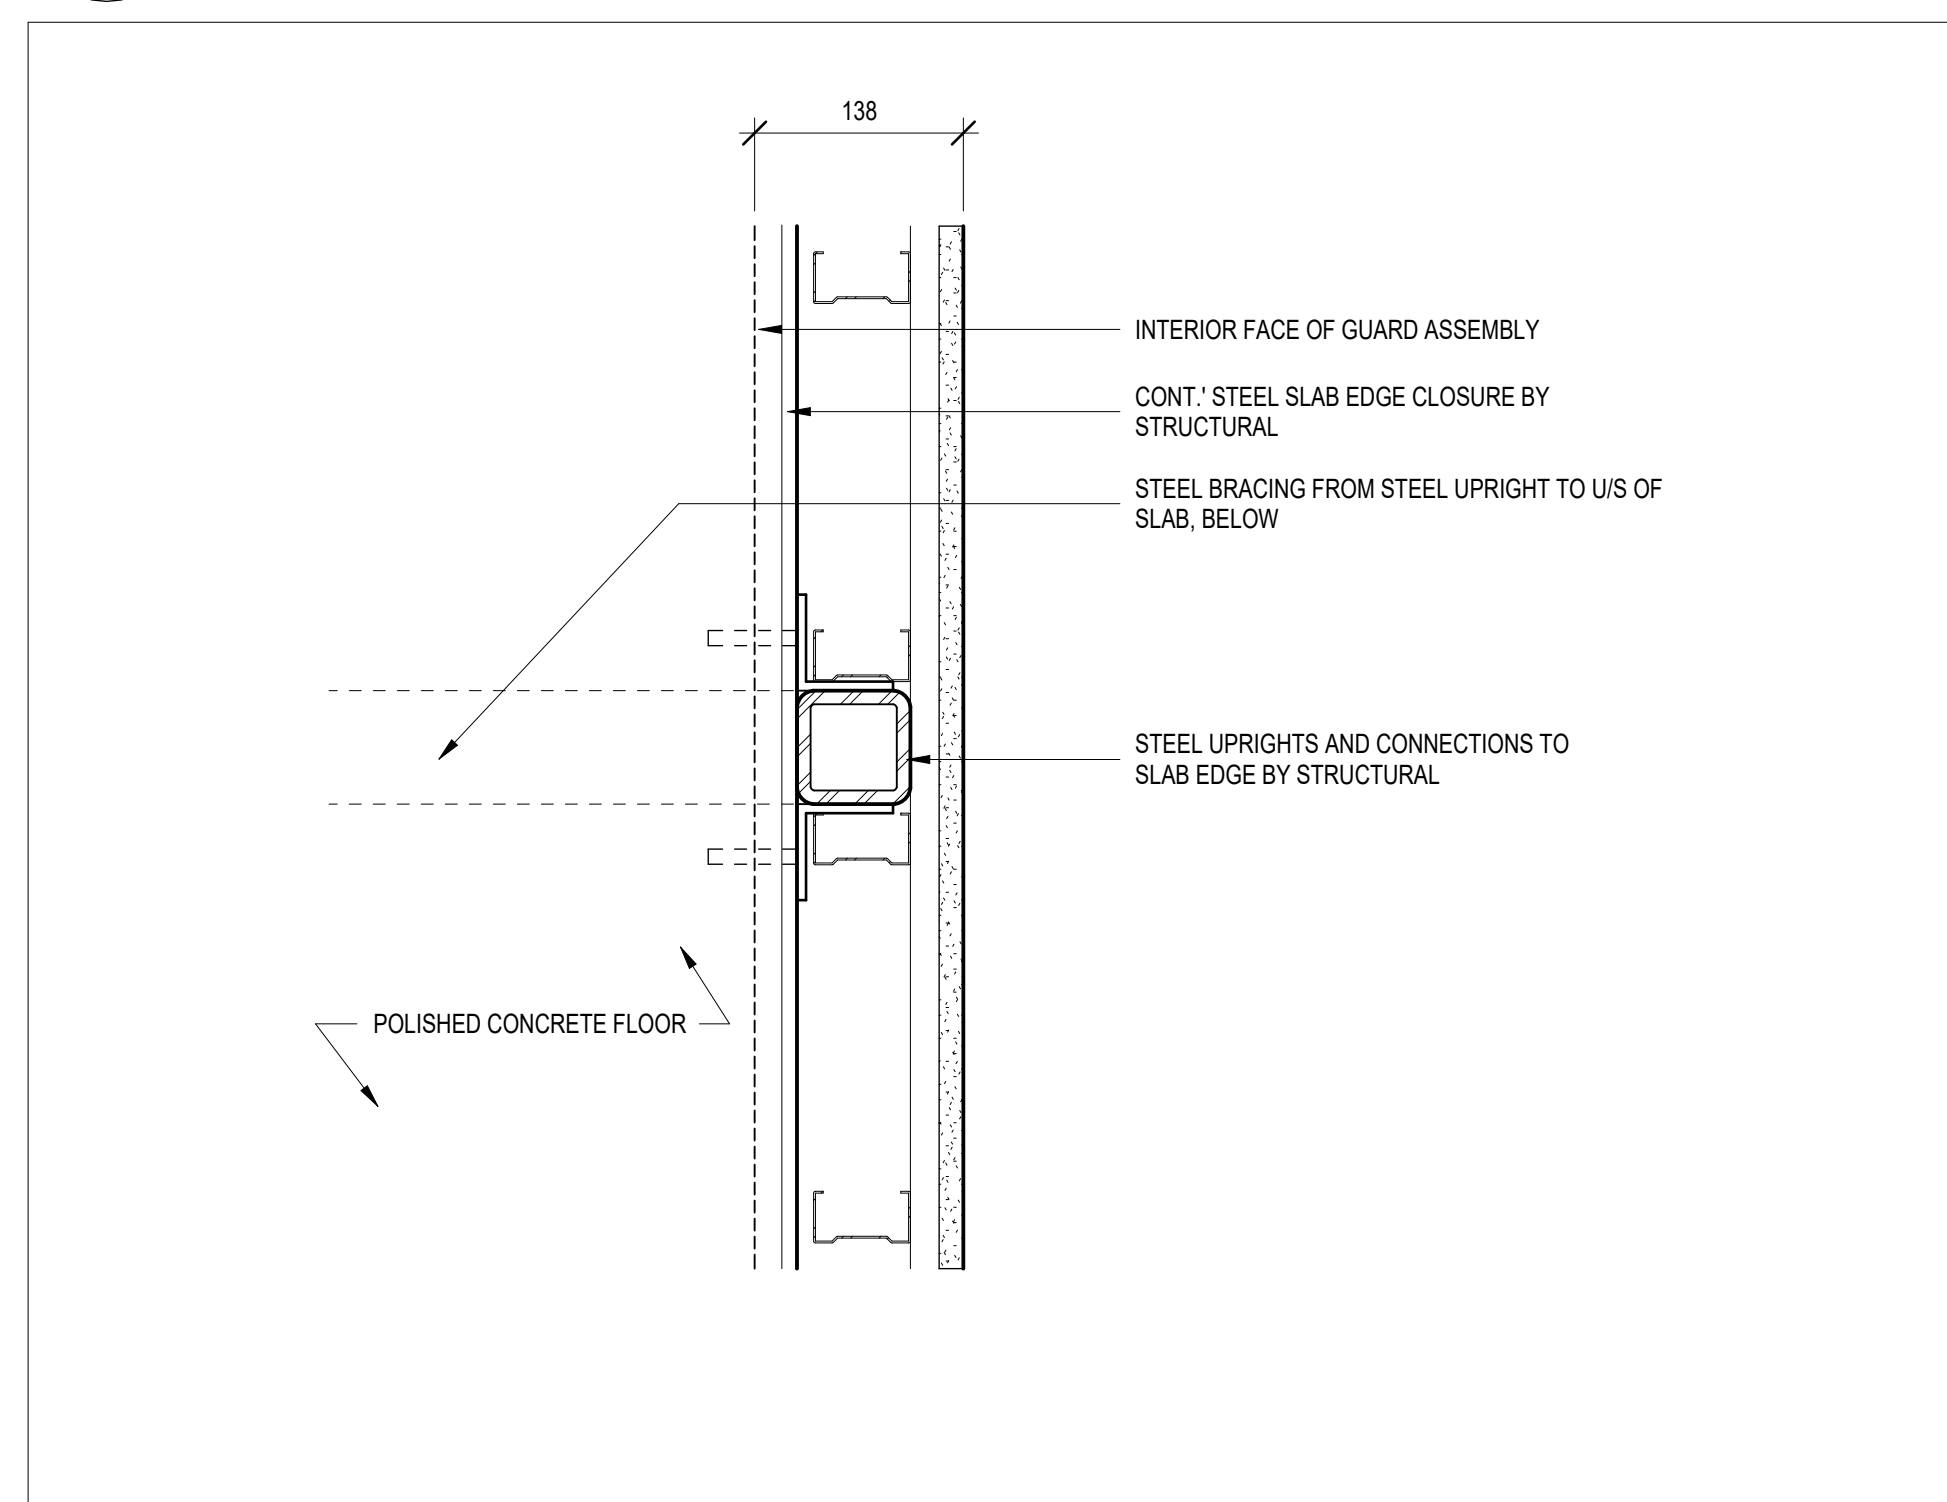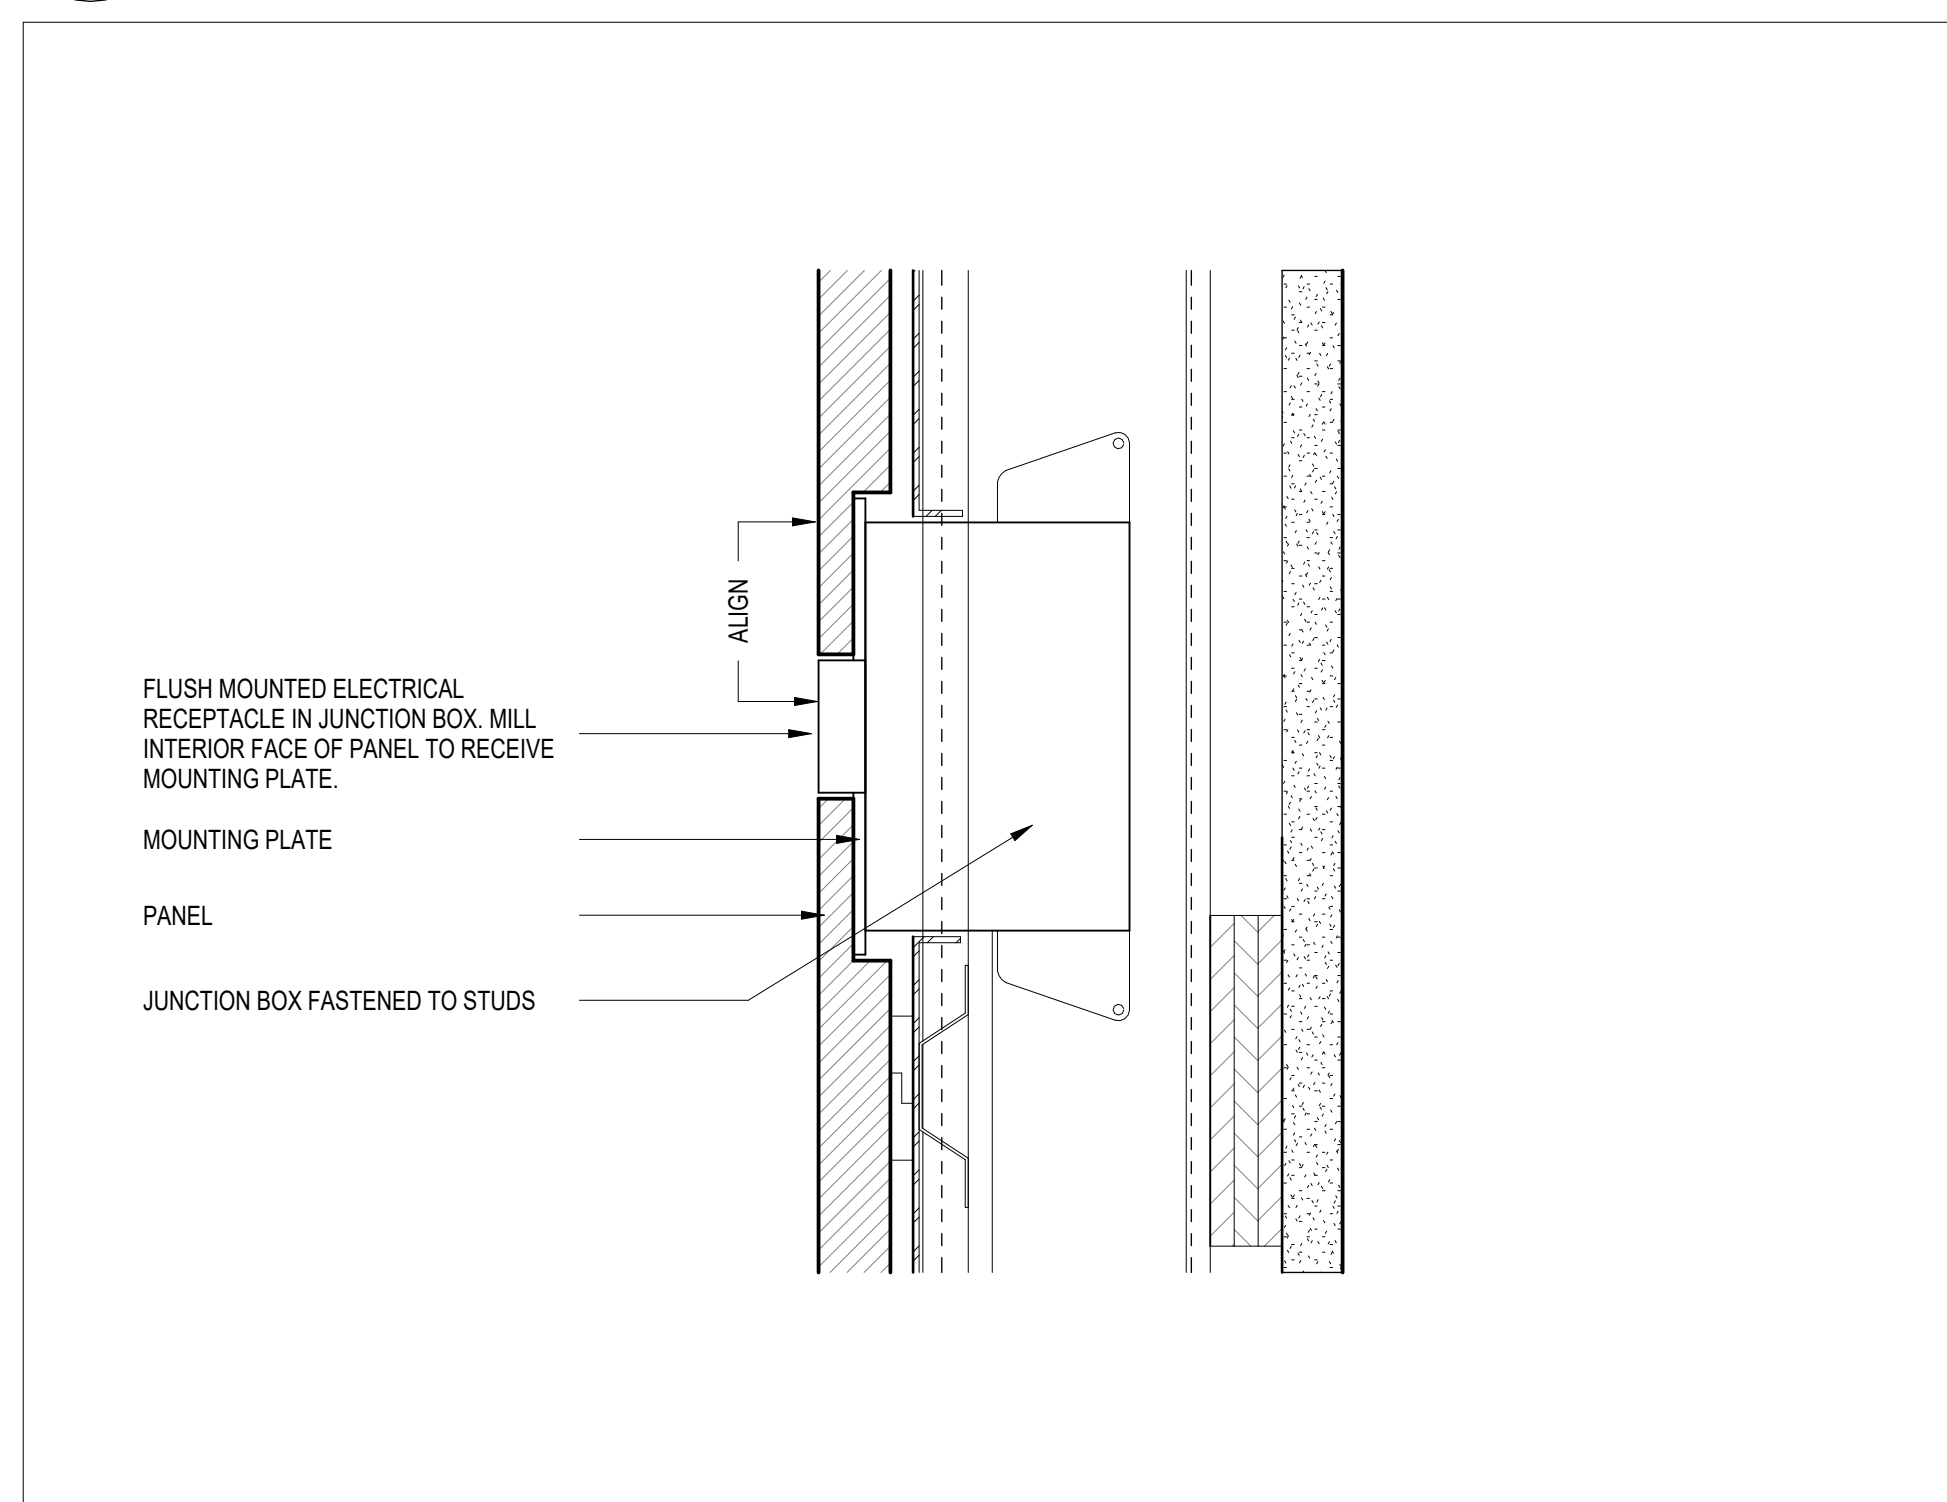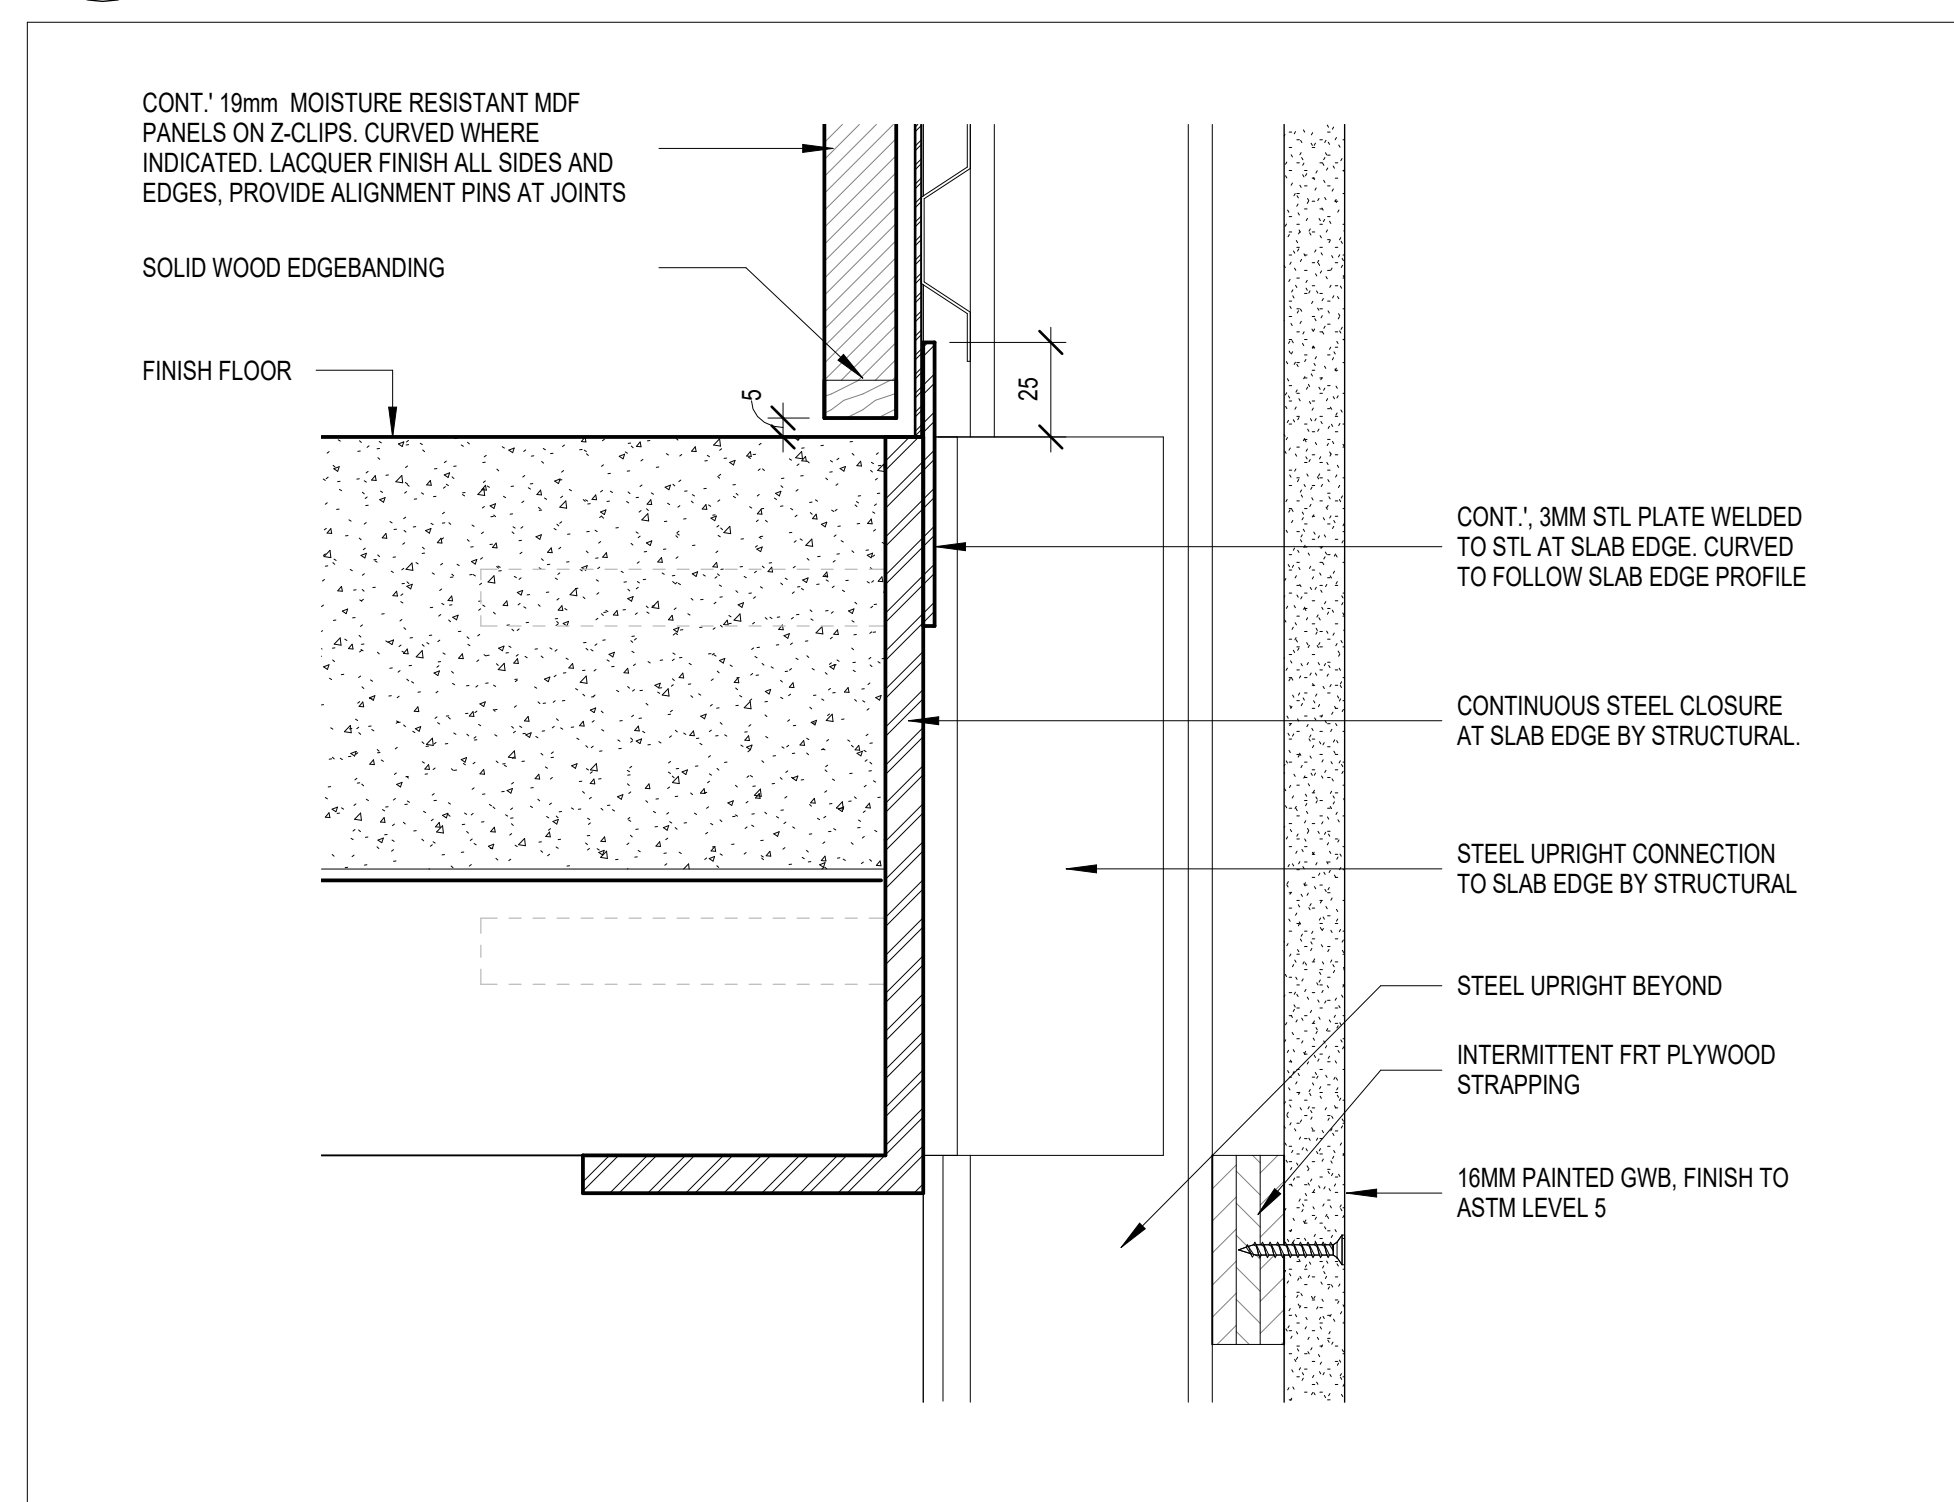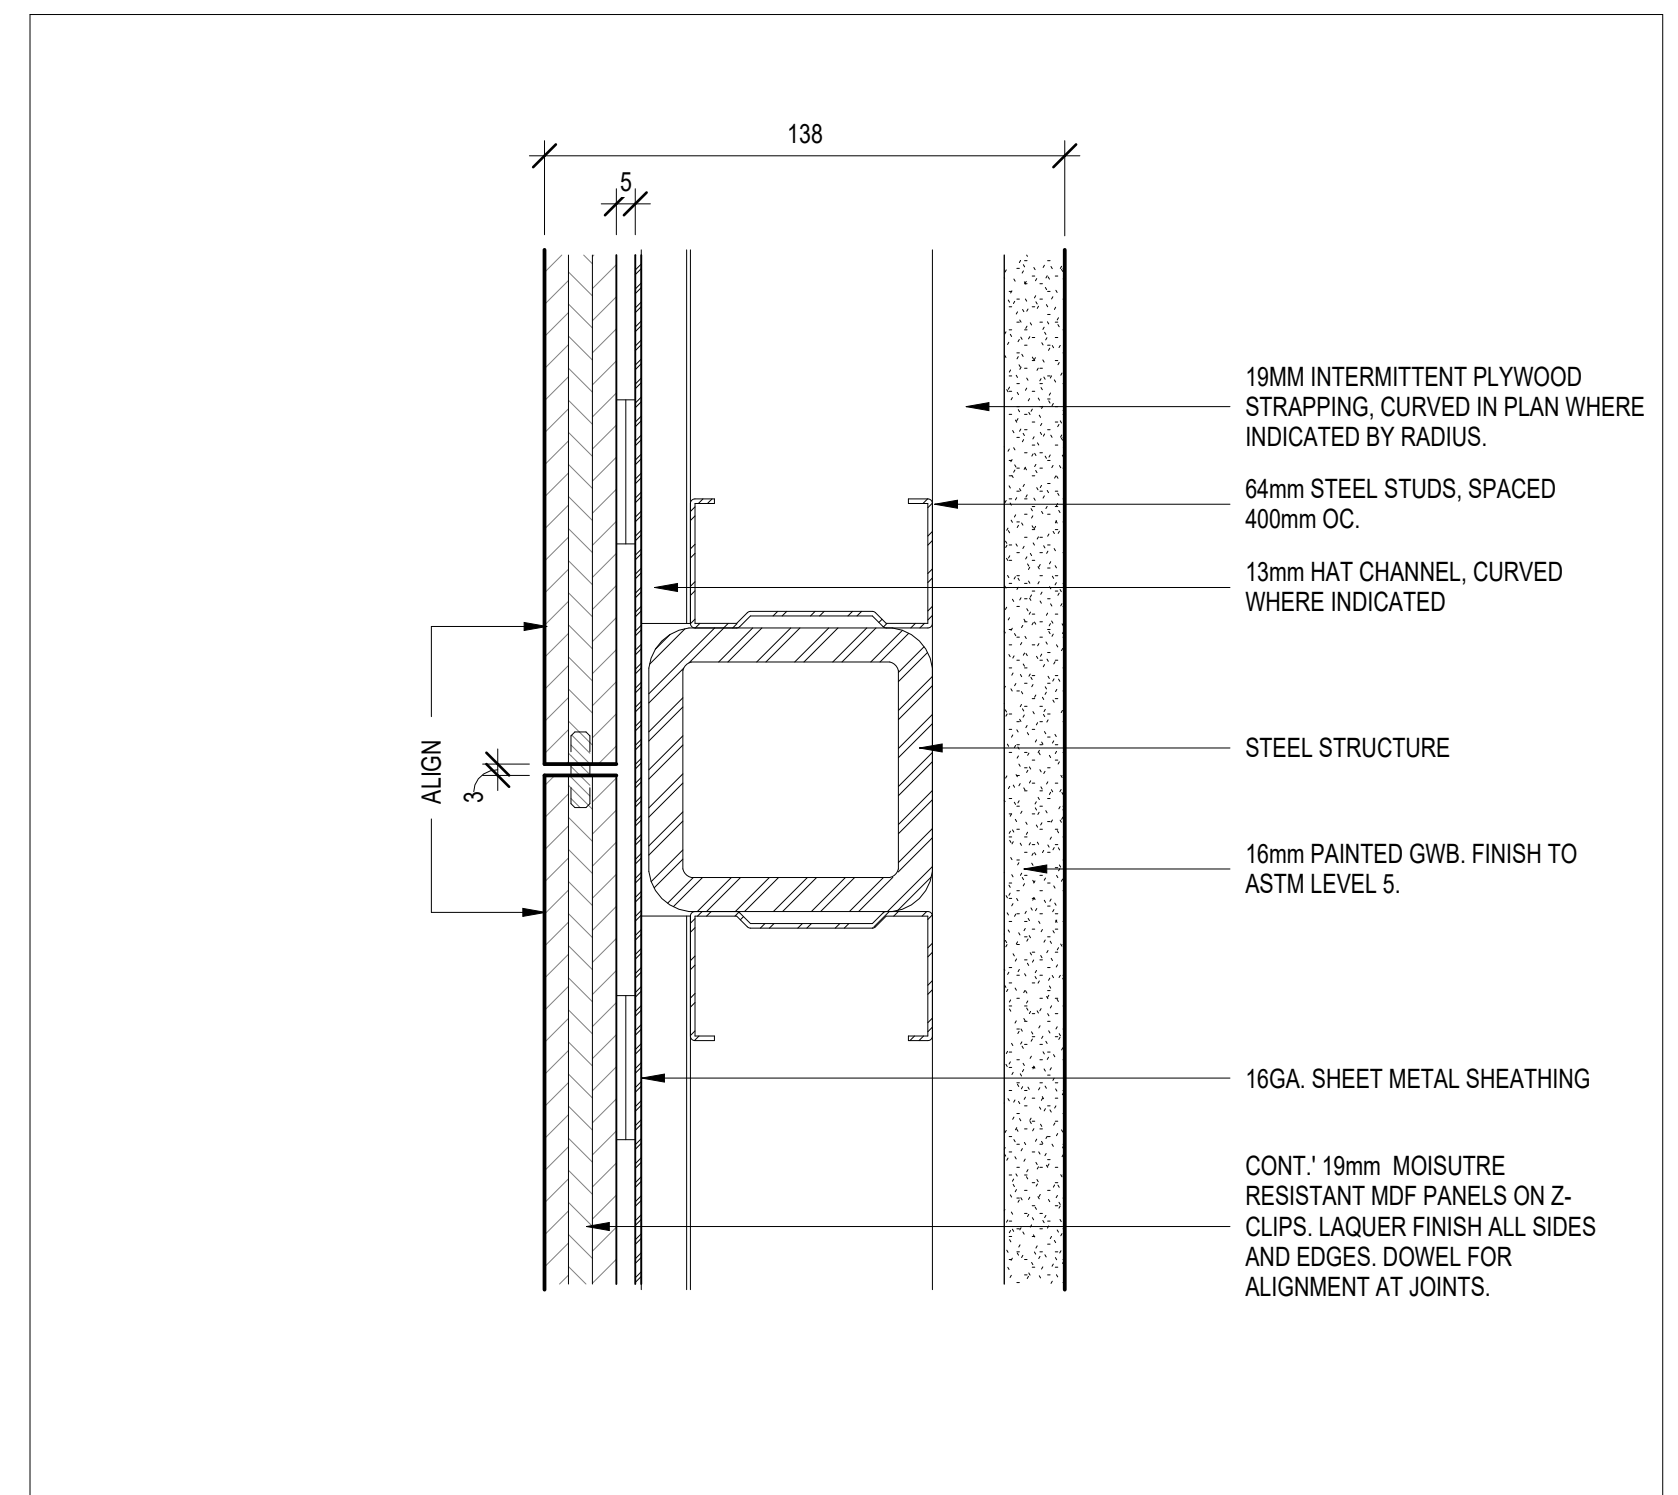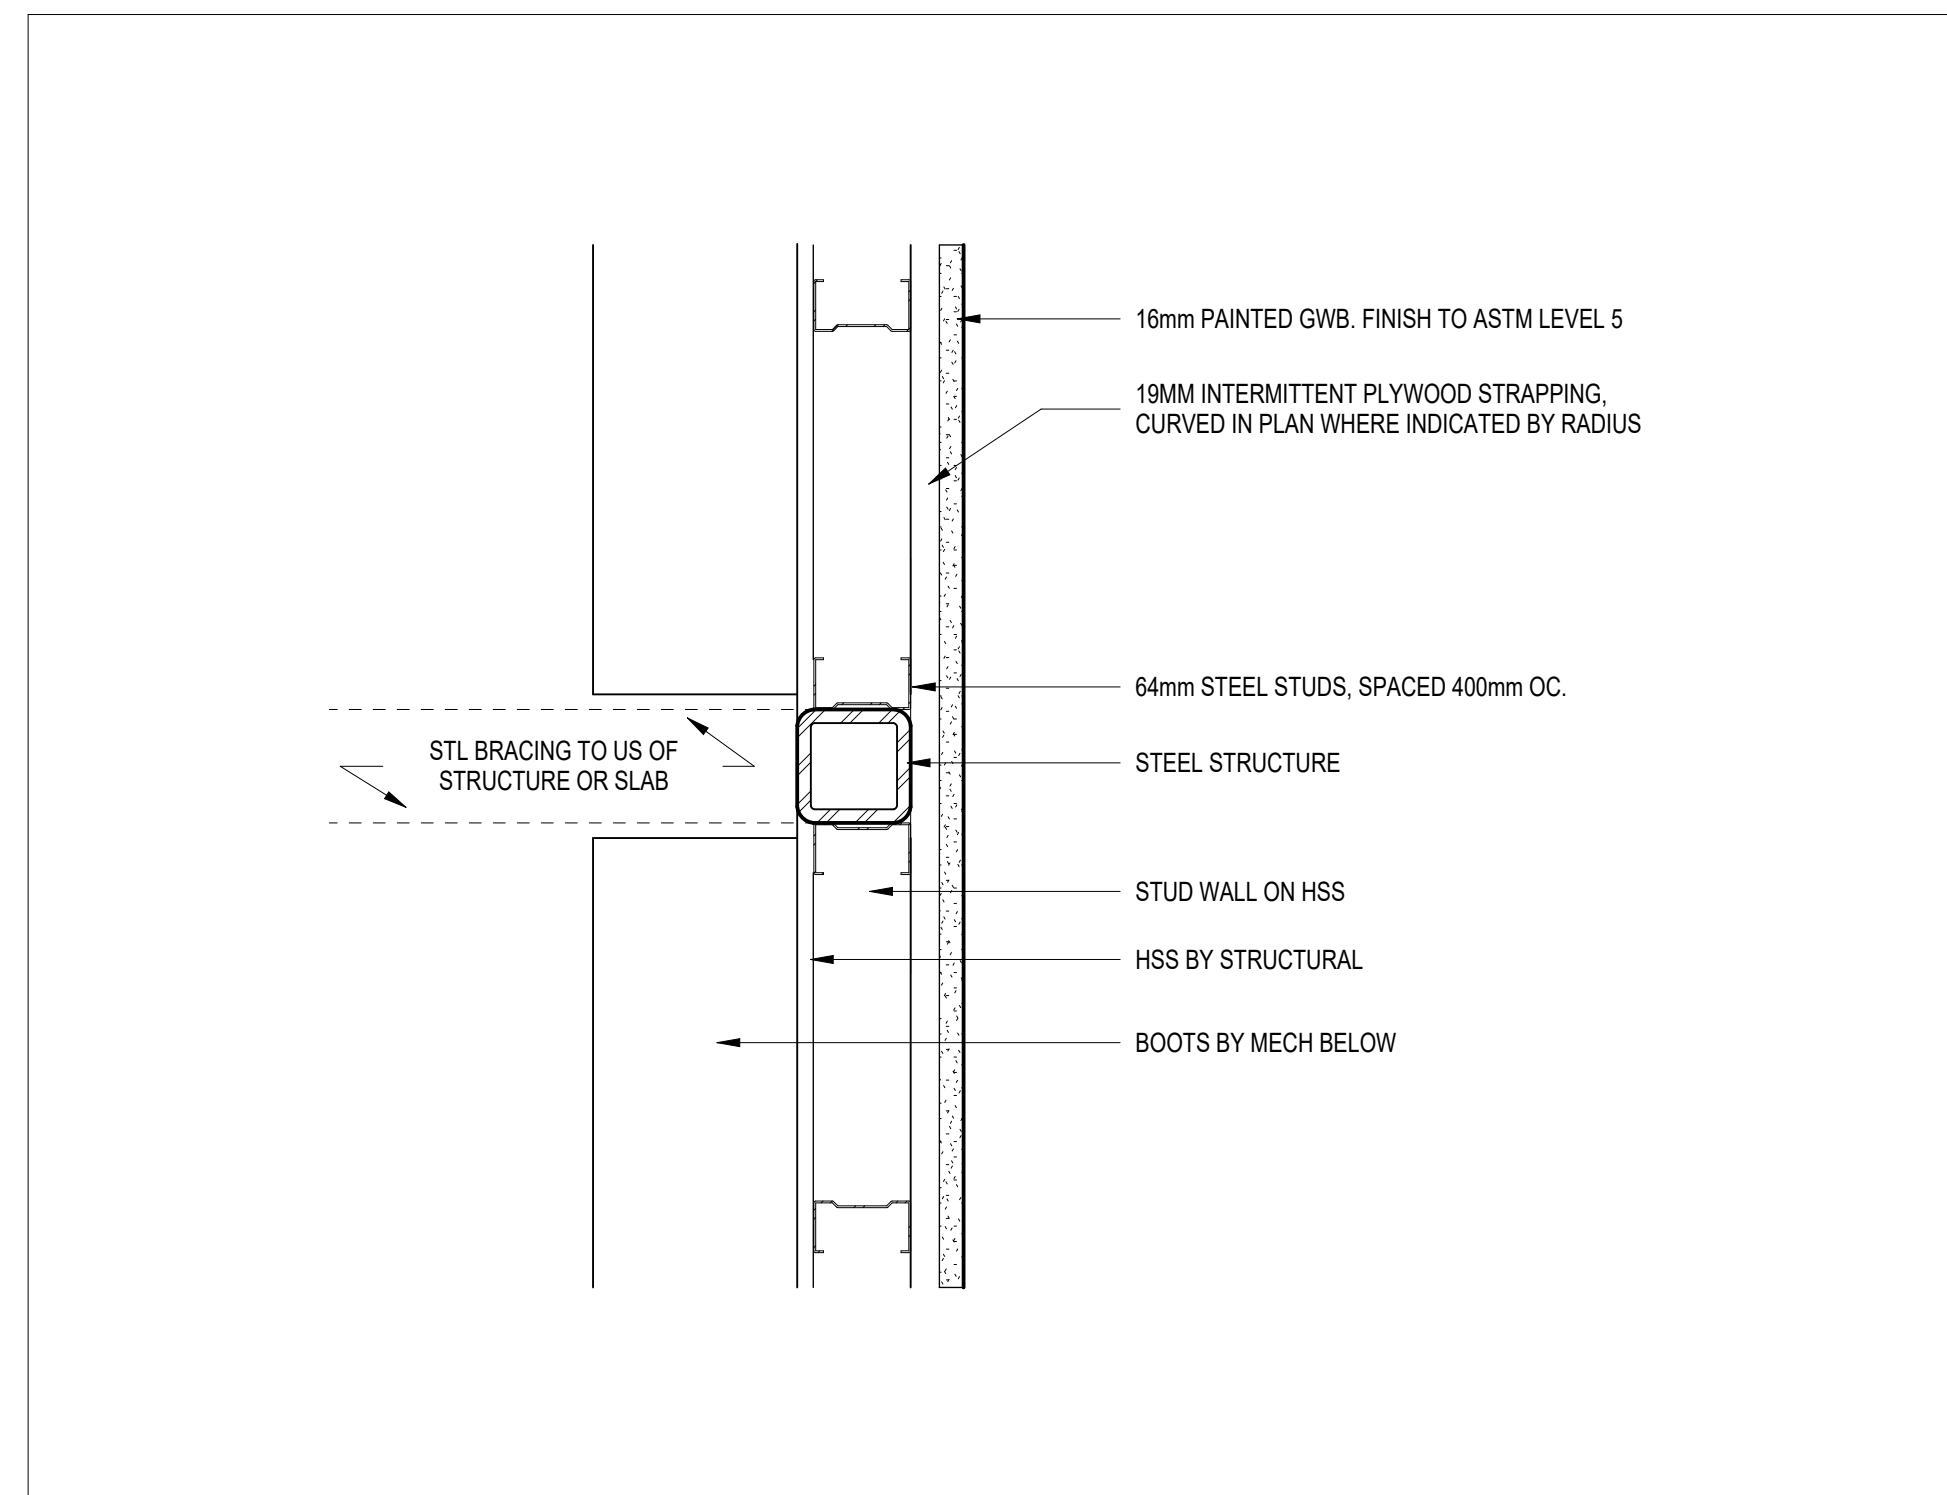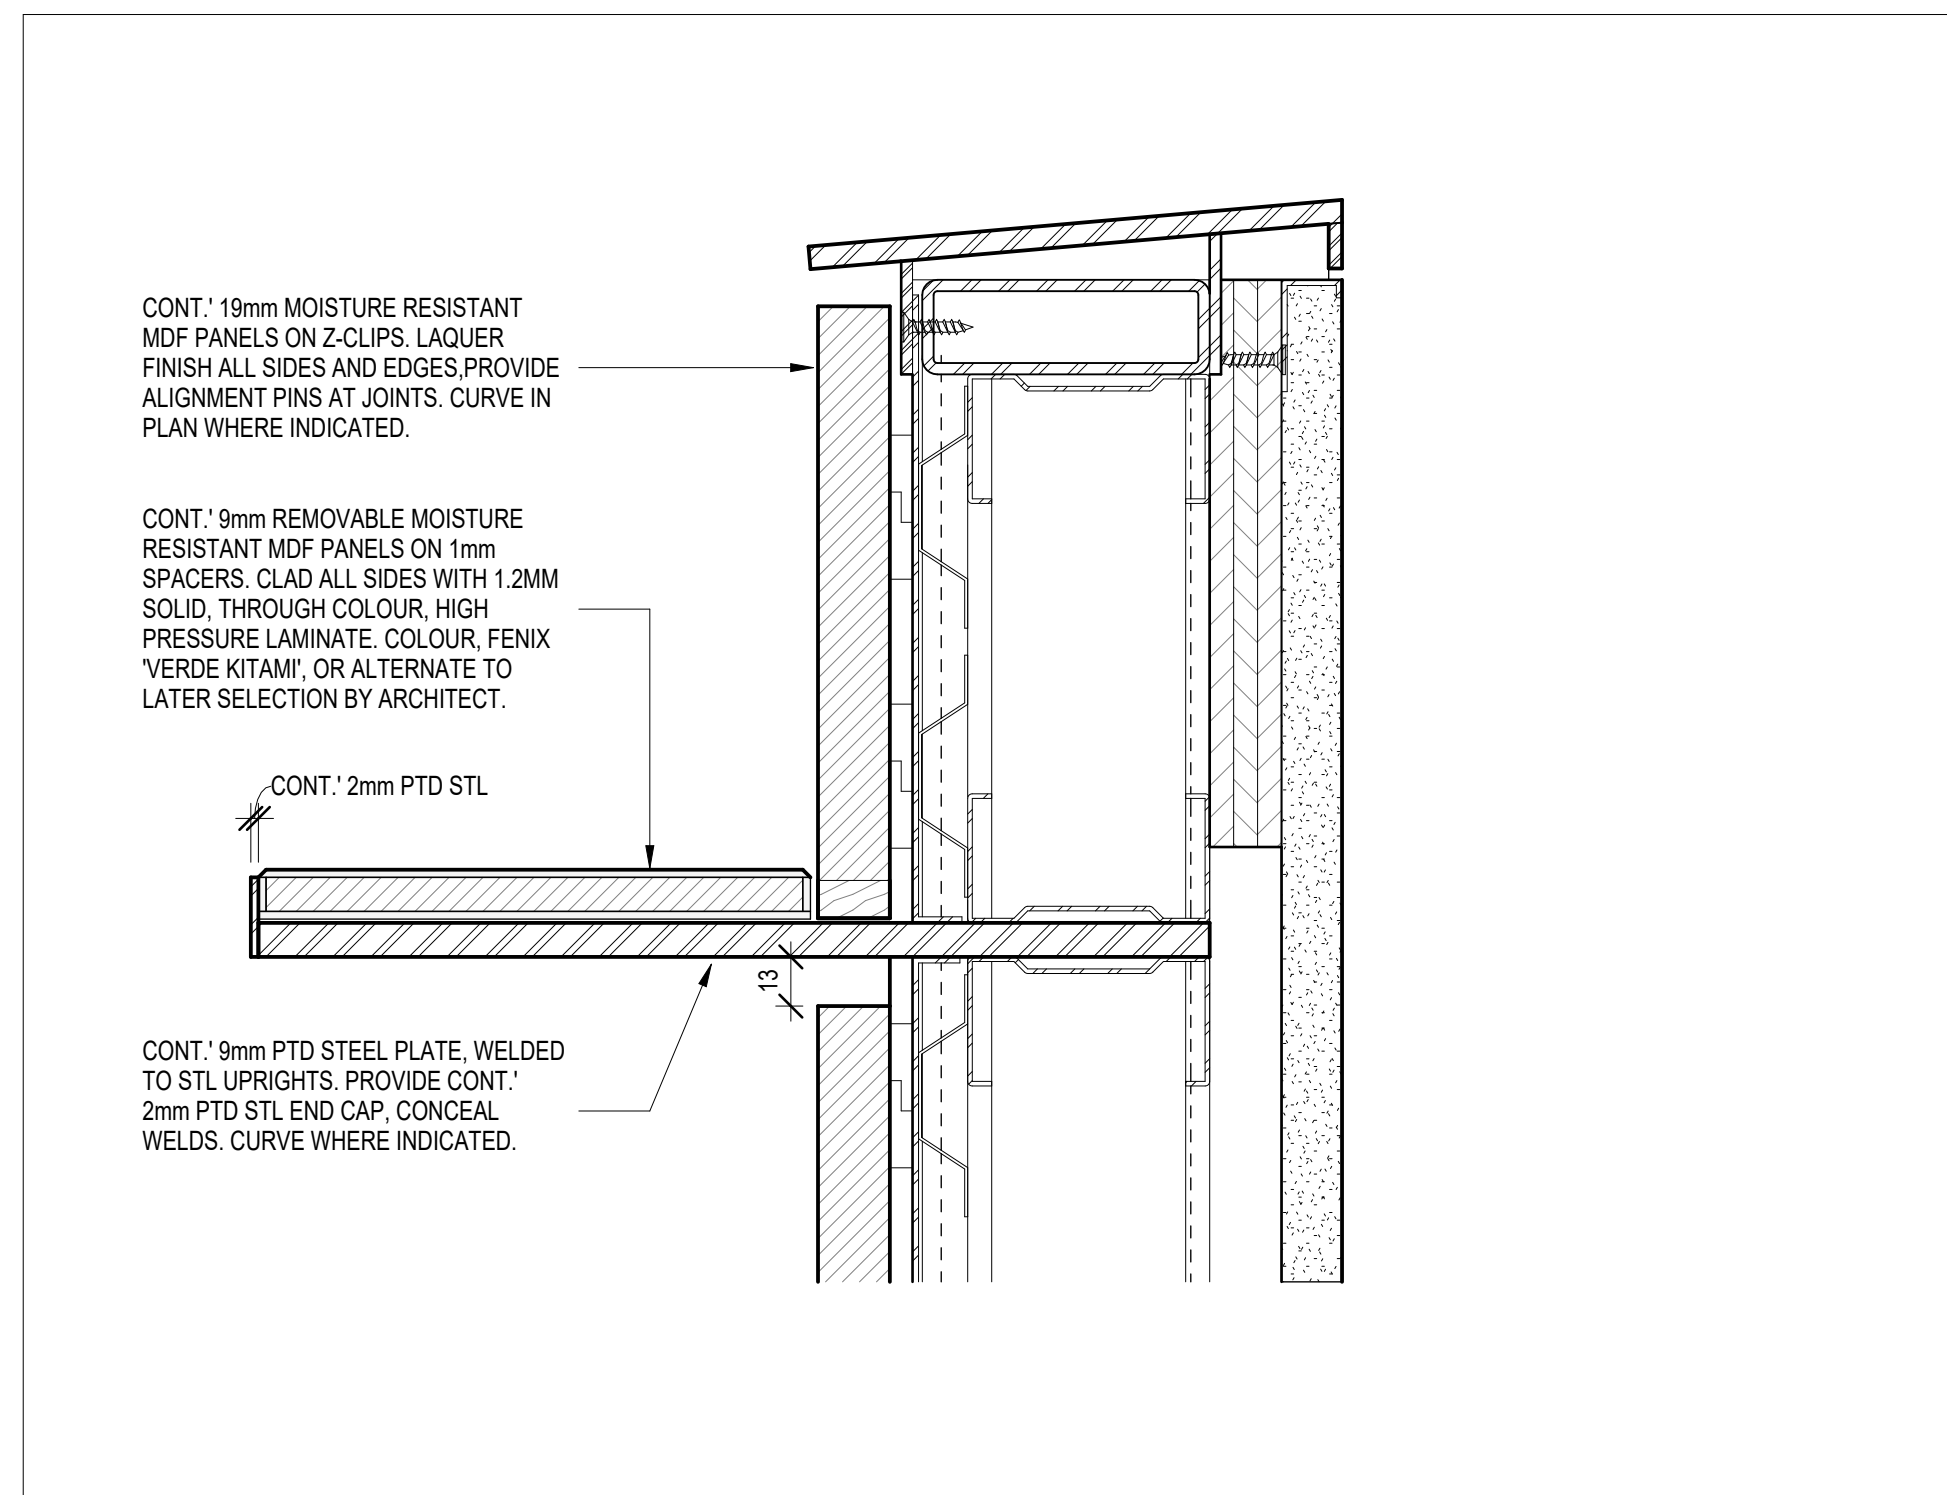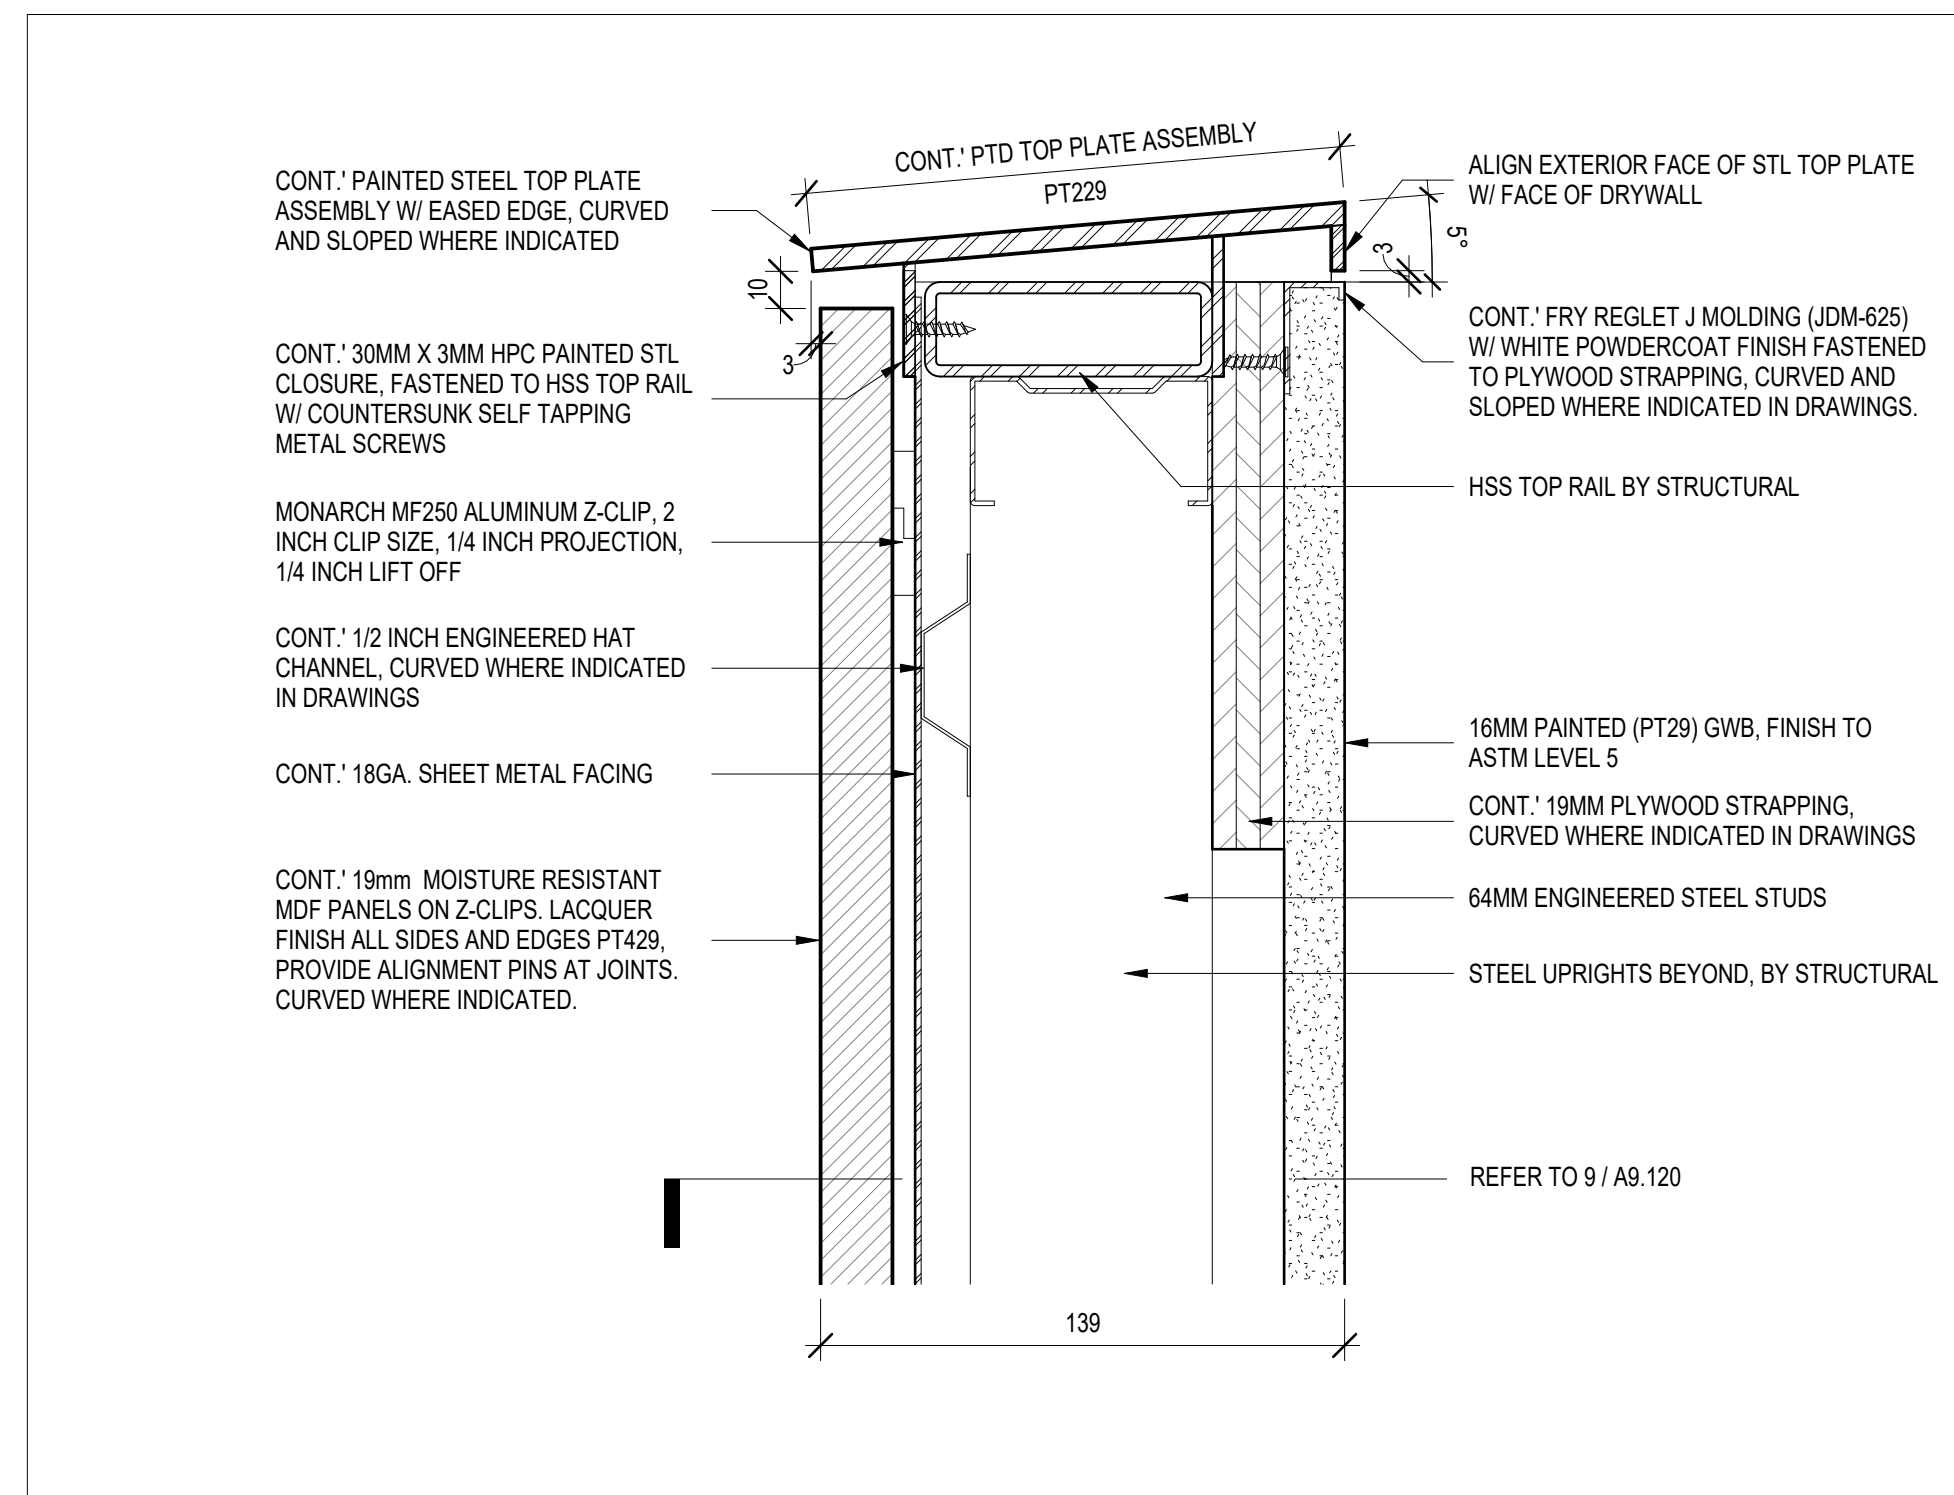

CONTRACT IS THAT OF THE ARCHITECT.
ANY VERSION OF THIS DRAWING REPRODUCED BY ANY
OTHER PARTY WITHOUT THE WRITTEN PERMISSION OR
APPROVAL OF THE ARCHITECT IS TO BE REJECTED.
THE ARCHITECT IS NOT LIABLE FOR ANY LOSS OR
DAMAGE TO PERSONS OR PROPERTY CAUSED BY THE
SUBSEQUENT REPRODUCTION OF THE ORIGINAL
DRAWING.

GENERAL NOTES:
DRAWINGS ARE NOT TO BE SCALED. CONTRACTOR WILL
VERIFY ALL EXISTING CONDITIONS AND DIMENSIONS
BEFORE TRYING TO REFORM THE WORK AND WILL REPORT ANY
DISCREPANCIES TO THE ARCHITECT IMMEDIATELY.
THE ARCHITECT SHALL BE CONSULTED FOR ALL
CHANGES BEFORE COMMENCING WORK.
THE ARCHITECT SHALL BE NOTIFIED IMMEDIATELY IN
CONJUNCTION WITH ALL OTHER CONTRACT DOCUMENTS
WHEN THE CONTRACTOR HAS ANY REQUESTS FOR
MECHANICAL AND ELECTRICAL DRAWINGS. IN CASES OF
DIFFERENCE BETWEEN THE CONSULTANTS' DOCUMENTS,
THE ARCHITECT'S DOCUMENTS SHALL PREVAIL.
THE WORK SHALL BE COMPLETED WITHIN THE
TIME. THE GREATER SHALL PREVAIL.

THE ARCHITECT'S RESPONSIBILITY FOR MECHANICAL OR
ELECTRICAL DEVICES, FITTINGS AND FIXTURES ARE
LIMITED TO THE DESIGN OF THE SYSTEMS. THE
ARCHITECT SHALL NOT BE RESPONSIBLE FOR THE
INSTALLATION OR THE PERFORMANCE OF THE SYSTEMS
SHOWN ON THE ARCHITECTURAL DRAWINGS. SHALL CARRY
THE RESPONSIBILITY FOR THE DESIGN OF THE
MECHANICAL AND ELECTRICAL ITEMS NOT SHOWN
HEREON. THE ARCHITECT IS NOT TO BE HELD
RESPONSIBLE FOR THE DESIGN OF THE MECHANICAL
AND ELECTRICAL ITEMS NOT SHOWN HEREON.

THESE DOCUMENTS ARE NOT TO BE USED FOR
ANY OTHER PURPOSES UNLESS SPECIFICALLY NOTED FOR SUCH
PURPOSE.

6	2025-11-31	ISSUED FOR S-620
5	2025-09-30	ISSUED FOR CONSOLIDATION
4	2025-08-08	ISSUED FOR BUILDING PERMIT R#1
3	2025-06-09	ISSUED FOR ADDENDUM 02
2	2025-04-01	ISSUED FOR TENDER PACKAGE 2
1	2025-12-09	ISSUED FOR BUILDING PERMIT

SEAL



ARCHITECT

KPMB

KPMB Architects
351 King Street East, Suite 1200
Toronto, Canada M5A 0L6
+1 416 977 5104
kpmb@kpmbarchitects.com

HINDLE ARCHITECTS

Hindle Architects
Suite 510, Burns Building
237 8th Avenue SE
Calgary, AB
T2G 5C3

TAVV

Tawaw Architecture Collective
#203, 1218 9 Ave SE
Calgary, AB T2G 0T1
(525) 431 0294

CMLC


Arts Commons Transformation Phase 1 Expansion

205 8th Avenue S.E. Calgary, Alberta

Project No.	2041
Scale	As indicated
Plot Date	10/09/24


FOH - L2 & L3 GUARD DETAILS

A9.120

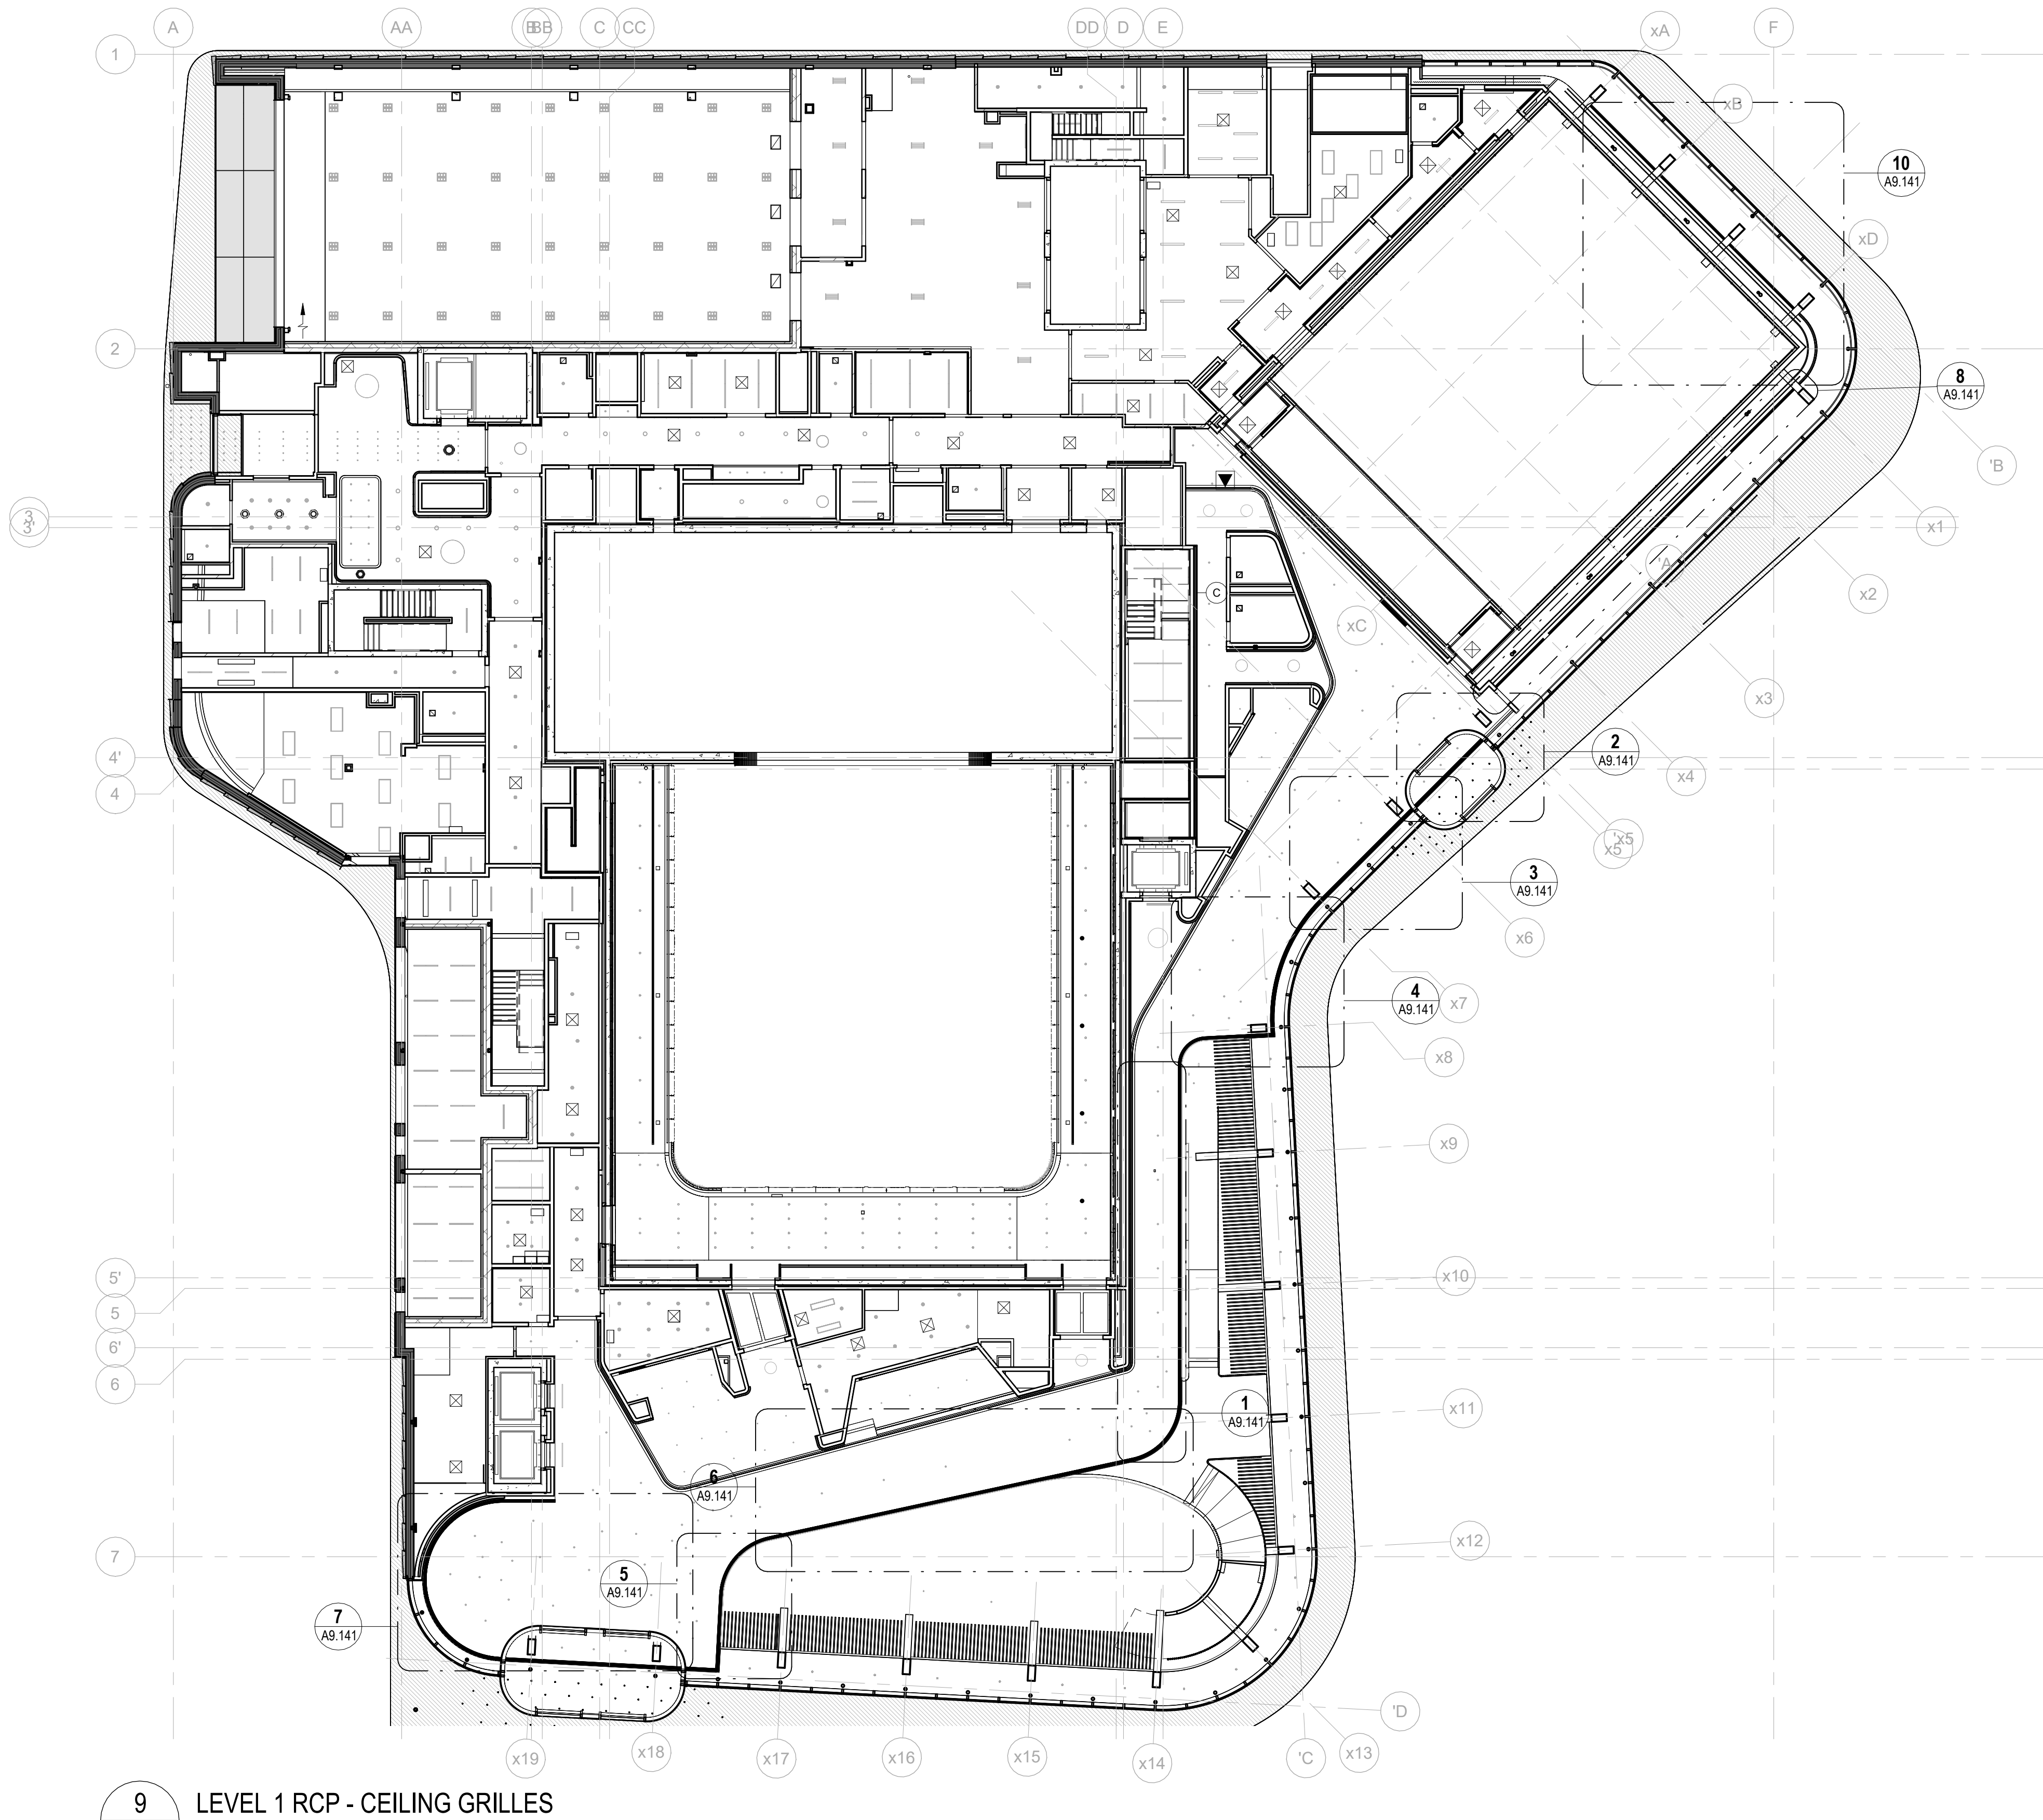


10 LEVEL 1 RCP - CEILING GRILLES - 9

A9.141 1:50

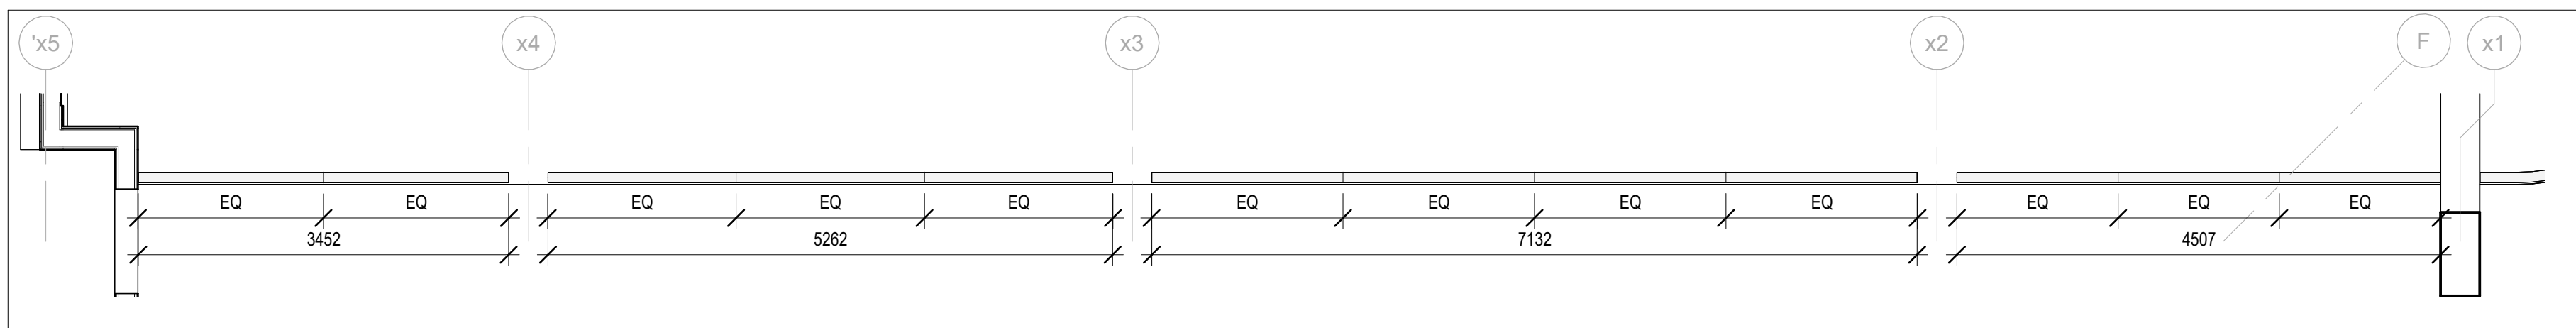


8 LEVEL 1 RCP - CEILING GRILLES - 8

A9.141 1:50

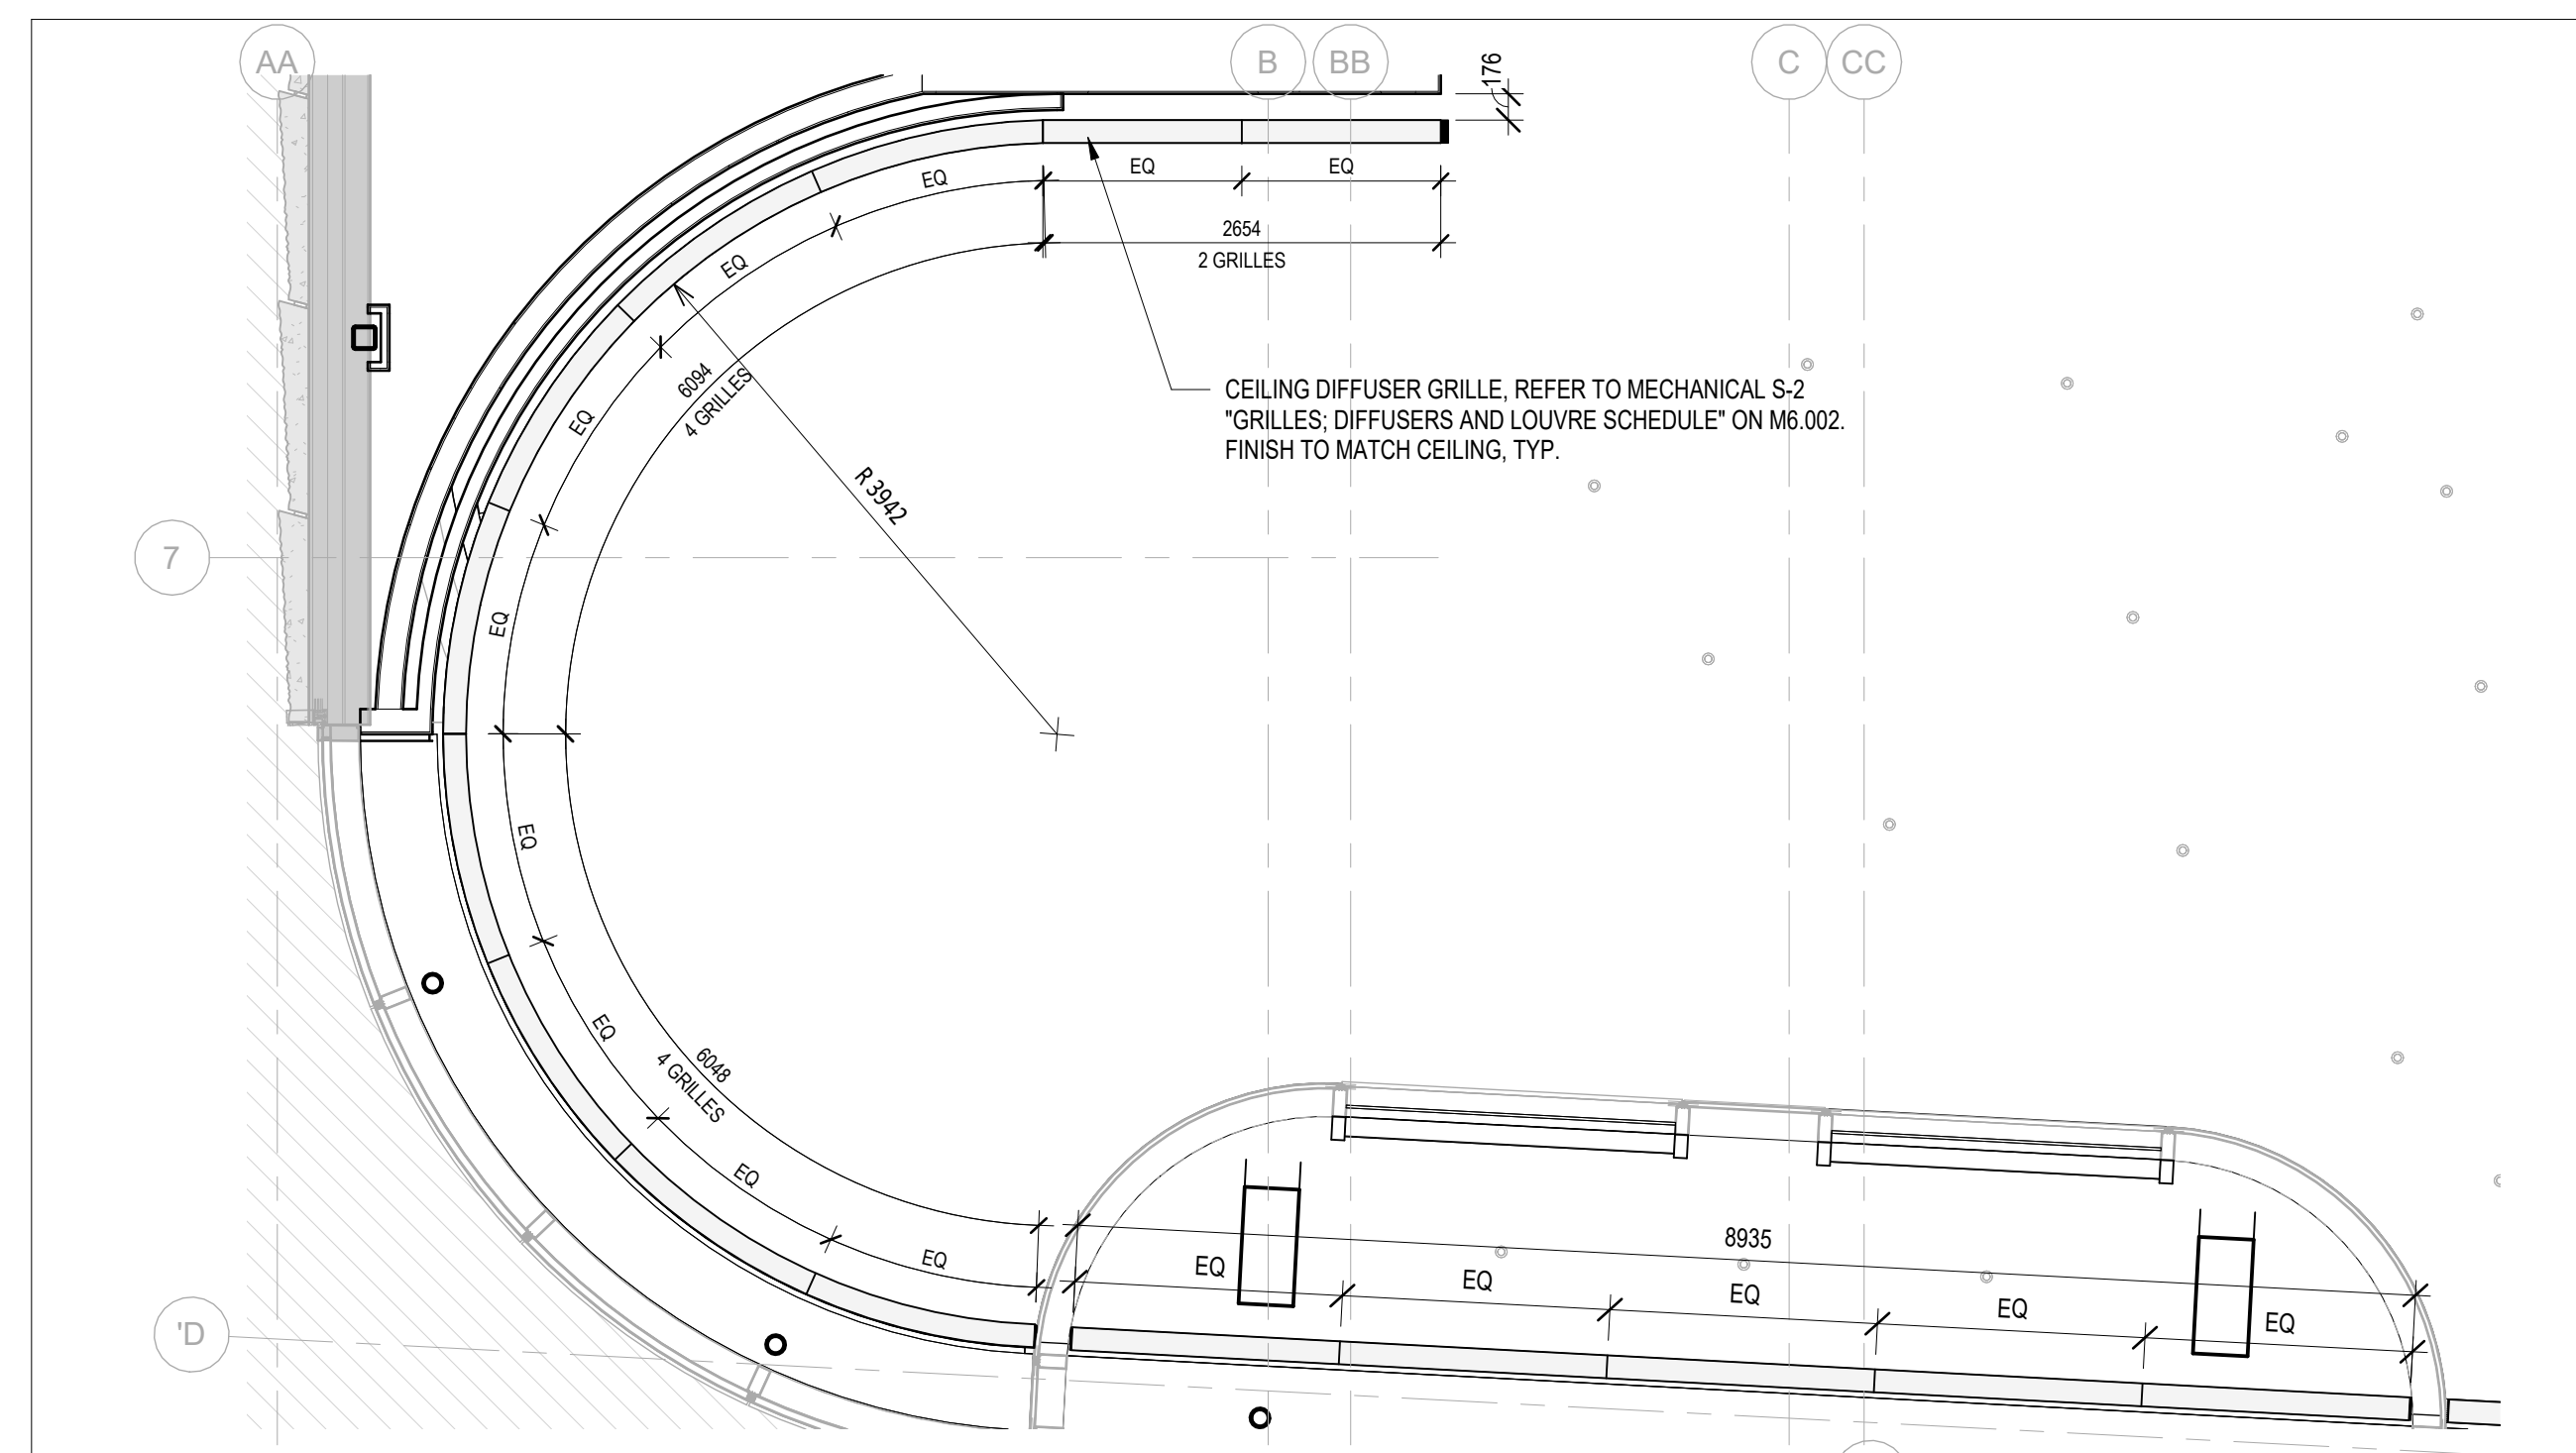


7 LEVEL 1 RCP - CEILING GRILLES - 7

A9.141 1:50

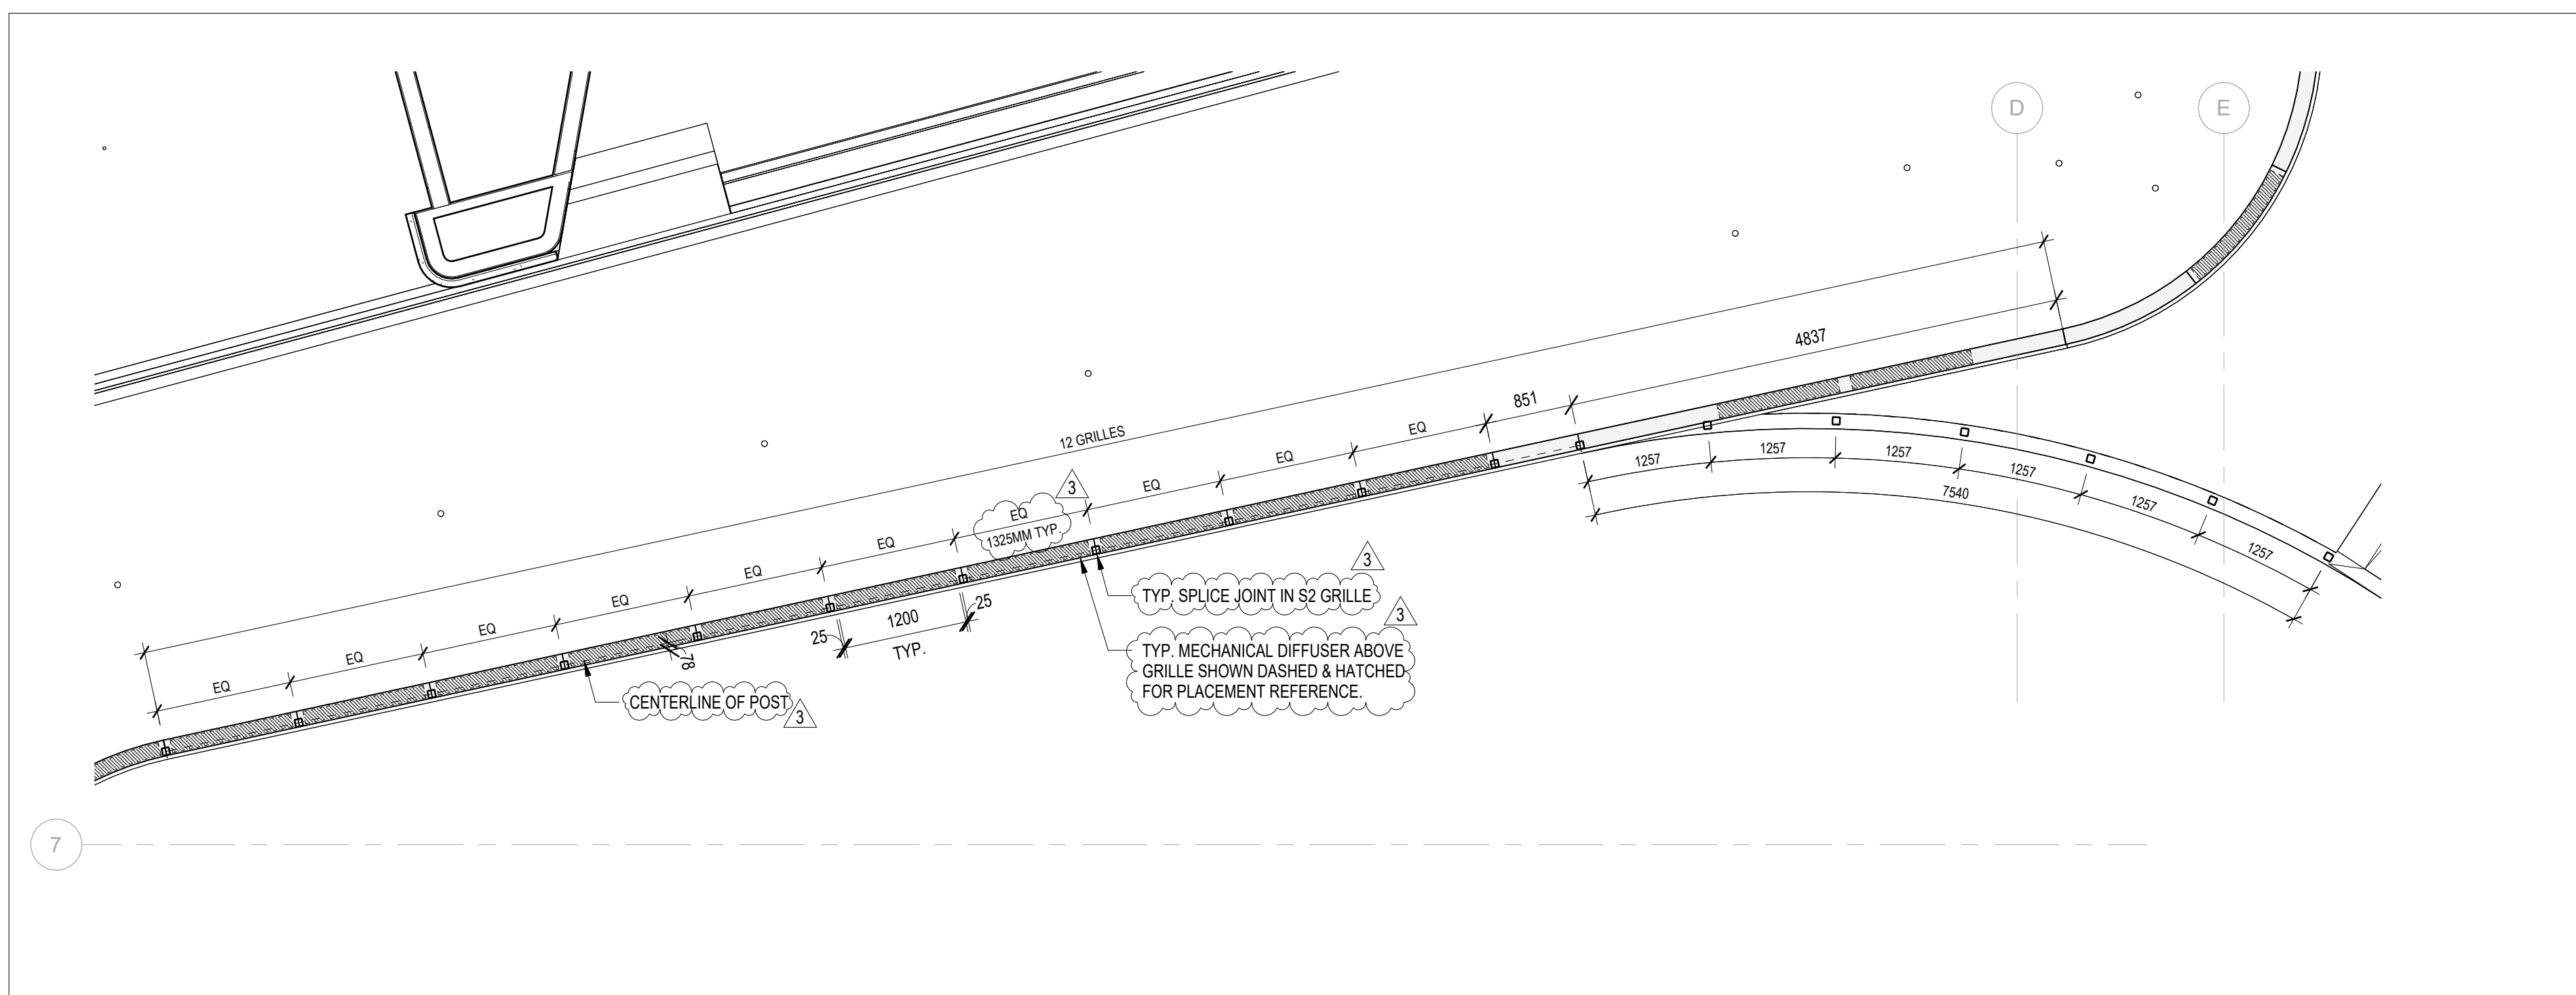


6 LEVEL 1 RCP - CEILING GRILLES - 6

A9.141 1:50

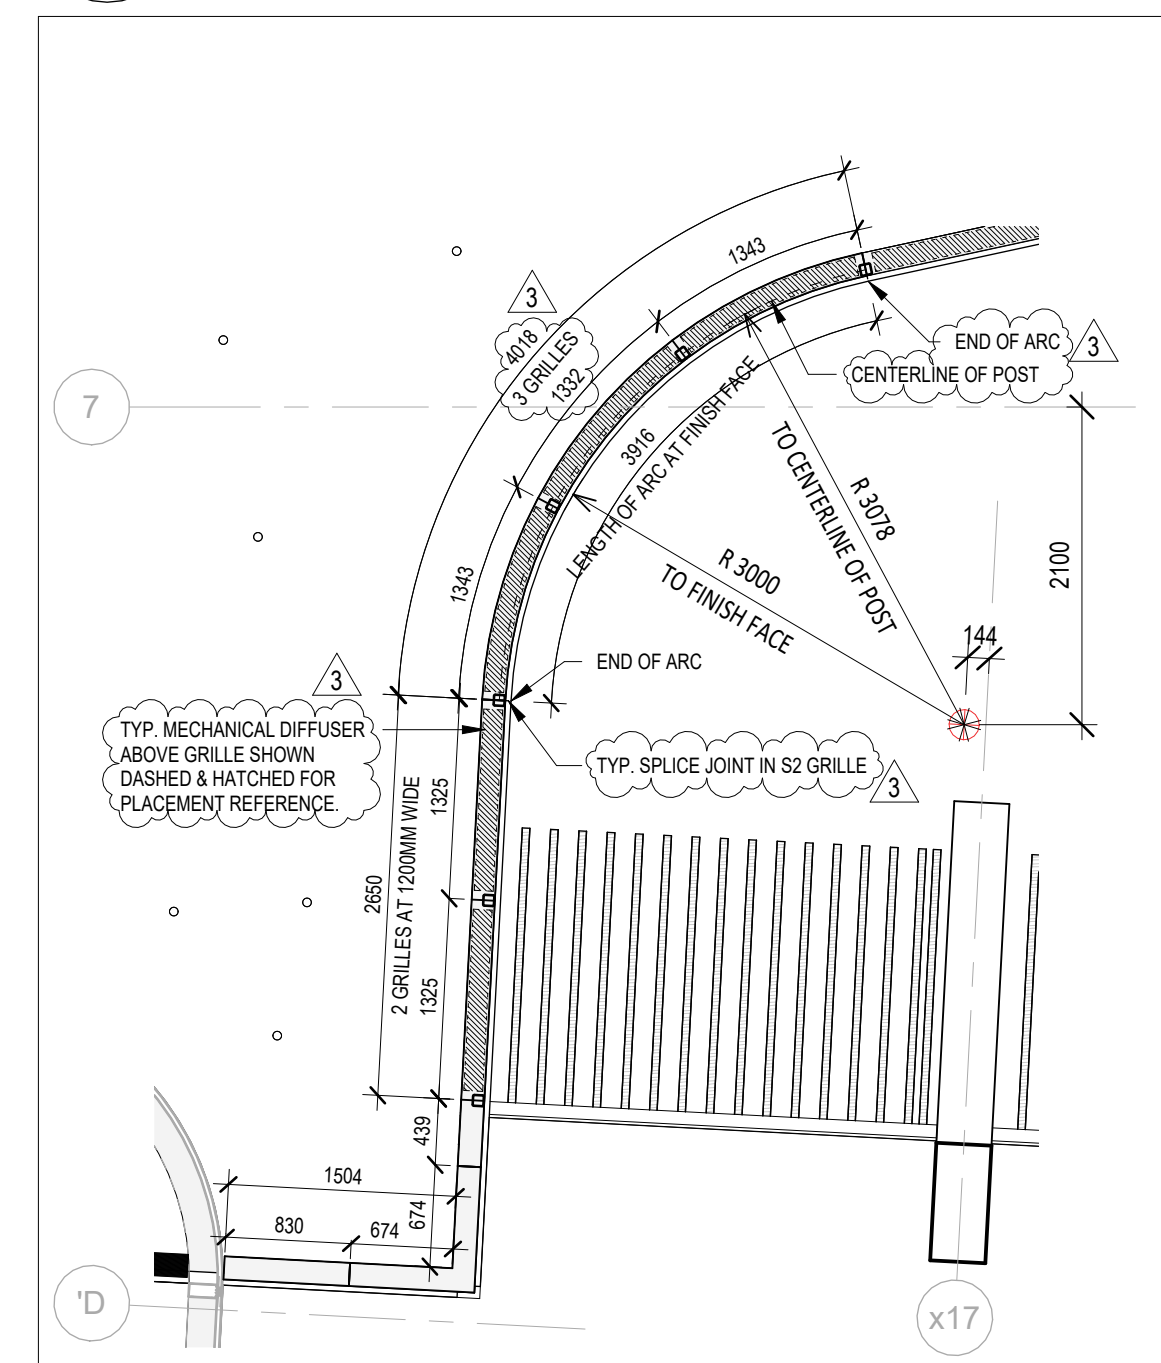


5 LEVEL 1 RCP - CEILING GRILLES - 4

A9.141 1:50

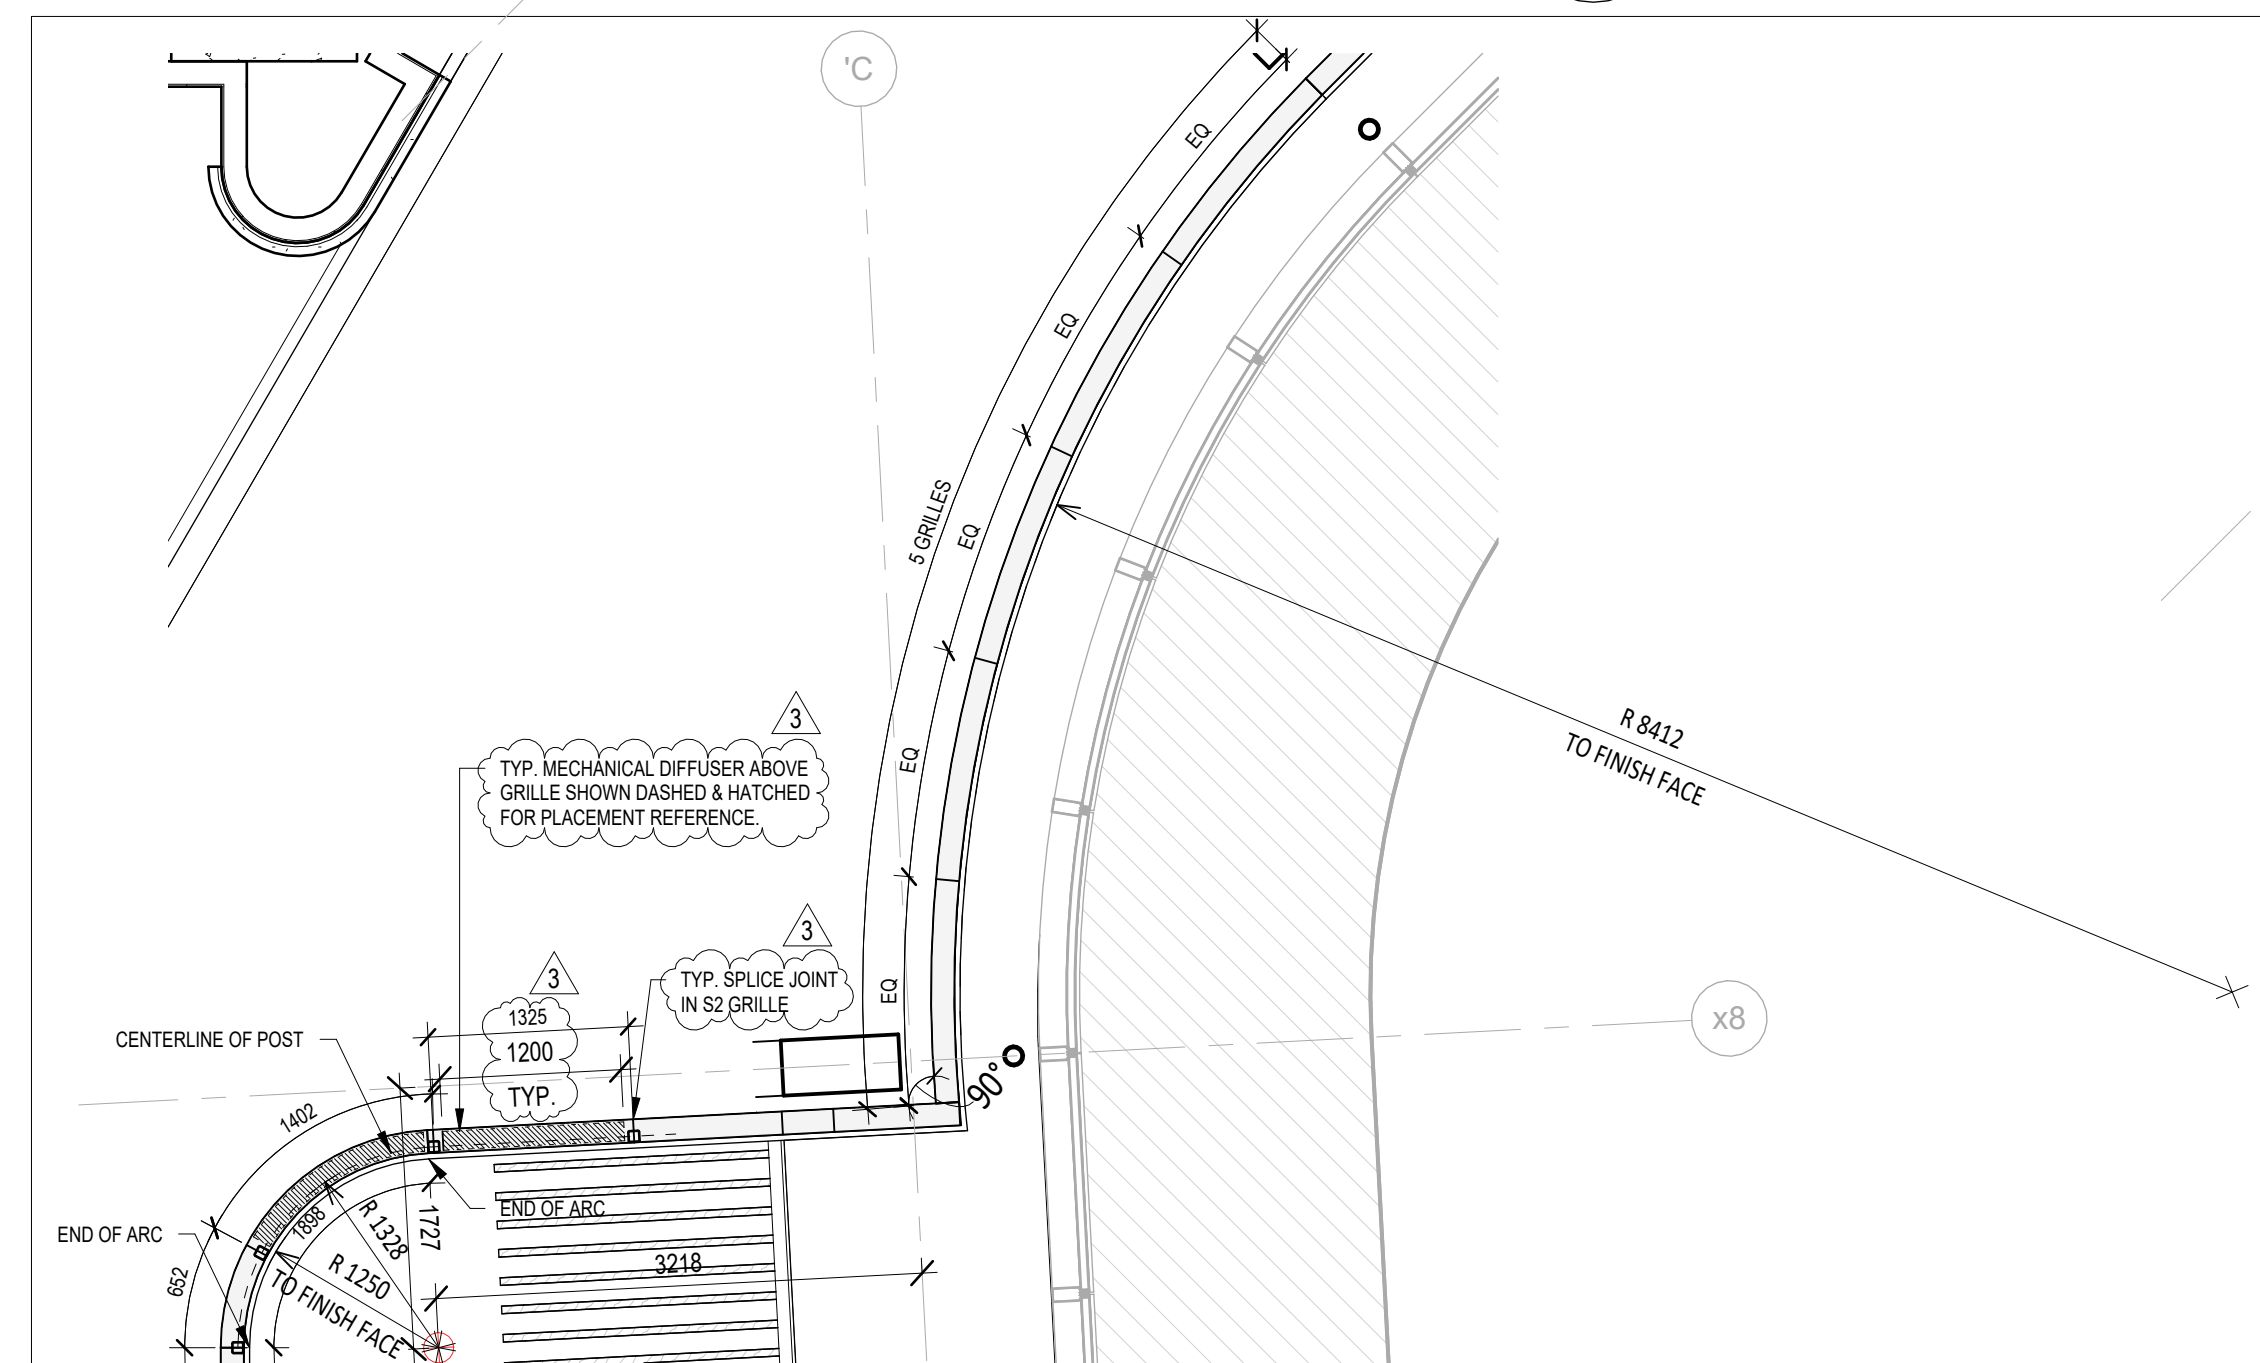


4 LEVEL 1 RCP - CEILING GRILLES - 3

A9.141 1:50

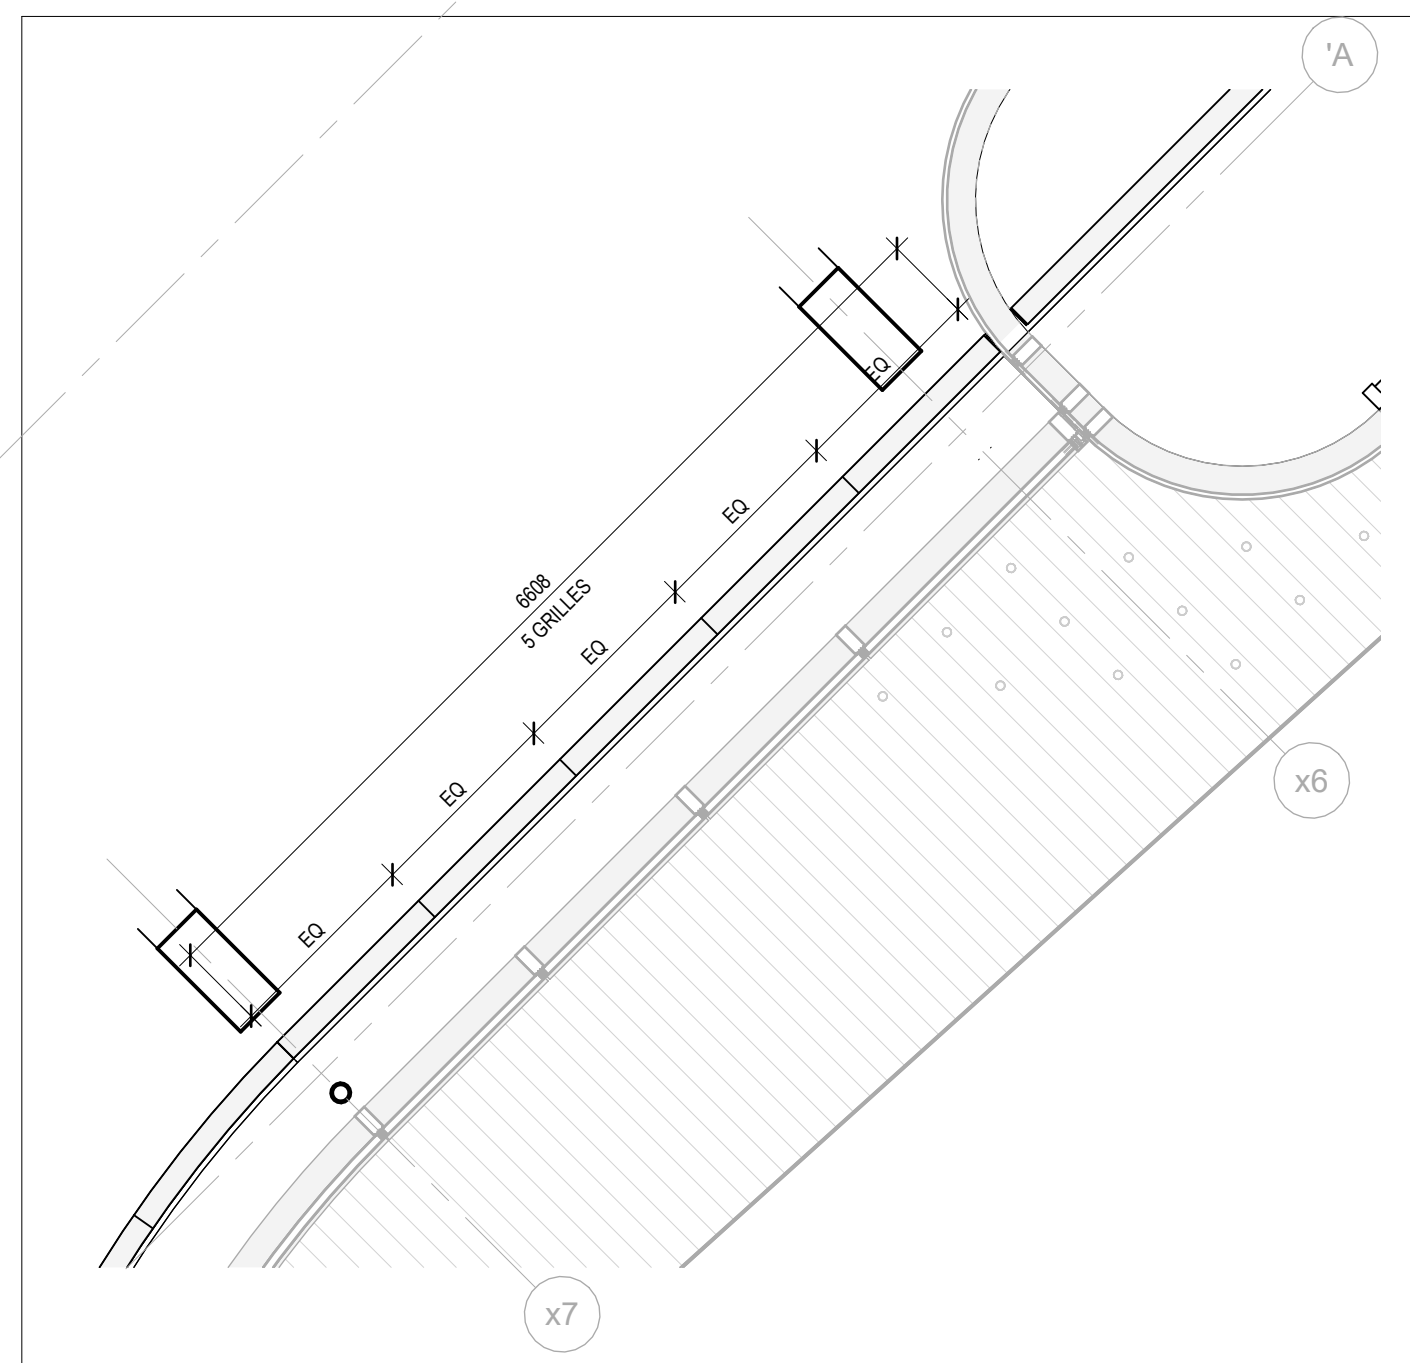


3 LEVEL 1 RCP - CEILING GRILLES - 2

A9.141 1:50

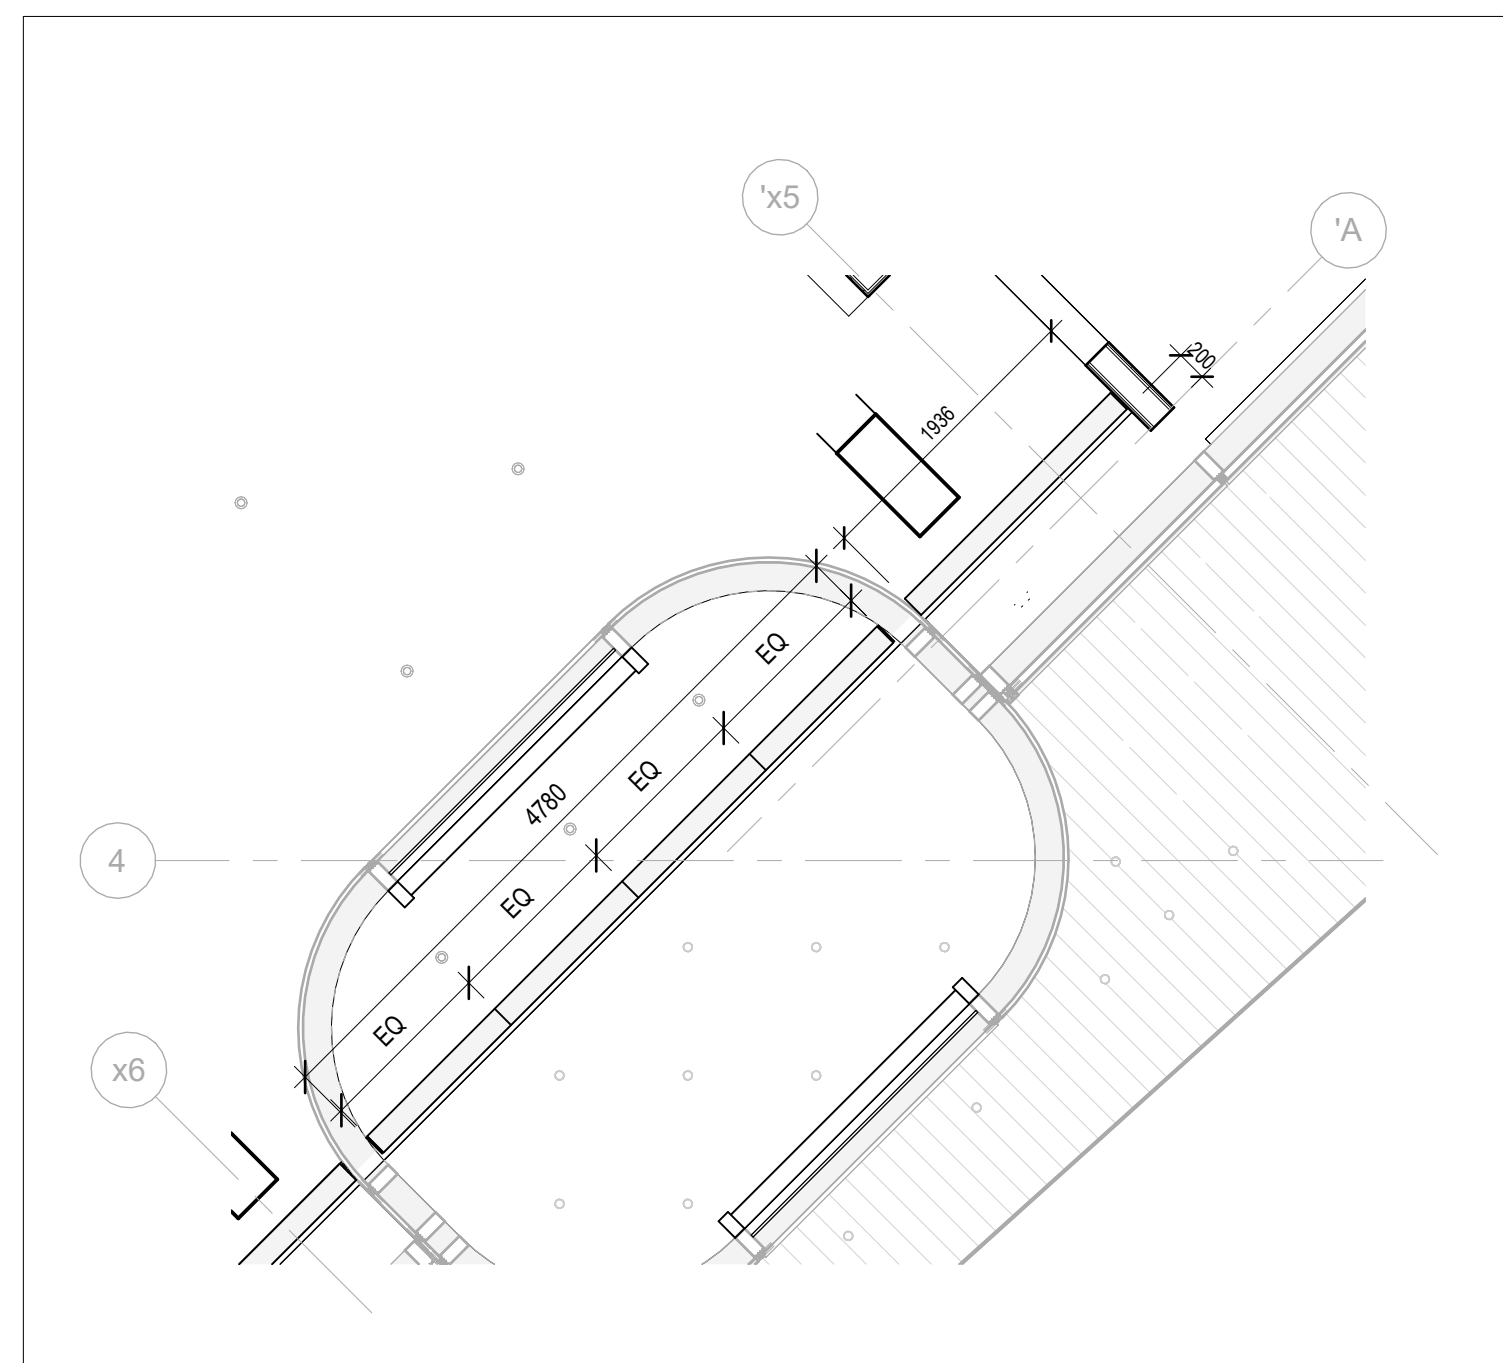

2 LEVEL 1 RCP - CEILING GRILLES - 1

A9.141 1:50

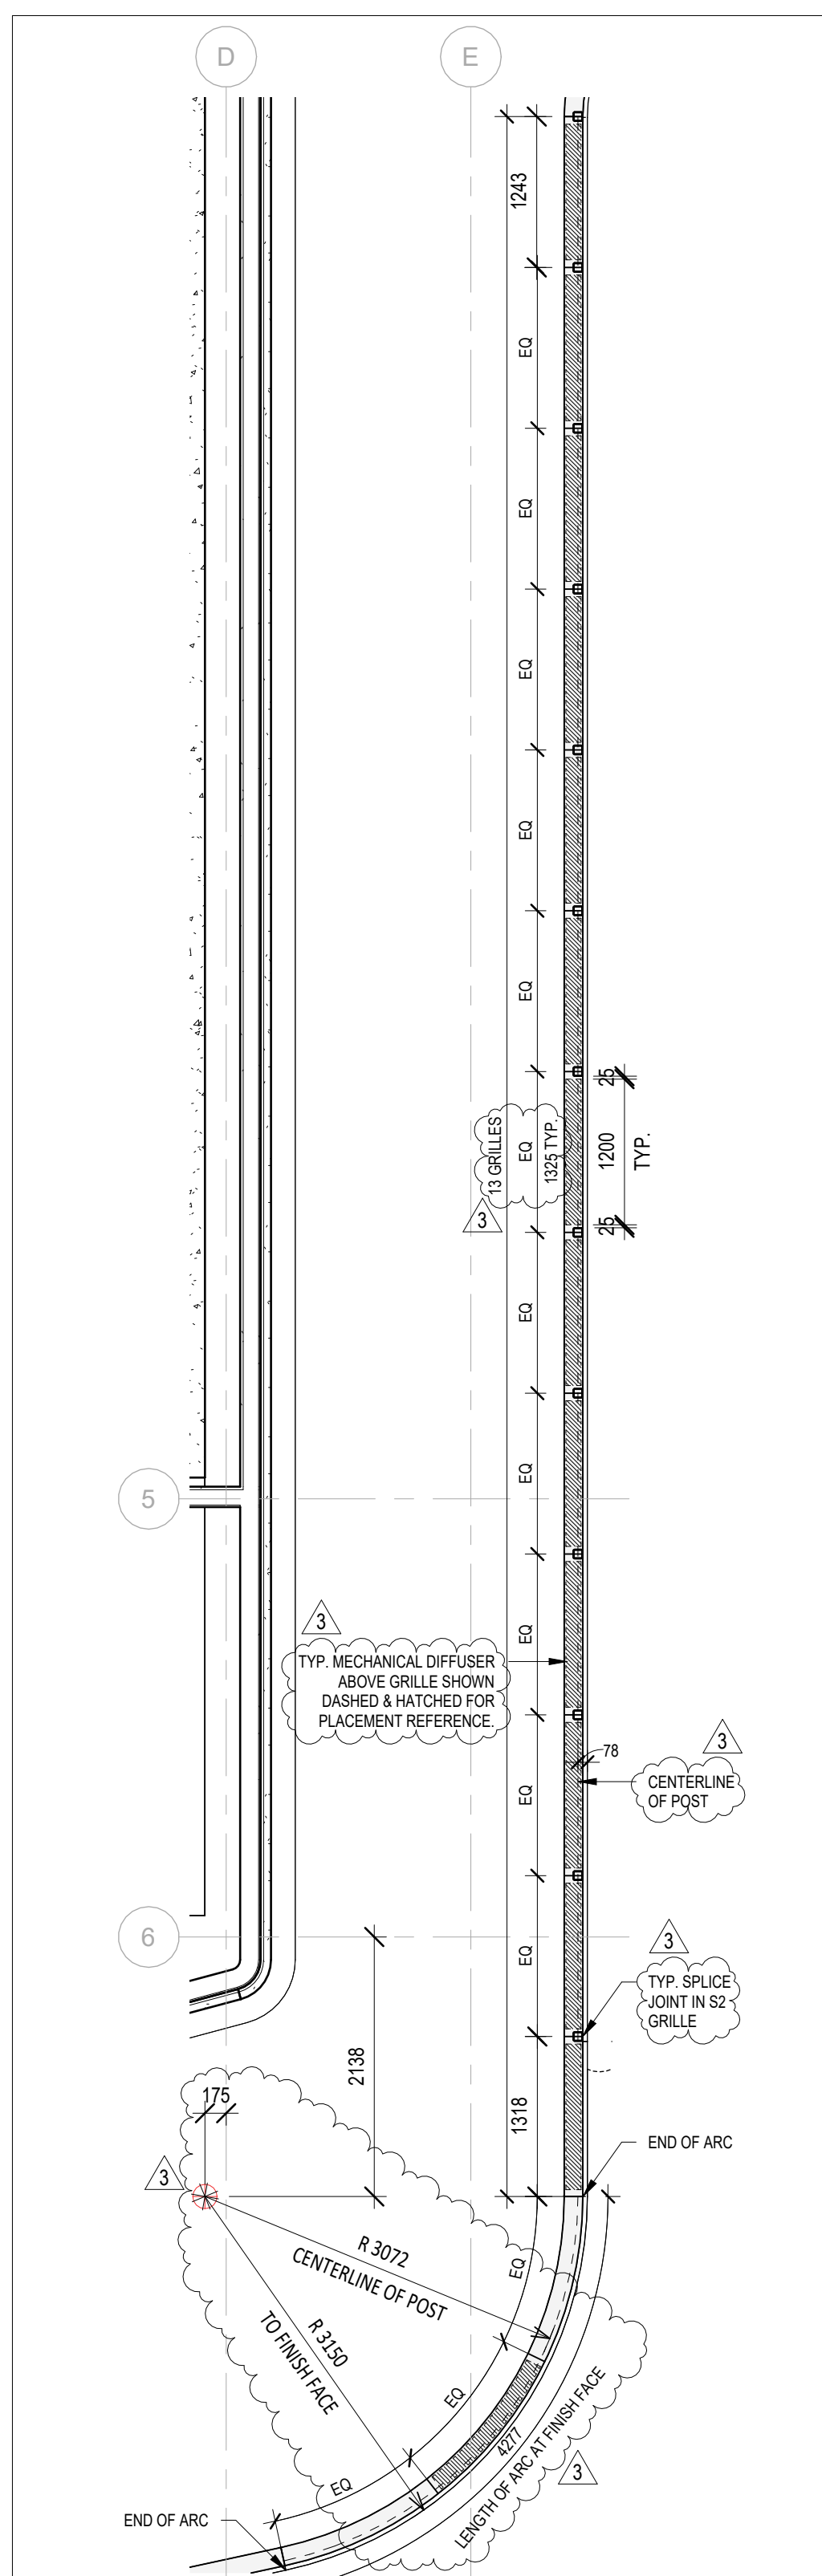

1 LEVEL 1 RCP - CEILING GRILLES - 5

A9.141 1:50

COPYRIGHT © THAT OF THE ARCHITECT.
ANY USE OF THIS DRAWING REPRODUCED BY ANY
PERSON FOR ANY REASON WITHOUT THE WRITTEN
APPROVAL OF THE ARCHITECT IS TO BE REJECTED.
THE ARCHITECT IS NOT LIABLE FOR ANY LOSS OR
DAMAGE OF INFORMATION RESULTING FROM
SUBSEQUENT REPRODUCTION OF THE ORIGINAL DRAWING.

GENERAL NOTES:
1. DRAWINGS ARE NOT TO BE SCALED. CONTRACTOR SHALL
VERIFY ALL EXISTING CONDITIONS AND CONDITIONS
REQUIRED TO PERFORM THE WORK AND ALL REPORT ANY
DISCREPANCIES WITH THE CONTRACT DOCUMENTS TO THE
ARCHITECT FOR USE IN THE CONSTRUCTION WORK.
2. THE ARCHITECTURAL DRAWINGS ARE TO BE READ IN
CONJUNCTION WITH ALL OTHER CONTRACT DOCUMENTS
INCLUDING THE PROJECT MANUAL AND THE STRUCTURAL,
MECHANICAL, ELECTRICAL, AND PLUMBING (M.E.P.) SCHEDULES.
DIFFERENCES BETWEEN THE CONTRACT DOCUMENTS
WITH RESPECT TO THE QUANTITY, SIZE OR KIND OF
WORK, THE SEQUENCE OF WORK, OR THE LOCATION OF
WORK, THE SEQUENCE OF WORK, OR THE LOCATION OF
ELECTRICAL, MECHANICAL, AND PLUMBING (M.E.P.) WORK
SHOWN ON THE ARCHITECTURAL DRAWINGS SHALL GOVERN
OVER THE SEQUENCE OF WORK, OR THE LOCATION OF
ELECTRICAL, MECHANICAL, AND PLUMBING (M.E.P.) WORK
SHOWN ON THE ARCHITECTURAL DRAWINGS.
3. THE ARCHITECT HAS NOT BEEN RETAINED FOR
SUPERVISION OF CONSTRUCTION AND ASSUMES NO
RESPONSIBILITY FOR MEANS, METHODS AND TECHNIQUES
OF CONSTRUCTION.
4. THESE DOCUMENTS ARE NOT TO BE USED FOR
CONSTRUCTION UNLESS SPECIFICALLY NOTED FOR SUCH
PURPOSE.

NO.	REVISION	DATE	BY	CHKD.
1	ISSUED FOR BIDDING	2024-11-22	AS	AS
2	ISSUED FOR TENDER	2024-11-22	AS	AS
3	ISSUED FOR TENDER	2024-11-22	AS	AS



ARCHITECTS
KPMB
KPMB Architects
351 King Street East, Suite 1200
Toronto, Canada M5A 0L6
+1 416 577 1104
kpmbs@kpmbarchitects.com


HINDLE ARCHITECTS
Hindle Architects
Suite 510, Burns Building
237 8th Avenue SE
Calgary, AB
T2G 0C3

TAW
Tawana Architecture Collective
2503, 1718 5 Ave SE
Calgary, AB T2G 0T1
(403) 451 0294

CMILC
Arts Commons Transformation
Phase 1 Expansion
ACT
236 8th Avenue S.E. Calgary, Alberta

Project No. 2041
Scale As indicated
Plot Date 01/05/25
**LEVEL 1 - GRILLE
SCHEDULE RCP**

A9.141

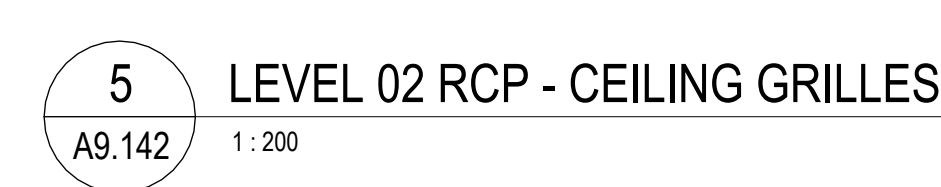

A9.142