


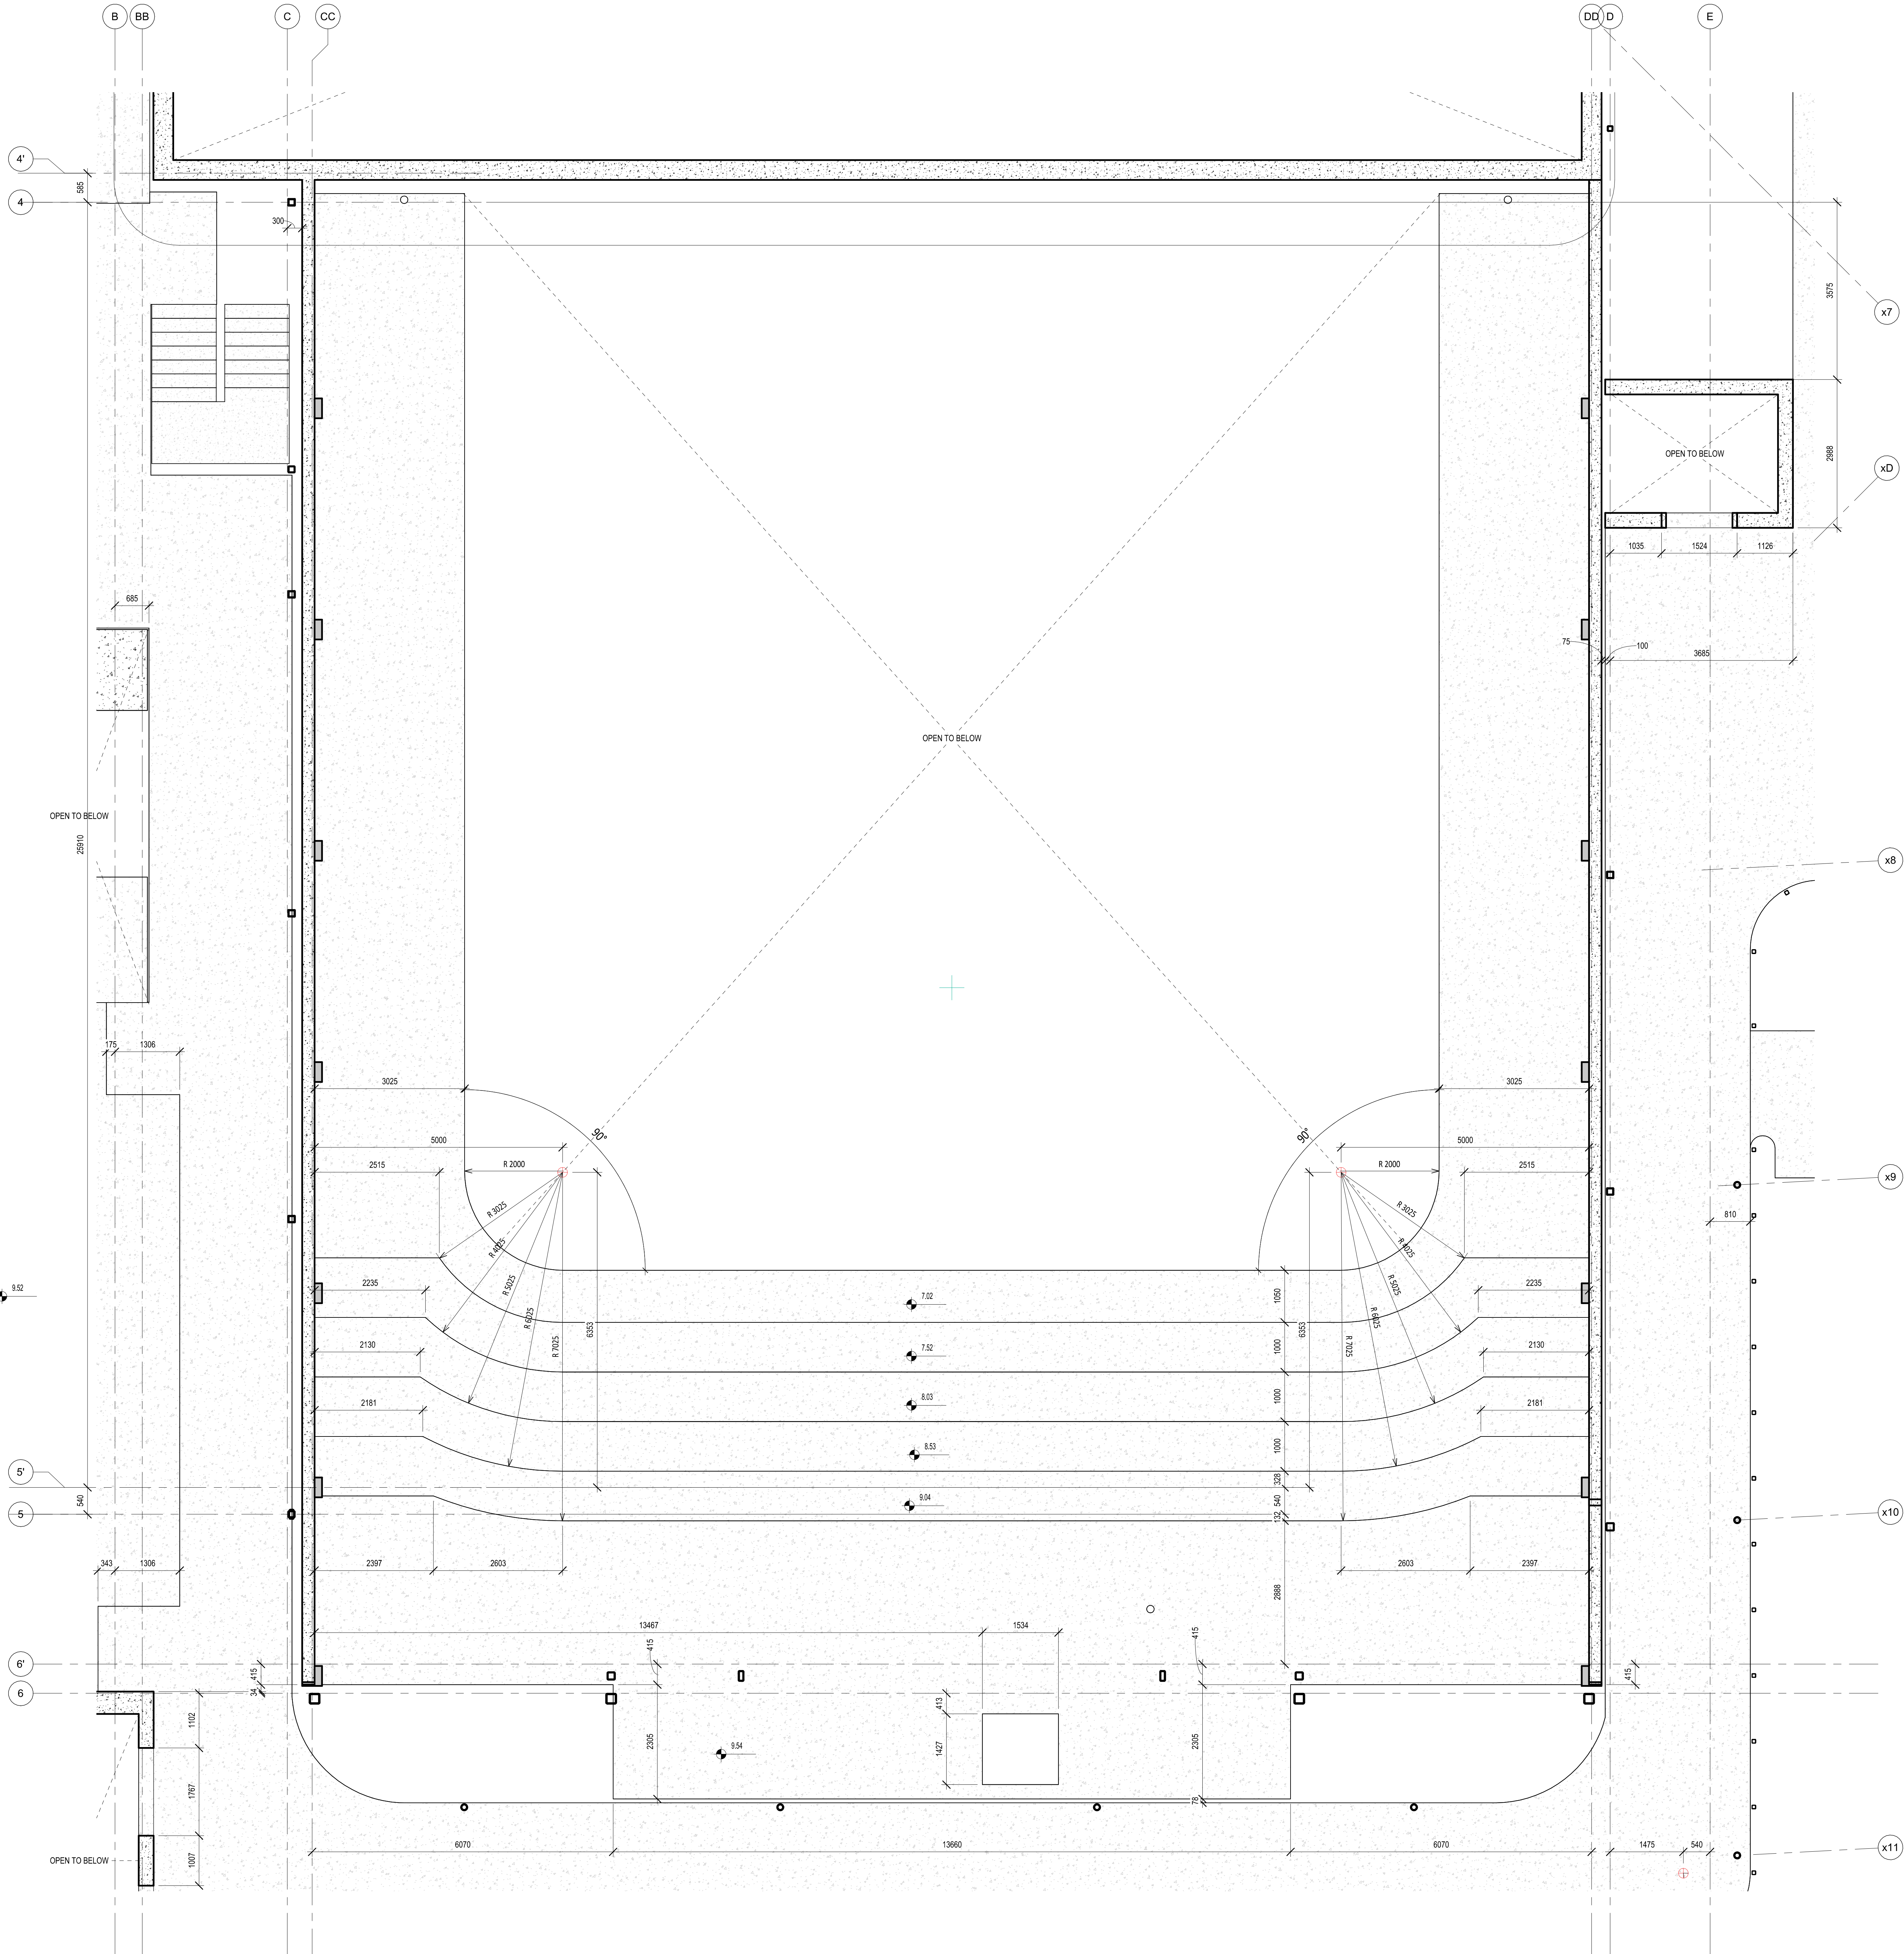


COPYRIGHT IS THAT OF THE ARCHITECT.
ANY USE OF THIS DRAWING REPRODUCED BY ANY
MANNER OR BY ANY MEDIA WITHOUT THE WRITTEN
APPROVAL OF THE ARCHITECT IS TO BE HELD FOR
THE ARCHITECT IS NOT LIABLE FOR ANY LOSS OR
DAMAGE TO INFORMATION RESULTS FROM
SUBSEQUENT REPRODUCTION OF THE ORIGINAL DRAWING.

ARCHITECT'S NOTES:
1. DRAWINGS ARE NOT TO BE SCALED. CONTRACTOR SHALL
VERIFY ALL EXISTING CONDITIONS AND DIMENSIONS
BEFORE TO PERFORM THE WORK AND ALL REPORT ANY
VARIATIONS WITH THE CONTRACT DOCUMENTS TO THE
ARCHITECT FOR THE CONTRACTOR'S REVIEW.
2. THE ARCHITECTURAL DRAWINGS ARE TO BE READ IN
CONJUNCTION WITH ALL OTHER CONTRACT DOCUMENTS
INCLUDING THE PROJECT MANUAL AND THE STRUCTURAL,
MECHANICAL AND ELECTRICAL DRAWINGS. IN CASE OF
DIFFERENCE BETWEEN THE CONTRACT DOCUMENTS
WITH RESPECT TO THE QUANTITY, SCOPE OR SEQUENCE OF
WORK, THE QUANTITY SHALL PREVAIL.
3. POSITIONS OF EXPOSED OR FINISHED MECHANICAL OR
ELECTRICAL, PLUMBING, FITTINGS AND PIPING ARE
INDICATED ON THE ARCHITECTURAL DRAWINGS. LOCATIONS
SHOWN ON THE ARCHITECTURAL DRAWINGS SHALL GOVERN
OVER MECHANICAL, ELECTRICAL, PLUMBING, FITTINGS,
MECHANICAL AND ELECTRICAL ITEMS NOT CLEARLY
LOCATED WILL BE LOCATED AS DIRECTED BY THE
ARCHITECT.
4. DIMENSIONS INDICATED ARE TAKEN BETWEEN THE FACES
UNLESS OTHERWISE SPECIFIED OTHERWISE NOTED.
5. THE ARCHITECT HAS NOT BEEN RETAINED FOR
SUPERVISION OF CONSTRUCTION AND ASSUMES NO
RESPONSIBILITY FOR MEANS, METHODS AND TECHNIQUES
OF CONSTRUCTION.
6. THESE DOCUMENTS ARE NOT TO BE USED FOR
CONSTRUCTION UNLESS SPECIFICALLY NOTED FOR SUCH
PURPOSE.

1	2024-06-28	ISSUED FOR CONSULTATION
2	2024-06-28	ISSUED FOR TENDER PACKAGE 1
3	2024-06-28	ISSUED FOR TENDER PACKAGE 2

KEY PLAN

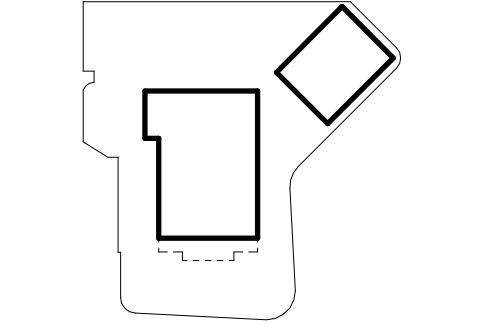

SCALE



ARCHITECTS

KPMB

KPMB Architects
351 King Street East, Suite 1200
Toronto, Canada M5A 0L6
+1 416 577 5104
kpm@kpmarchitects.com


HINDLE ARCHITECTS

Hindle Architects
Suite 510, Burns Building
237 8th Avenue SE
Calgary, AB
T2G 0C3

TAW
Tawana Architecture Collective
8203, 118 5 Ave SE
Calgary, AB T2G 0T1
(403) 451 0294

CMILC
Arts Commons Transformation
Phase 1 Expansion

ACT
206 8th Avenue S.E. Calgary, Alberta

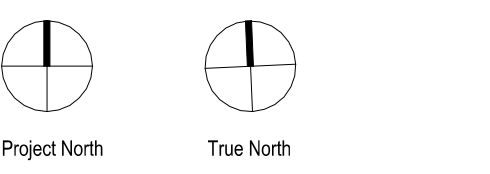

Project No. 2041
Scale 1:50
Plot Date 2024-06-28

**ENLARGED SLAB EDGE
PLAN - LEVEL 3 - LARGE
HALL**

A2.464