


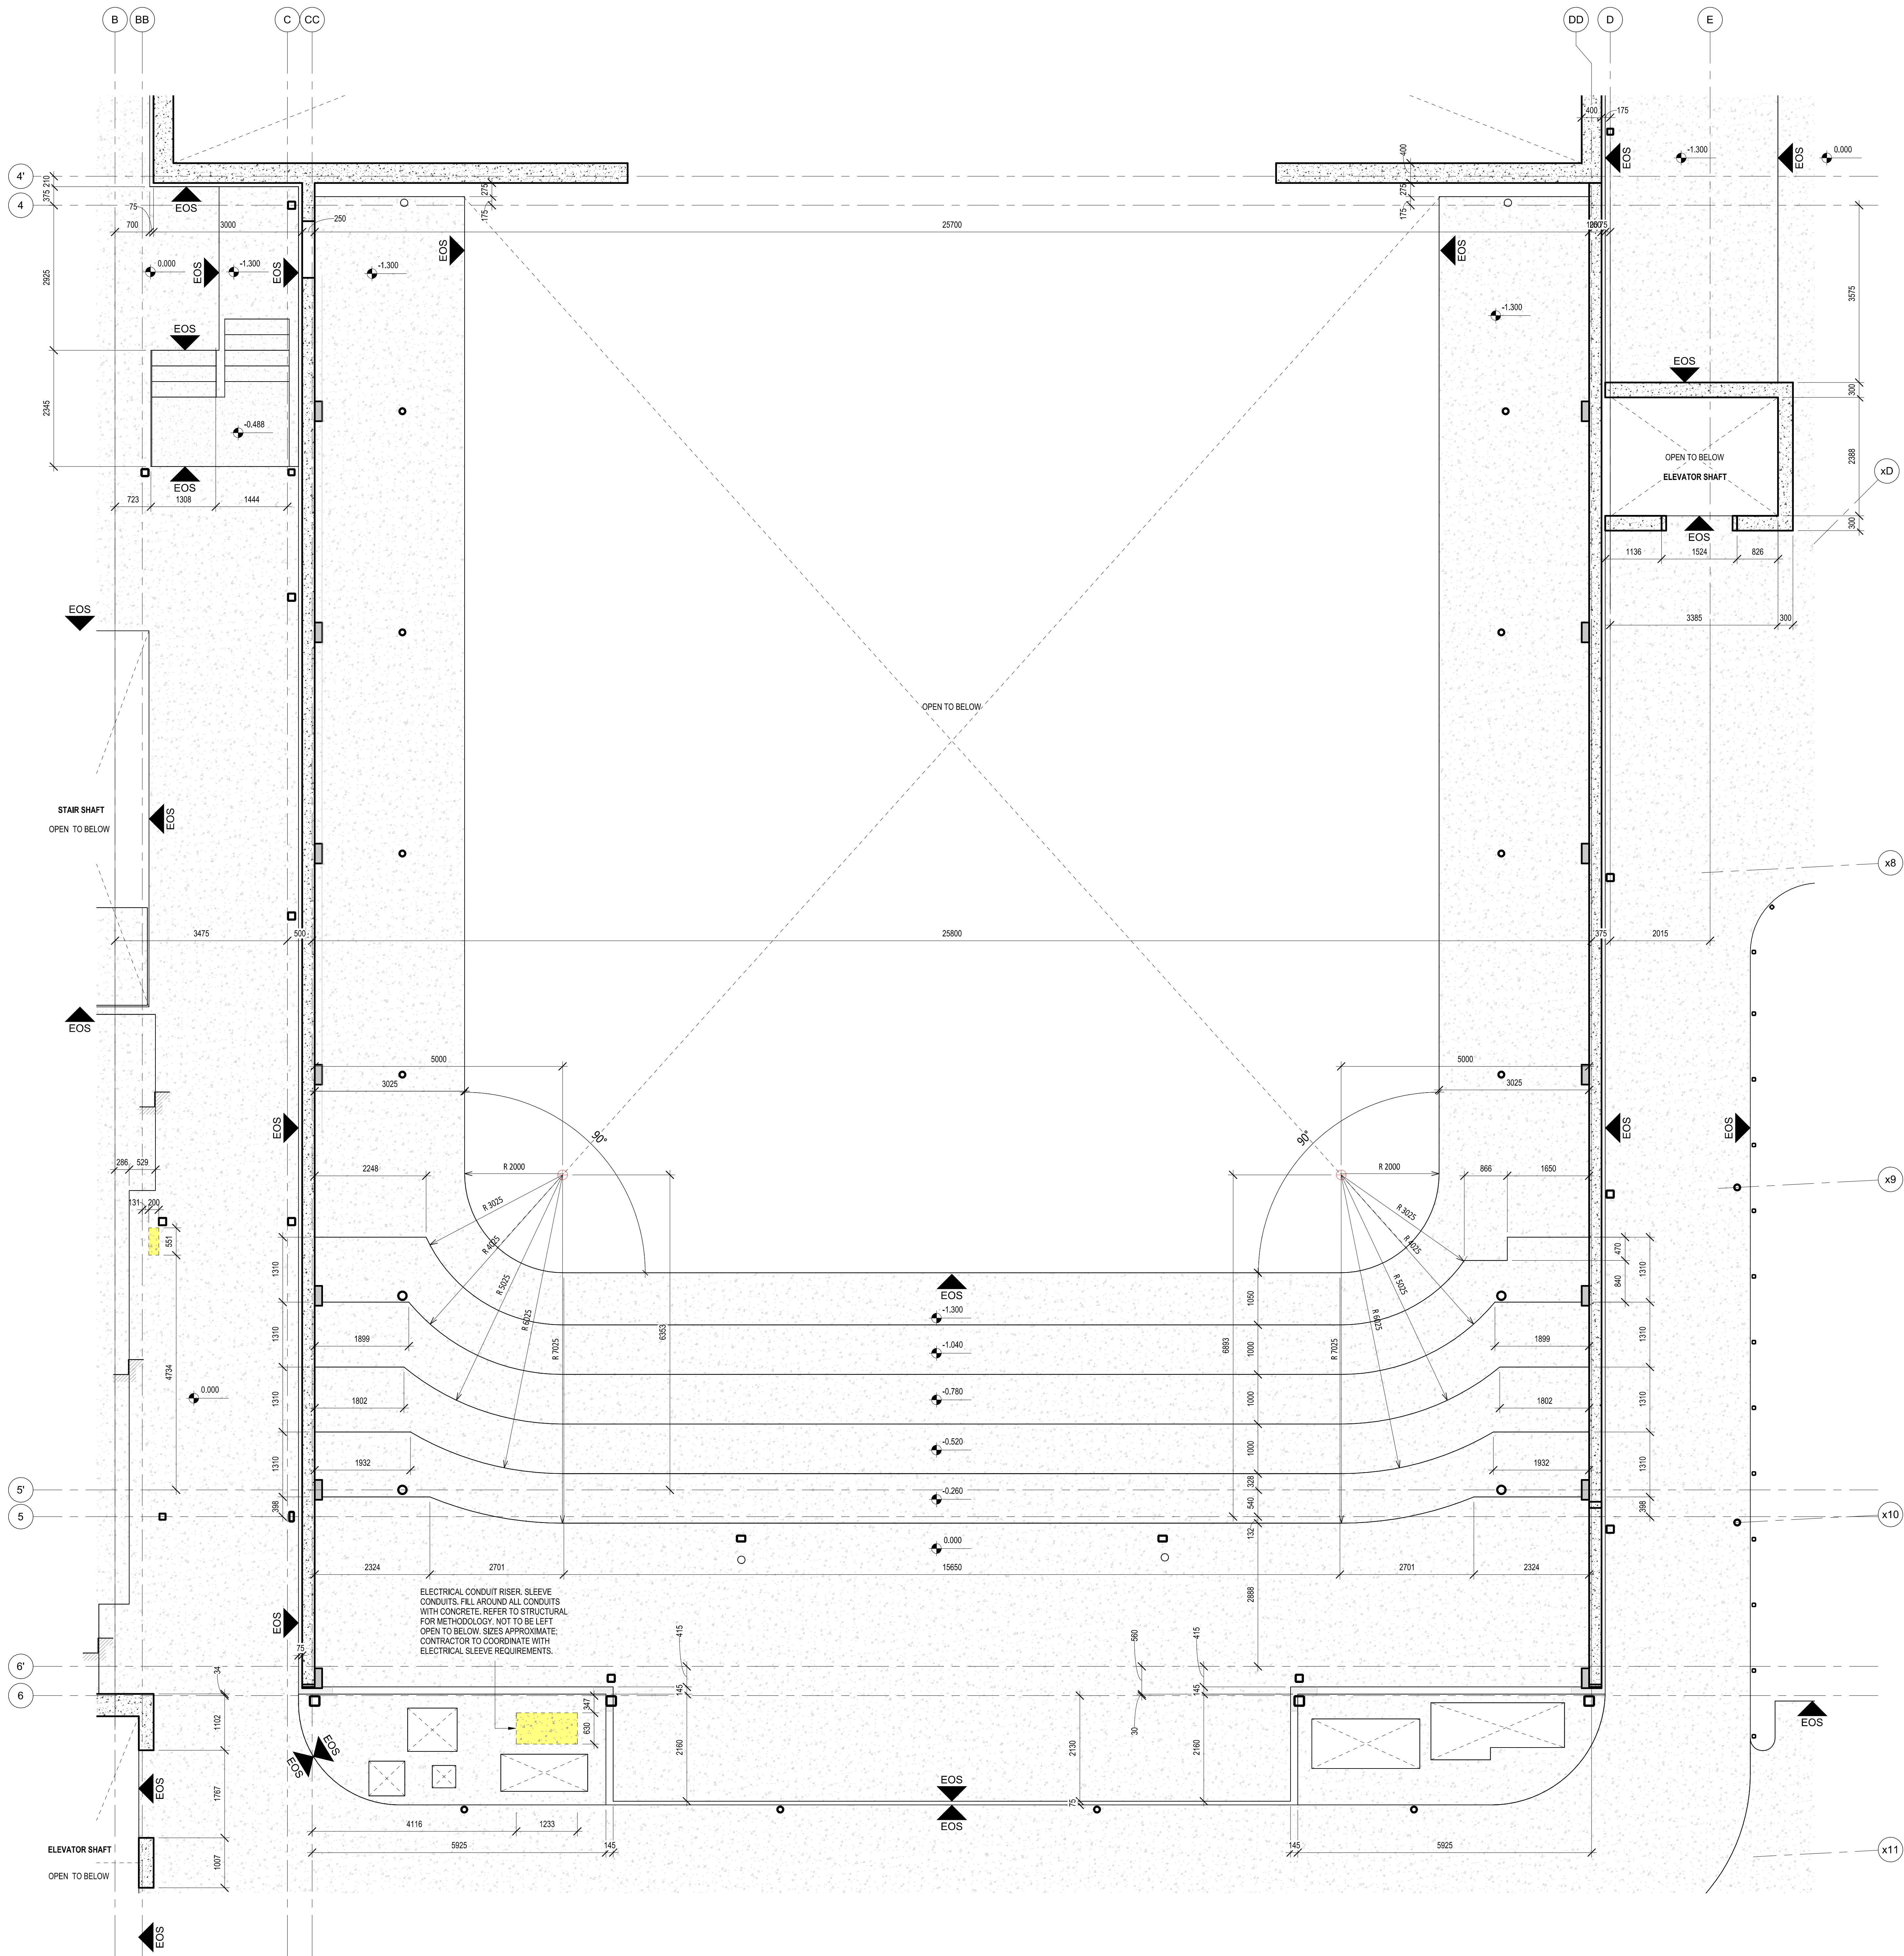


COPYRIGHT IS THAT OF THE ARCHITECT.
ANY USE OF THIS DRAWING REPRODUCED BY ANY
MANNER FOR ANY MEDIA WITHOUT THE WRITTEN
APPROVAL OF THE ARCHITECT IS TO BE REJECTED.
THE ARCHITECT IS NOT LIABLE FOR ANY LOSS OR
DAMAGE TO INFORMATION RESULTING FROM
SUBSEQUENT REPRODUCTION OF THE ORIGINAL DRAWING.

GENERAL NOTES:
1. DRAWINGS ARE NOT TO BE SCALED. CONTRACTOR SHALL
VERIFY ALL EXISTING CONDITIONS AND DIMENSIONS
BEFORE PROCEEDING WITH THE WORK AND ALL REPORT ANY
VARIATIONS TO THE ARCHITECT.
2. THE ARCHITECTURAL DRAWINGS ARE TO BE READ IN
CONJUNCTION WITH ALL OTHER CONTRACT DOCUMENTS
INCLUDING THE PROJECT MANUAL AND THE STRUCTURAL,
MECHANICAL AND ELECTRICAL DRAWINGS. IN CASE OF
CONFLICT, THE CONTRACT DOCUMENTS SHALL PREVAIL.
3. POSITIONS OF EXISTING OR PROPOSED MECHANICAL OR
ELECTRICAL EQUIPMENT SHALL BE INDICATED ON THE ARCHITECTURAL DRAWINGS. LOCATIONS
SHOWN ON THE ARCHITECTURAL DRAWINGS SHALL COORDINATE
WITH THE MECHANICAL AND ELECTRICAL DRAWINGS.
4. DIMENSIONS INDICATED ARE TAKEN BETWEEN THE FINES
UNLESS OTHERWISE NOTED.
5. THE ARCHITECT HAS NOT BEEN RETAINED FOR
RESPONSIBILITY FOR MEANS, METHODS AND TECHNIQUES
OF CONSTRUCTION.
6. THESE DOCUMENTS ARE NOT TO BE USED FOR
CONSTRUCTION UNLESS SPECIFICALLY NOTED FOR SUCH
PURPOSE.

1	2024-06-27	ISSUED FOR CONSULTATION
2	2024-06-27	ISSUED FOR TENDER PACKAGE 2

KEY PLAN

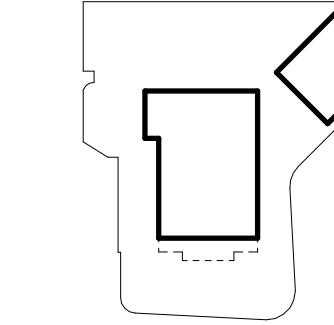

SEAL



ARCHITECTS

KPMB

KPMB Architects
351 King Street East, Suite 1200
Toronto, Canada M5A 0L6
+1 416 577 5104
kpmb@kpmbarchitects.com

HINDLE ARCHITECTS


Hindle Architects
Suite 510, Burns Building
237 8th Avenue SE
Calgary, AB
T2G 0C3

TAW
Tawana Architecture Collective
803, 218 5 Ave SE
Calgary, AB T2G 0T1
(403) 451 0294

CMILC
Arts Commons Transformation
Phase 1 Expansion



206 8th Avenue S.E. Calgary, Alberta

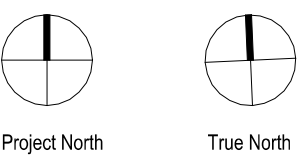

Project No. 2041
Scale 1:50
Plot Date 2024-06-28

ENLARGED SLAB EDGE
PLAN - LEVEL 4 - LARGE
HALL

A2.465