




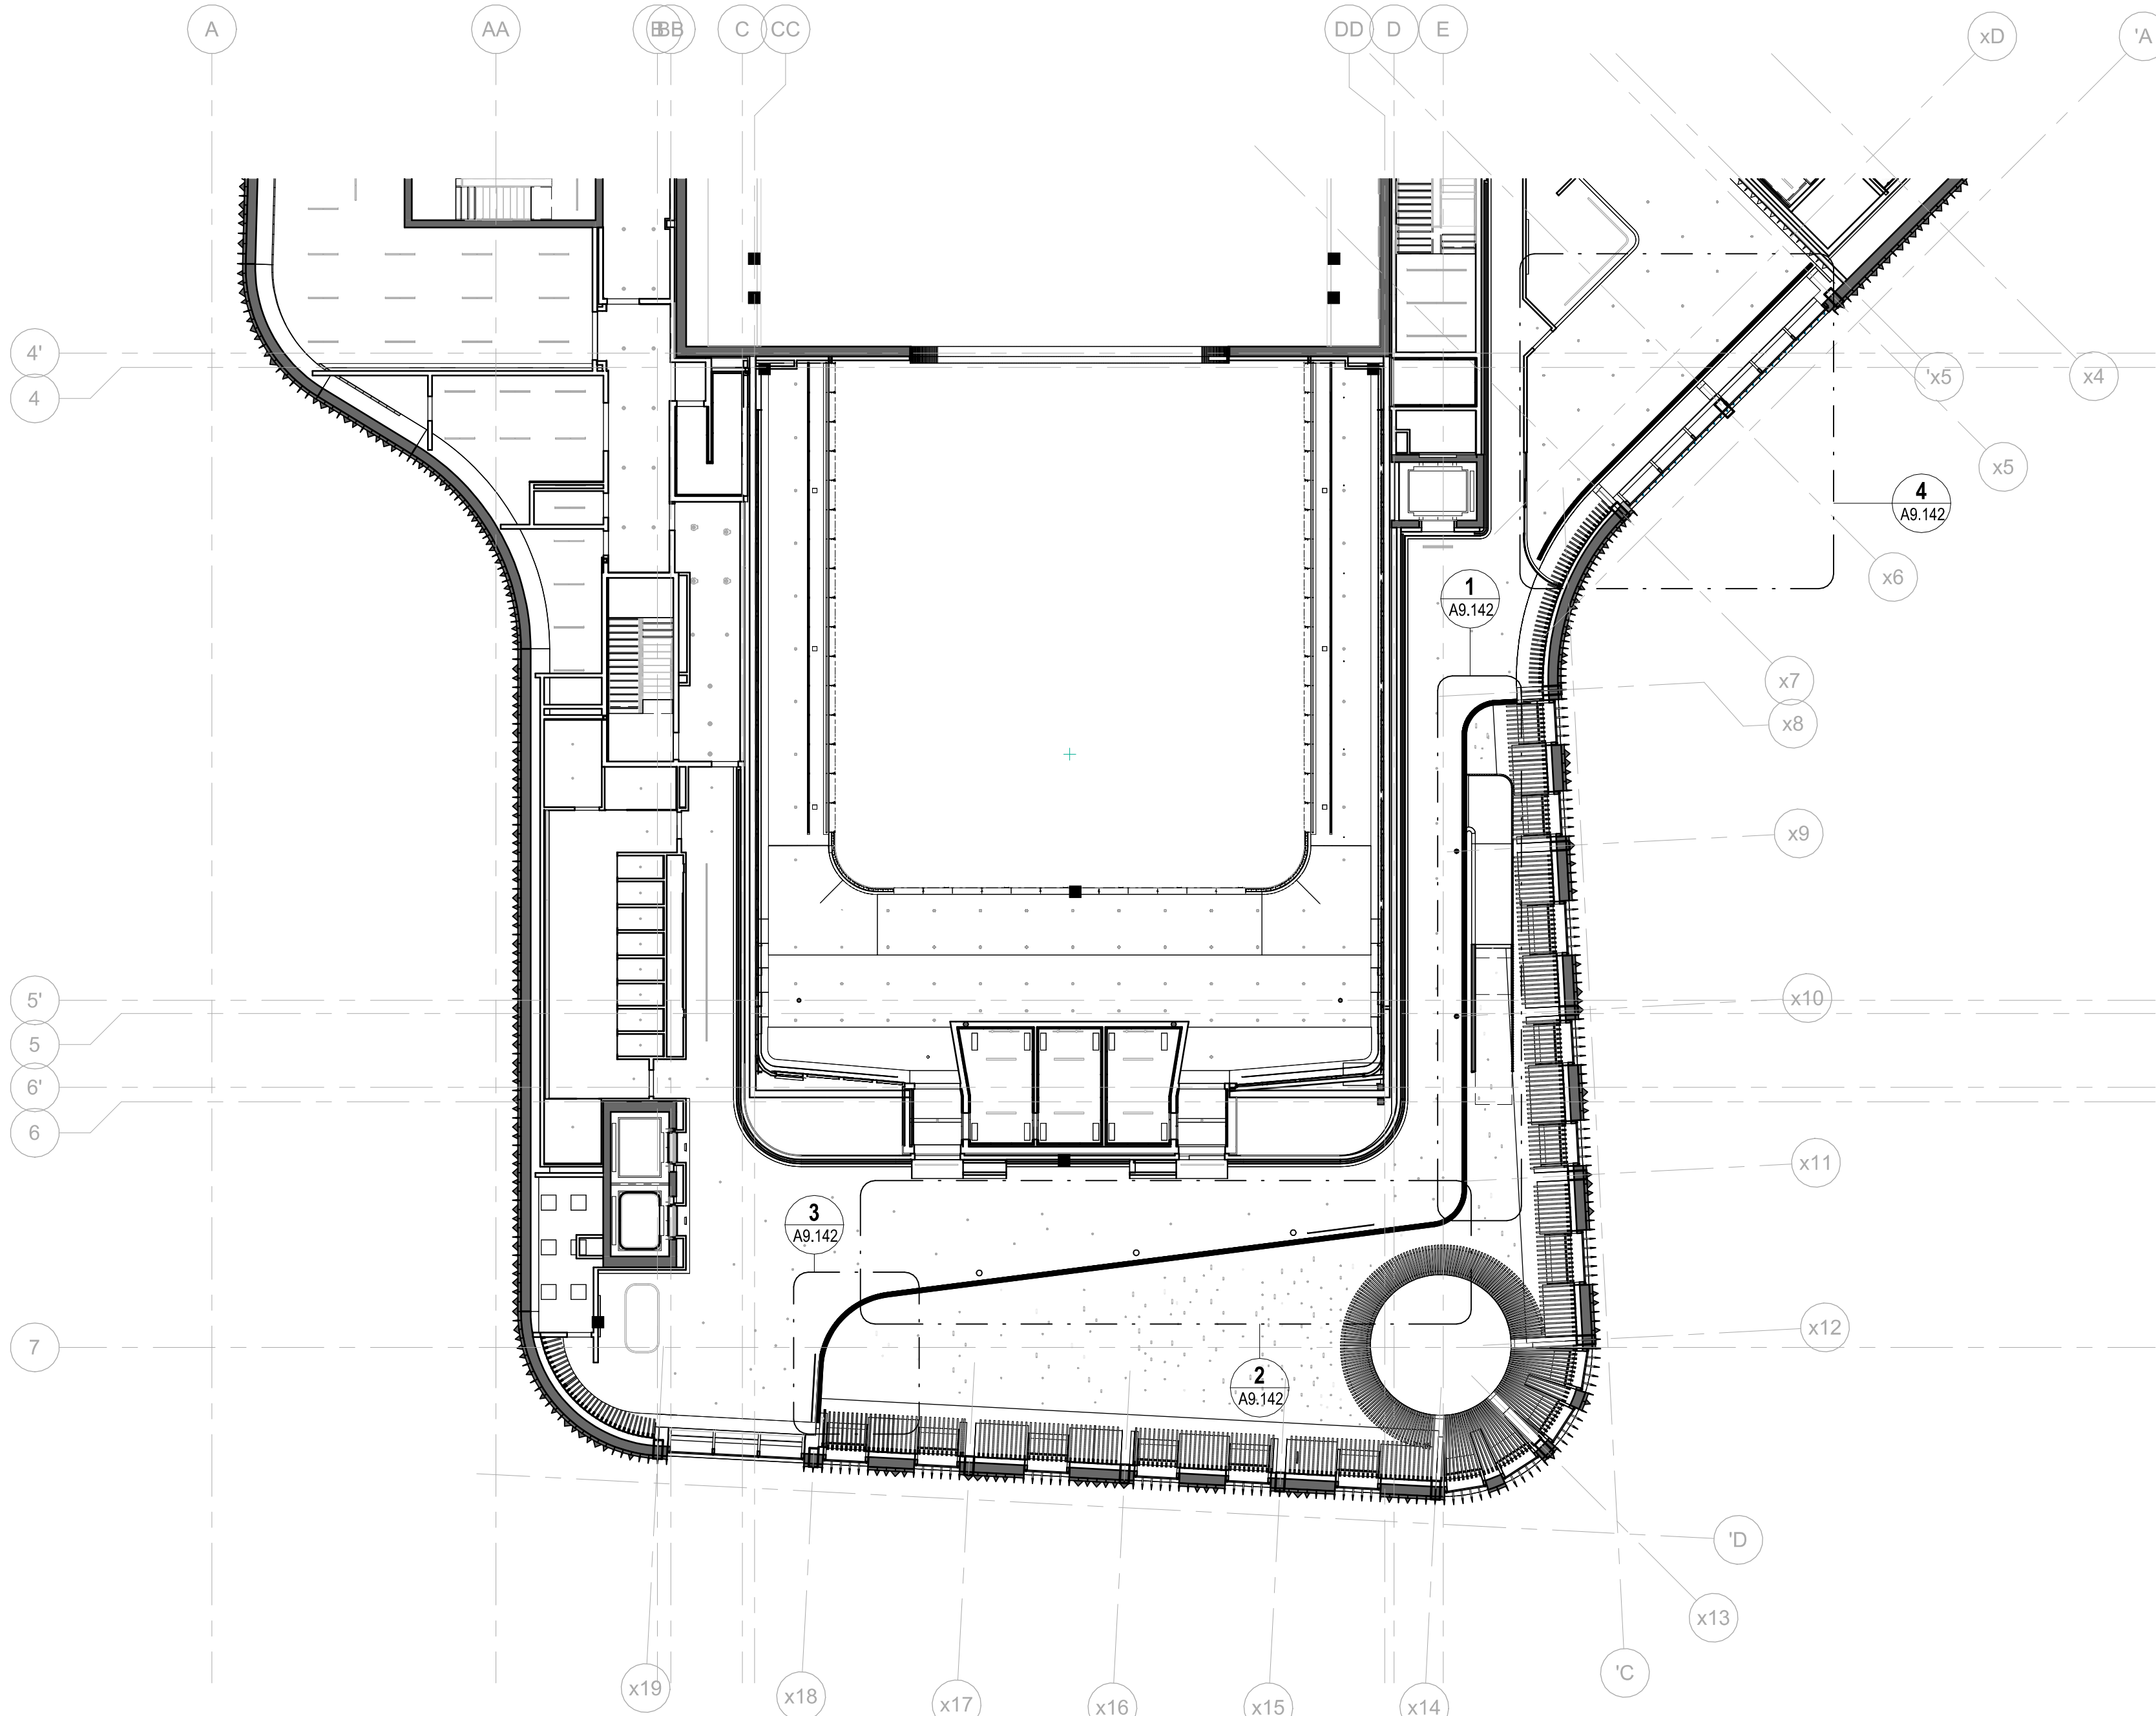


5 LEVEL 02 RCP - CEILING GRILLES
A9.142 1:200

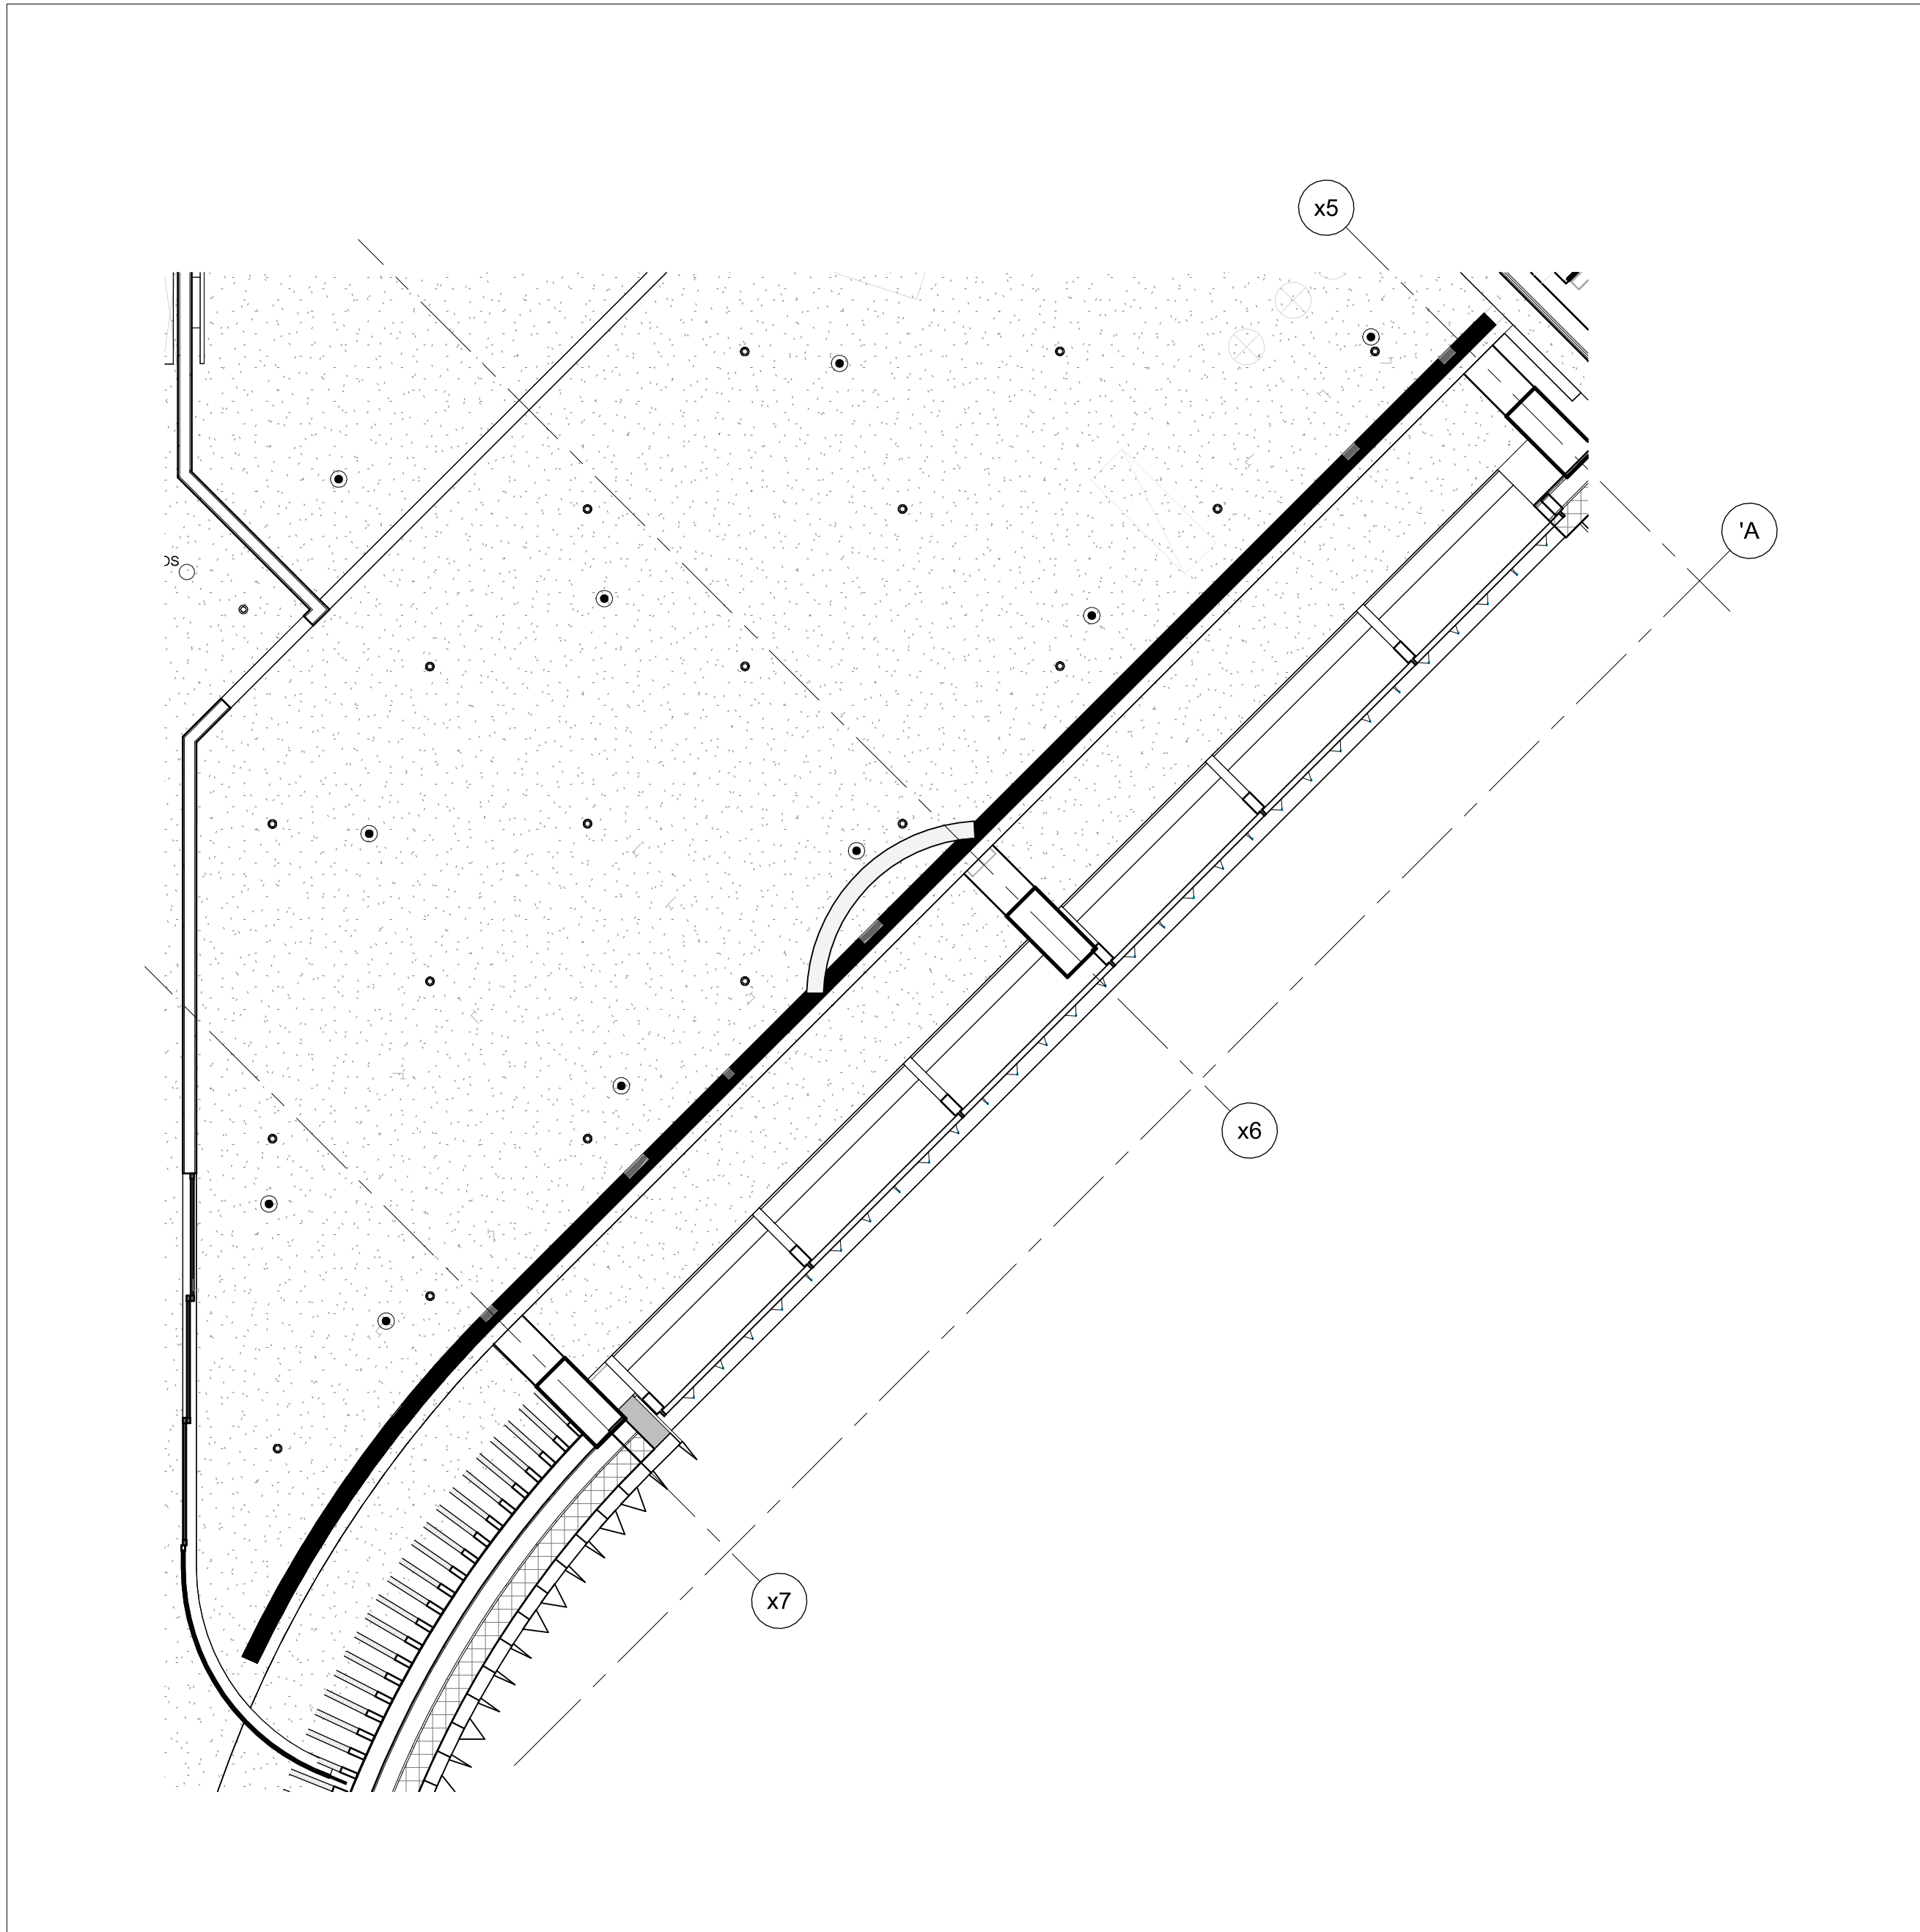


4 LEVEL 02 RCP - CEILING GRILLES - 4
A9.142 1:50

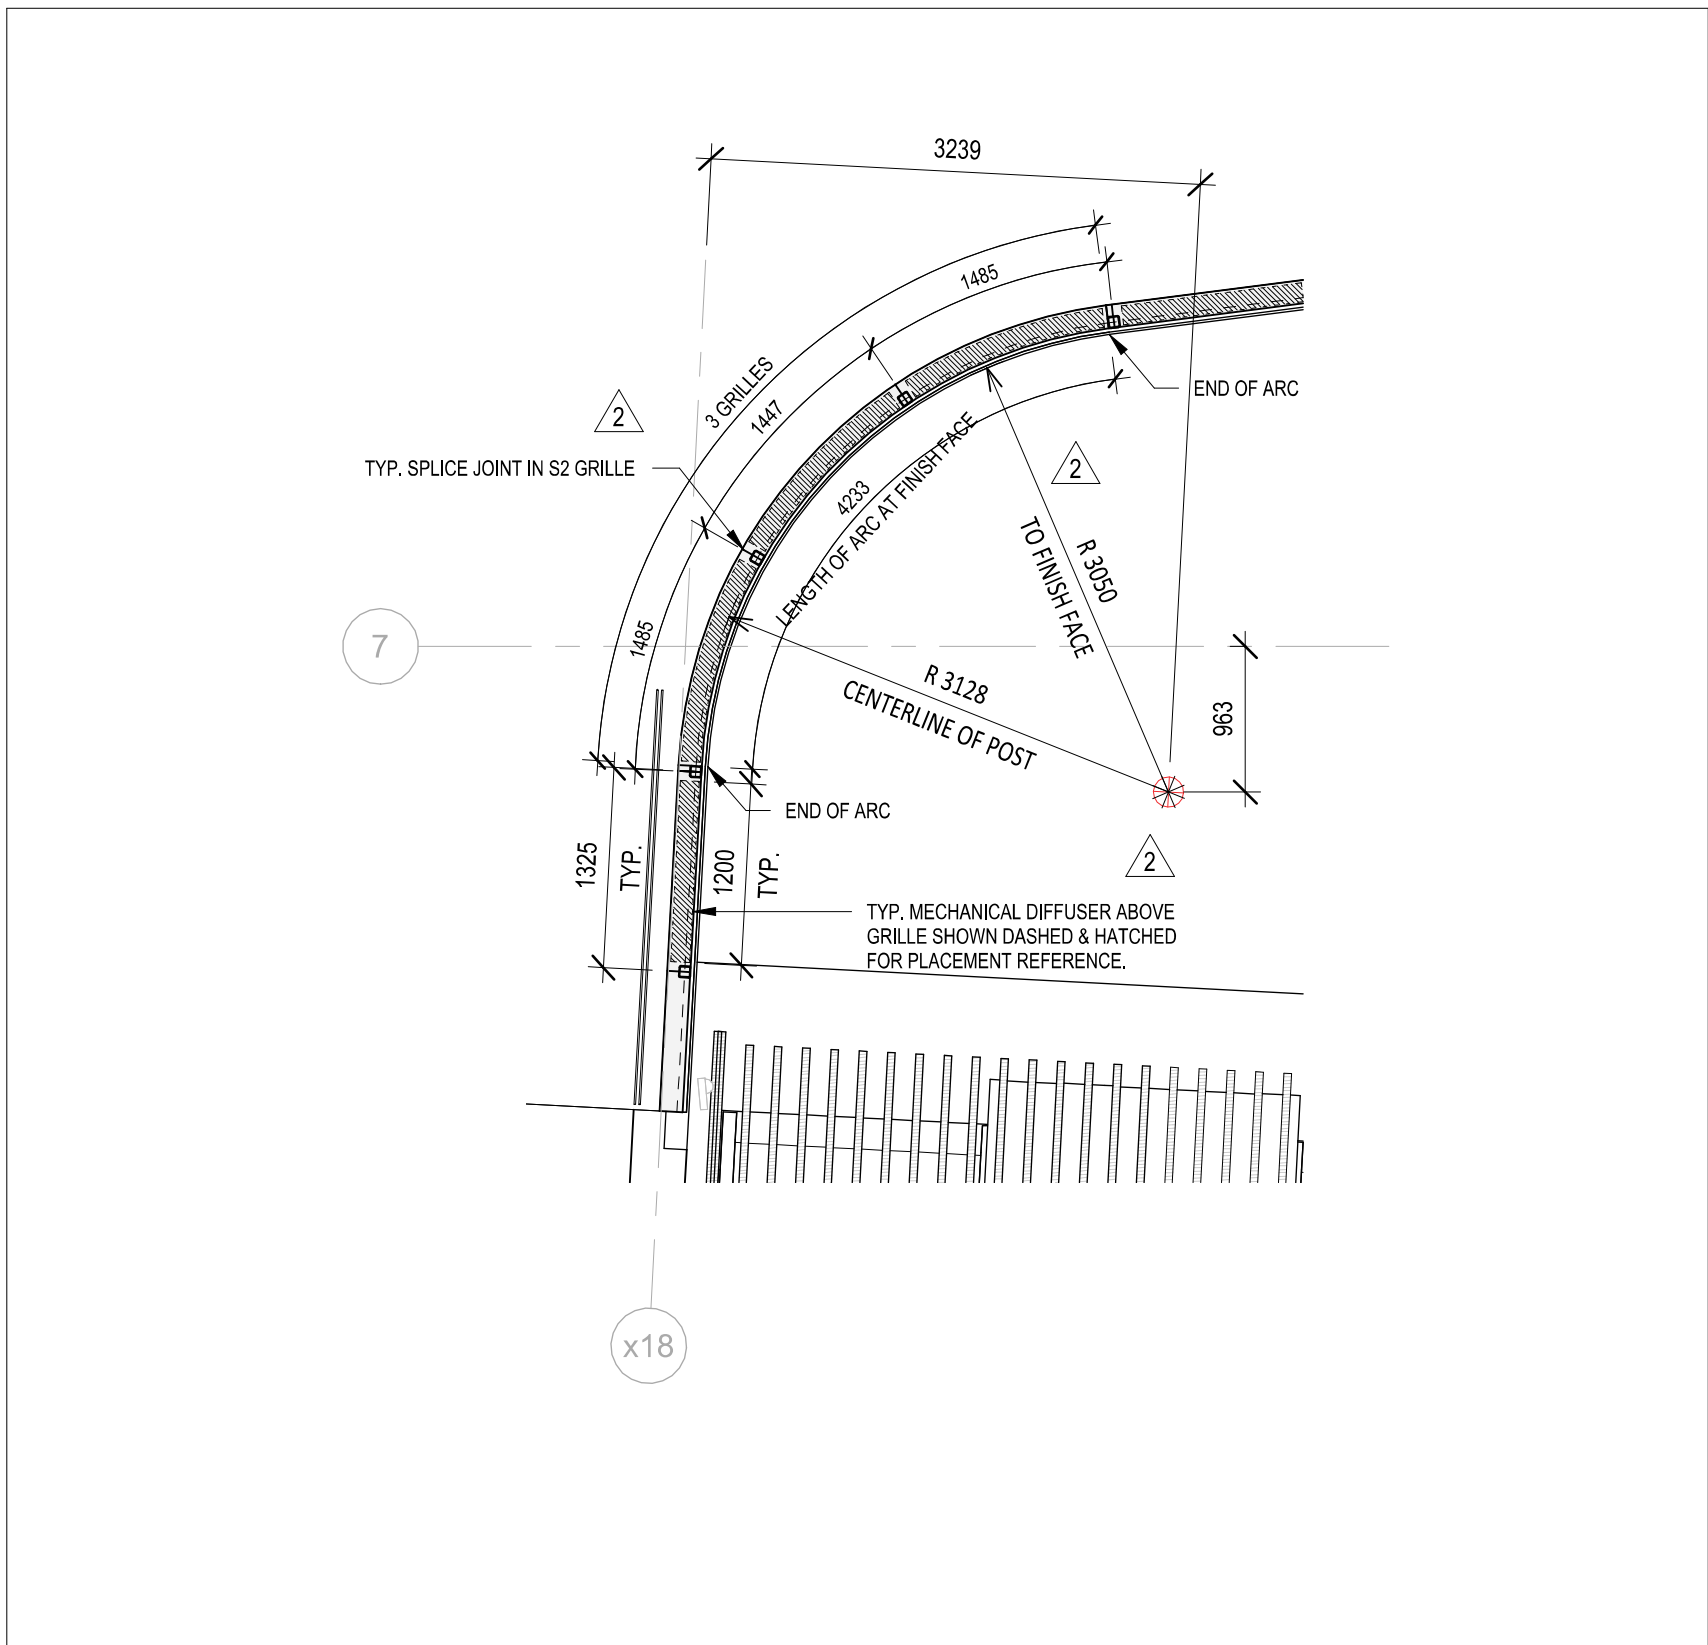

3 LEVEL 02 RCP - CEILING GRILLES - 3
A9.142 1:50

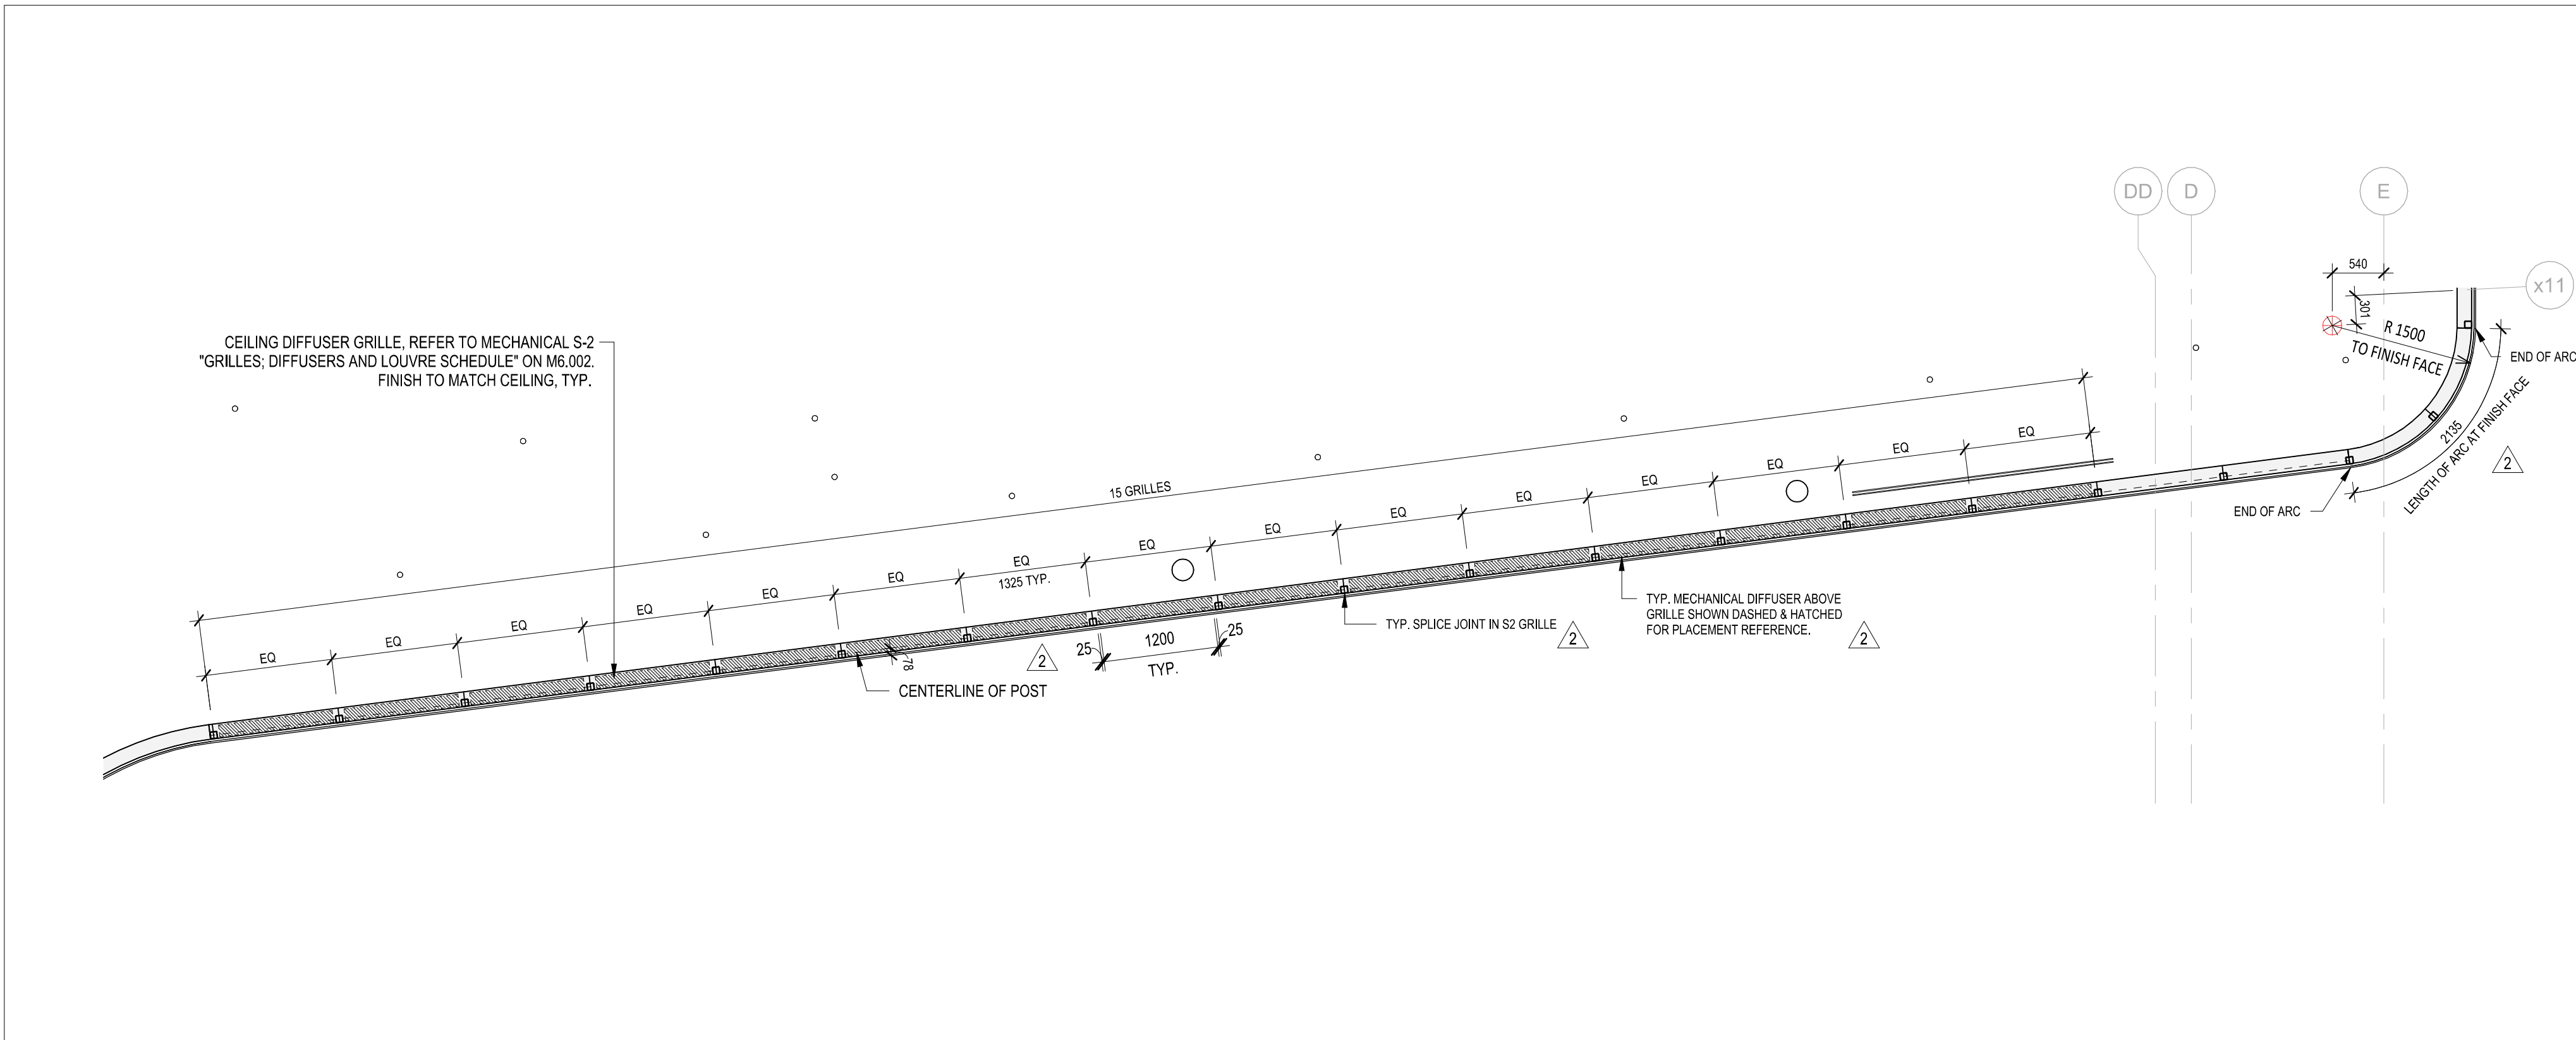

2 LEVEL 02 RCP - CEILING GRILLES - 2
A9.142 1:50

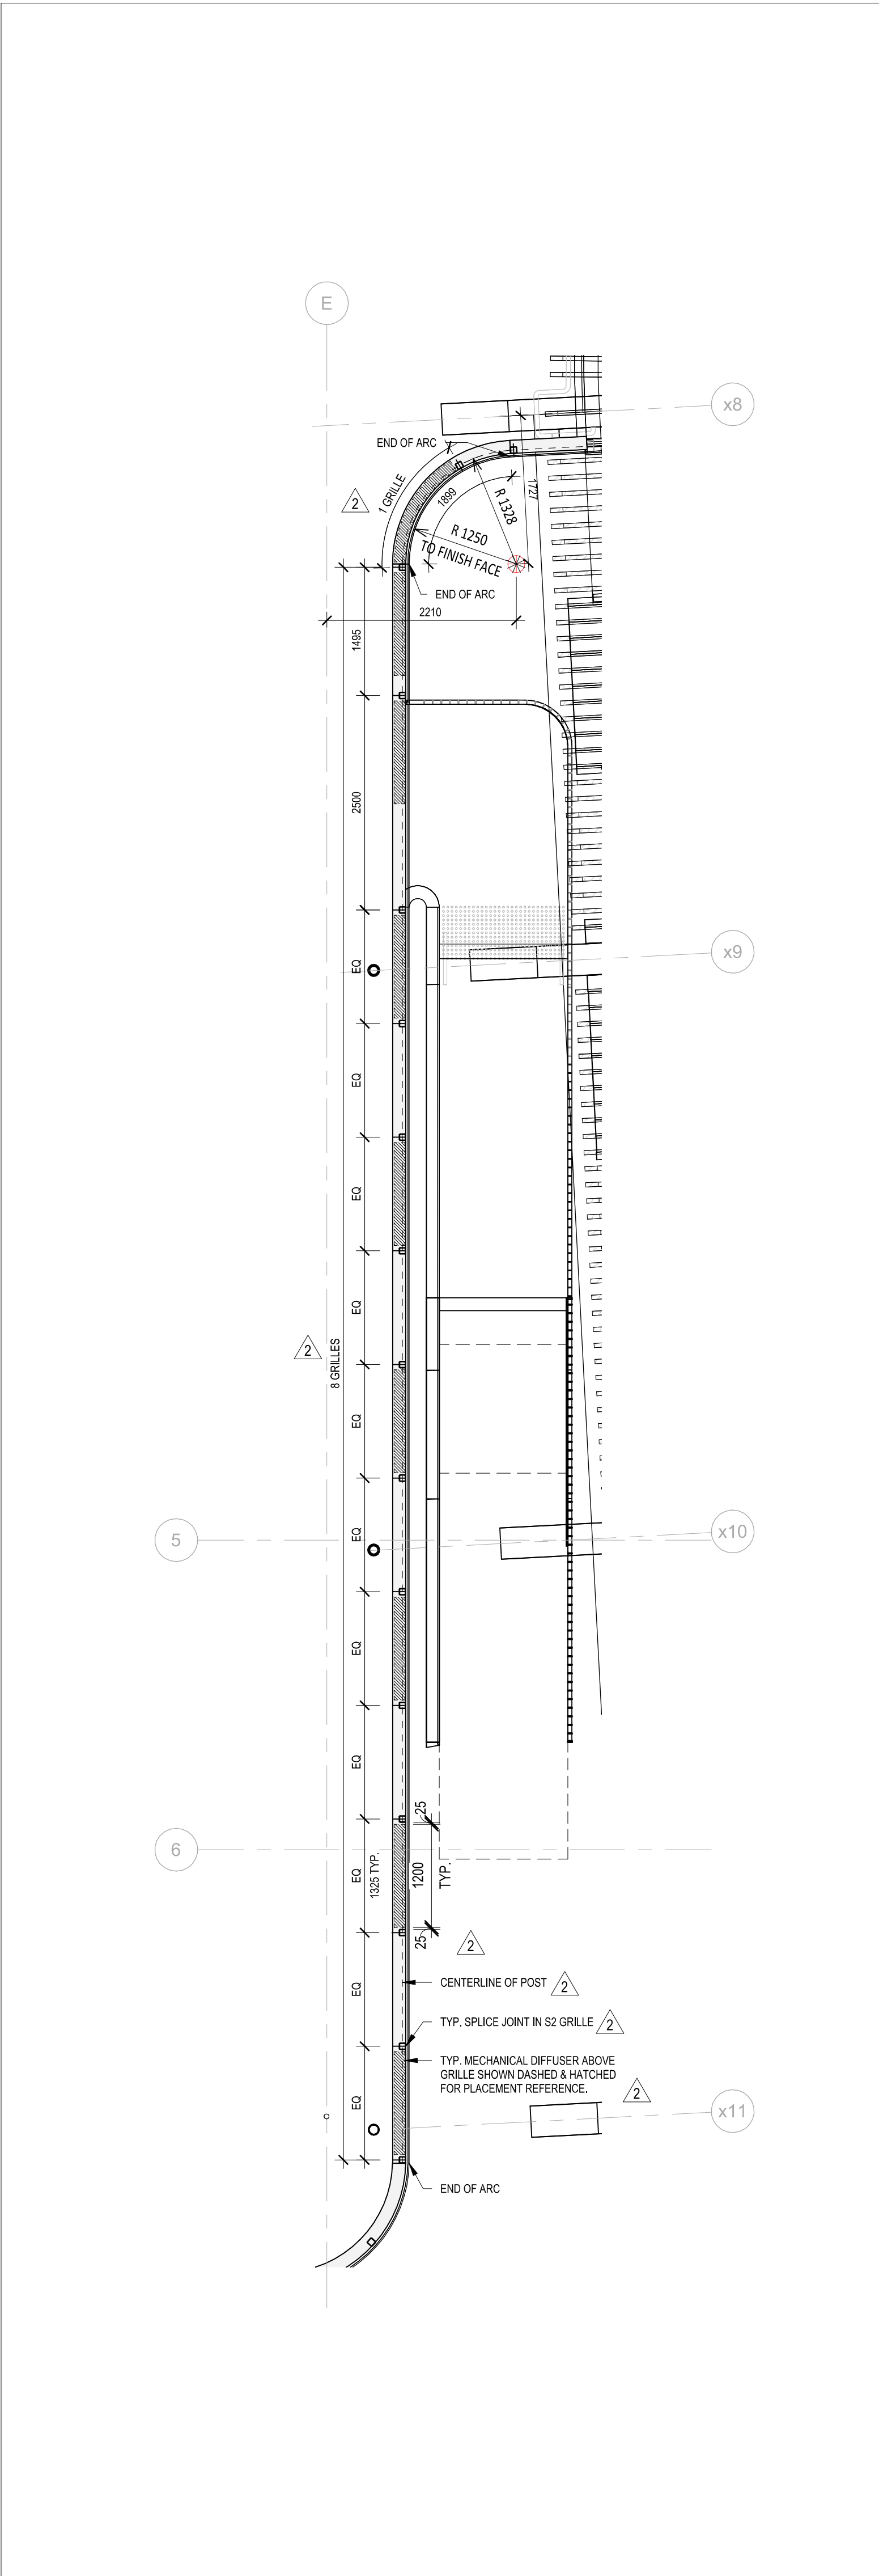


1 LEVEL 02 RCP - CEILING GRILLES - 1
A9.142 1:50

COPYRIGHT IS THAT OF THE ARCHITECT.
ANY USE OF THIS DRAWING REPRODUCED BY ANY
MEDIUM FOR ANY MEDIA WITHOUT THE WRITTEN
APPROVAL OF THE ARCHITECT IS TO BE HELD FOR
THE ARCHITECT IS NOT LIABLE FOR ANY LOSS OR
DAMAGE TO INFORMATION RESULTING FROM
SUBSEQUENT REPRODUCTION OF THE ORIGINAL DRAWING.

ARCHITECT'S NOTES:
1. DRAWINGS ARE NOT TO BE SCALED. CONTRACTOR SHALL
VERIFY ALL EXISTING CONDITIONS AND DIMENSIONS
BEFORE CONSTRUCTION. THE ARCHITECT SHALL BE
RESPONSIBLE FOR THE CONSTRUCTION WORK.
2. THE ARCHITECTURAL DRAWINGS ARE TO BE READ IN
CONJUNCTION WITH ALL OTHER CONTRACT DOCUMENTS,
INCLUDING THE PROJECT MANUAL AND THE STRUCTURAL,
MECHANICAL, AND ELECTRICAL DRAWINGS. IN CASE OF
CONFLICT, THE CONTRACT DOCUMENTS SHALL PREVAIL.
3. POSITIONS OF EXISTING OR PROPOSED MECHANICAL OR
ELECTRICAL EQUIPMENT SHALL BE INDICATED AS
LOCATIONS ON THE ARCHITECTURAL DRAWINGS SHALL GOVERN
OVER MECHANICAL AND ELECTRICAL DRAWINGS.
4. DIMENSIONS INDICATED ARE TAKEN BETWEEN THE FACES
UNLESS OTHERWISE NOTED.
5. THE ARCHITECT HAS NOT BEEN RETAINED FOR
SUPERVISION OF CONSTRUCTION AND ASSUMES NO
RESPONSIBILITY FOR MEANS, METHODS AND TECHNIQUES
OF CONSTRUCTION.
6. THESE DOCUMENTS HAVE NOT TO BE USED FOR
CONSTRUCTION UNLESS SPECIFICALLY NOTED FOR SUCH
PURPOSE.

1	2025-05-03	ISSUED FOR CONSULTATION
2	2025-05-03	ISSUED FOR REVIEW
3	2025-05-07	ISSUED FOR TENDER PACKAGE 2

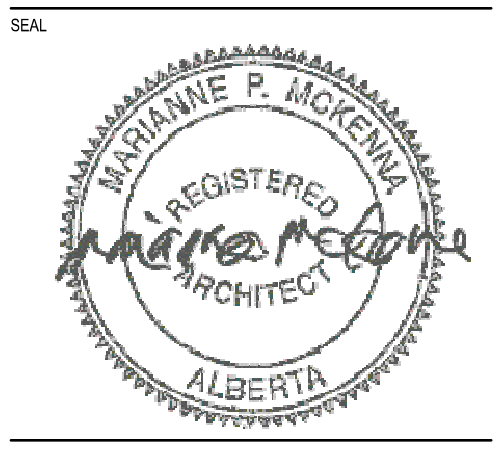

ARCHITECTS

KPMB

KPMB Architects
351 King Street East, Suite 1200
Toronto, Canada M5A 0L6
+1 416 577 5104
kpmb@kpmbarchitects.com

HINDLE ARCHITECTS


Hindle Architects
Suite 510, Burns Building
237 8th Avenue SE
Calgary, AB
T2G 0C3

CMILC

Arts Commons Transformation
Phase 1 Expansion

ACT

206 8th Avenue S.E. Calgary, Alberta

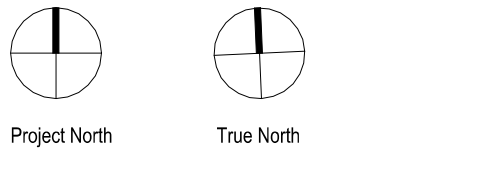

Project No: 2041
Scale: As indicated
Plot Date: 01/05/25

LEVEL 2 - GRILLE
SCHEDULE RCP